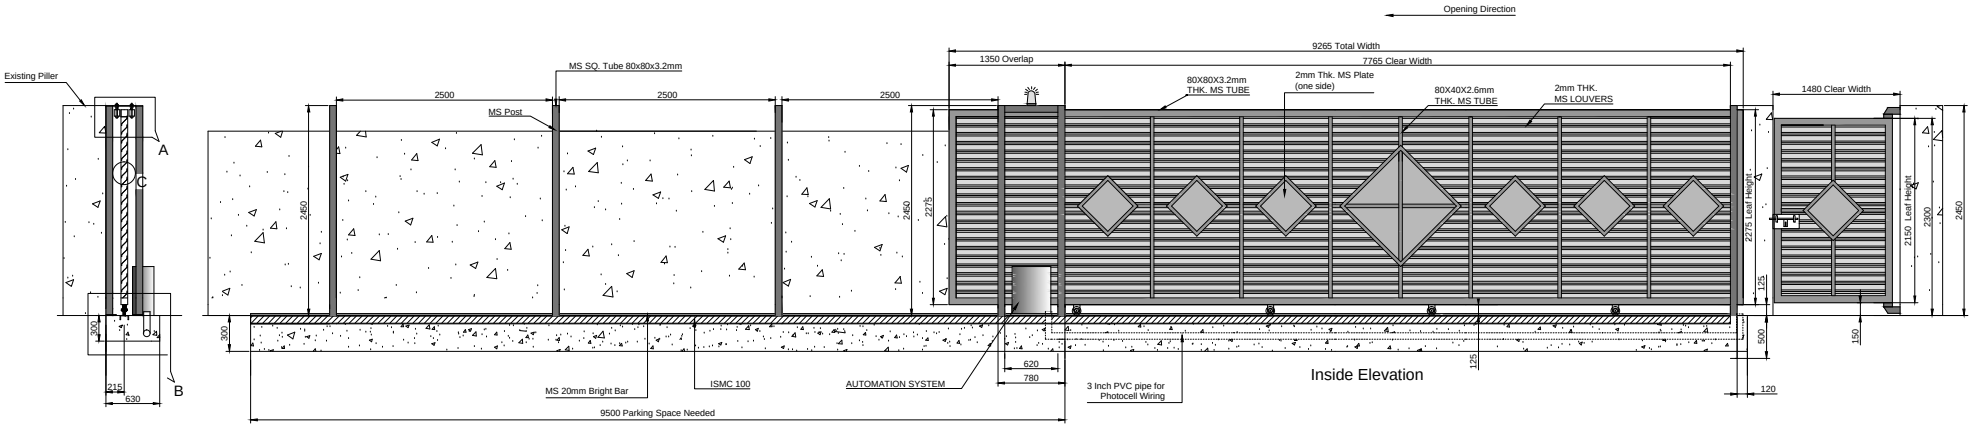


SR NO	TUBE SPECIFICATION	
1	80X80X3.2mm	OUTER TUBE
2	80X40X2.6mm	INTERMEDIATE TUBE
3	2mm THK. MS SHEET	FOR LOUVERS
4	2mm THK. MS SHEET	MIDDLE SHEET

SR NO	CLEAR WIDTH	CLEAR HEIGHT	QUANTITY
1	7765mm	2400mm	1 NOS
2	1480mm	2300mm	1 NOS

Power supply - Single phase 230V, 50 Hz.
Cable for power supply- 1.5 sqmm 3 core
Cable for Photocell - 0.5 sqmm 4 core, length- 12m

Note- All required civil work will be client's scope.
One coat of red oxide & two coats of approved RAL shade will be given to the gate.
Final finishing will be done on site itself.All required supply & supply cables will be in Client's scope.

This drawing & designing is the property of NIHVA TECHNOLOGIES. Not to be sold or copied to any other concern.

TITLE
Motorized Sliding gate
7.765x2.4m & Wicket gate

NIHVA TECHNOLOGIES PVT. LTD.
NIHVA TECHNOLOGIES PVT. LTD. PUNE
Tel : 020 66304033
Email:- info@nihva.com
Website:- www.nihva.com

	SIGN	DATE
DRAWN	Omkar	06/02/18
CHECK	Shekhar	06/02/18
APPROVAL	Shekhar	06/02/18

CLIENT - DEV TECNOSKILL
PROJECT - AMAR TEA
SITE LOCATION - UMARGAON, GUJARAT
DWG. NO. : NIHVA/17-18/0354 | Rev- 0
If any queries contact : design@nihva.com
SCALE: NTS | WT: | SHEET: 01 OF 01
ALL DIMENSION ARE IN mm