

NOTE : ~ PLEASE MAINTAIN 7 MM GAP BETWEEN TWO LIP BUSHES.

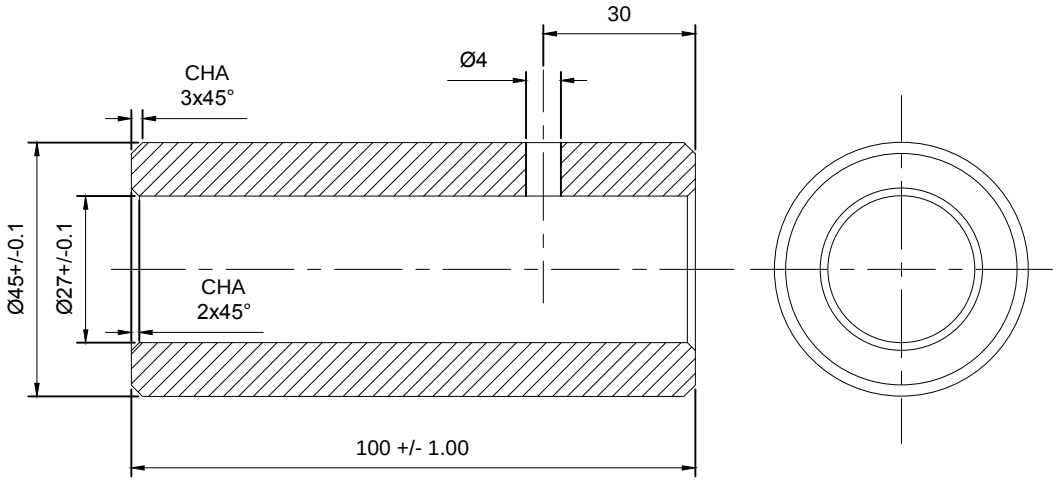

NOTE:~ MTL : MS

BUSH Ø45 X 103L = 50 NOS

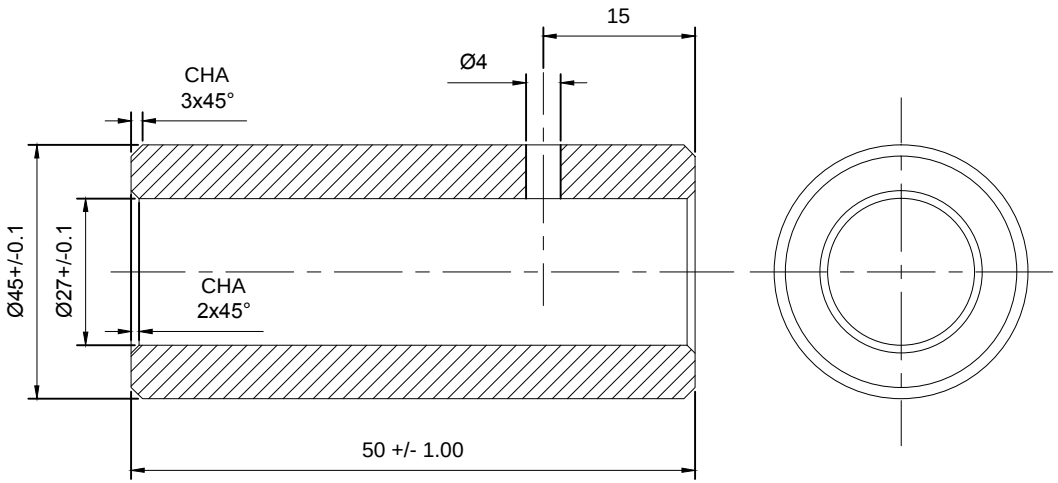

NOTE:~ MTL : MS

BUSH Ø45 X 53L = 50 NOS

This drawing & design is the property of NIHVA TECHNOLOGIES. Not to be sold or copied to any other concern.

TITLE: LIP MOUNTING BUSH			NIHVA TECHNOLOGIES PVT. LTD. PUNE Tel : 020 66304033 Email:- info@nihva.com Website:- www.nihva.com
	NAME	SIGN	DATE
DRAWN	P.V.A		17.10.2019
CHECK	V.M.T		17.10.2019
APPRD.			
If any queries contact : design@nihva.com			
ALL DIMENSION ARE IN mm			

CLIENT -

PROJECT - NDL451

SITE LOCATION -

DWG. NO. : NIHVA/19-20/VDR/286

SCALE: NTS | WT: | REV- 0