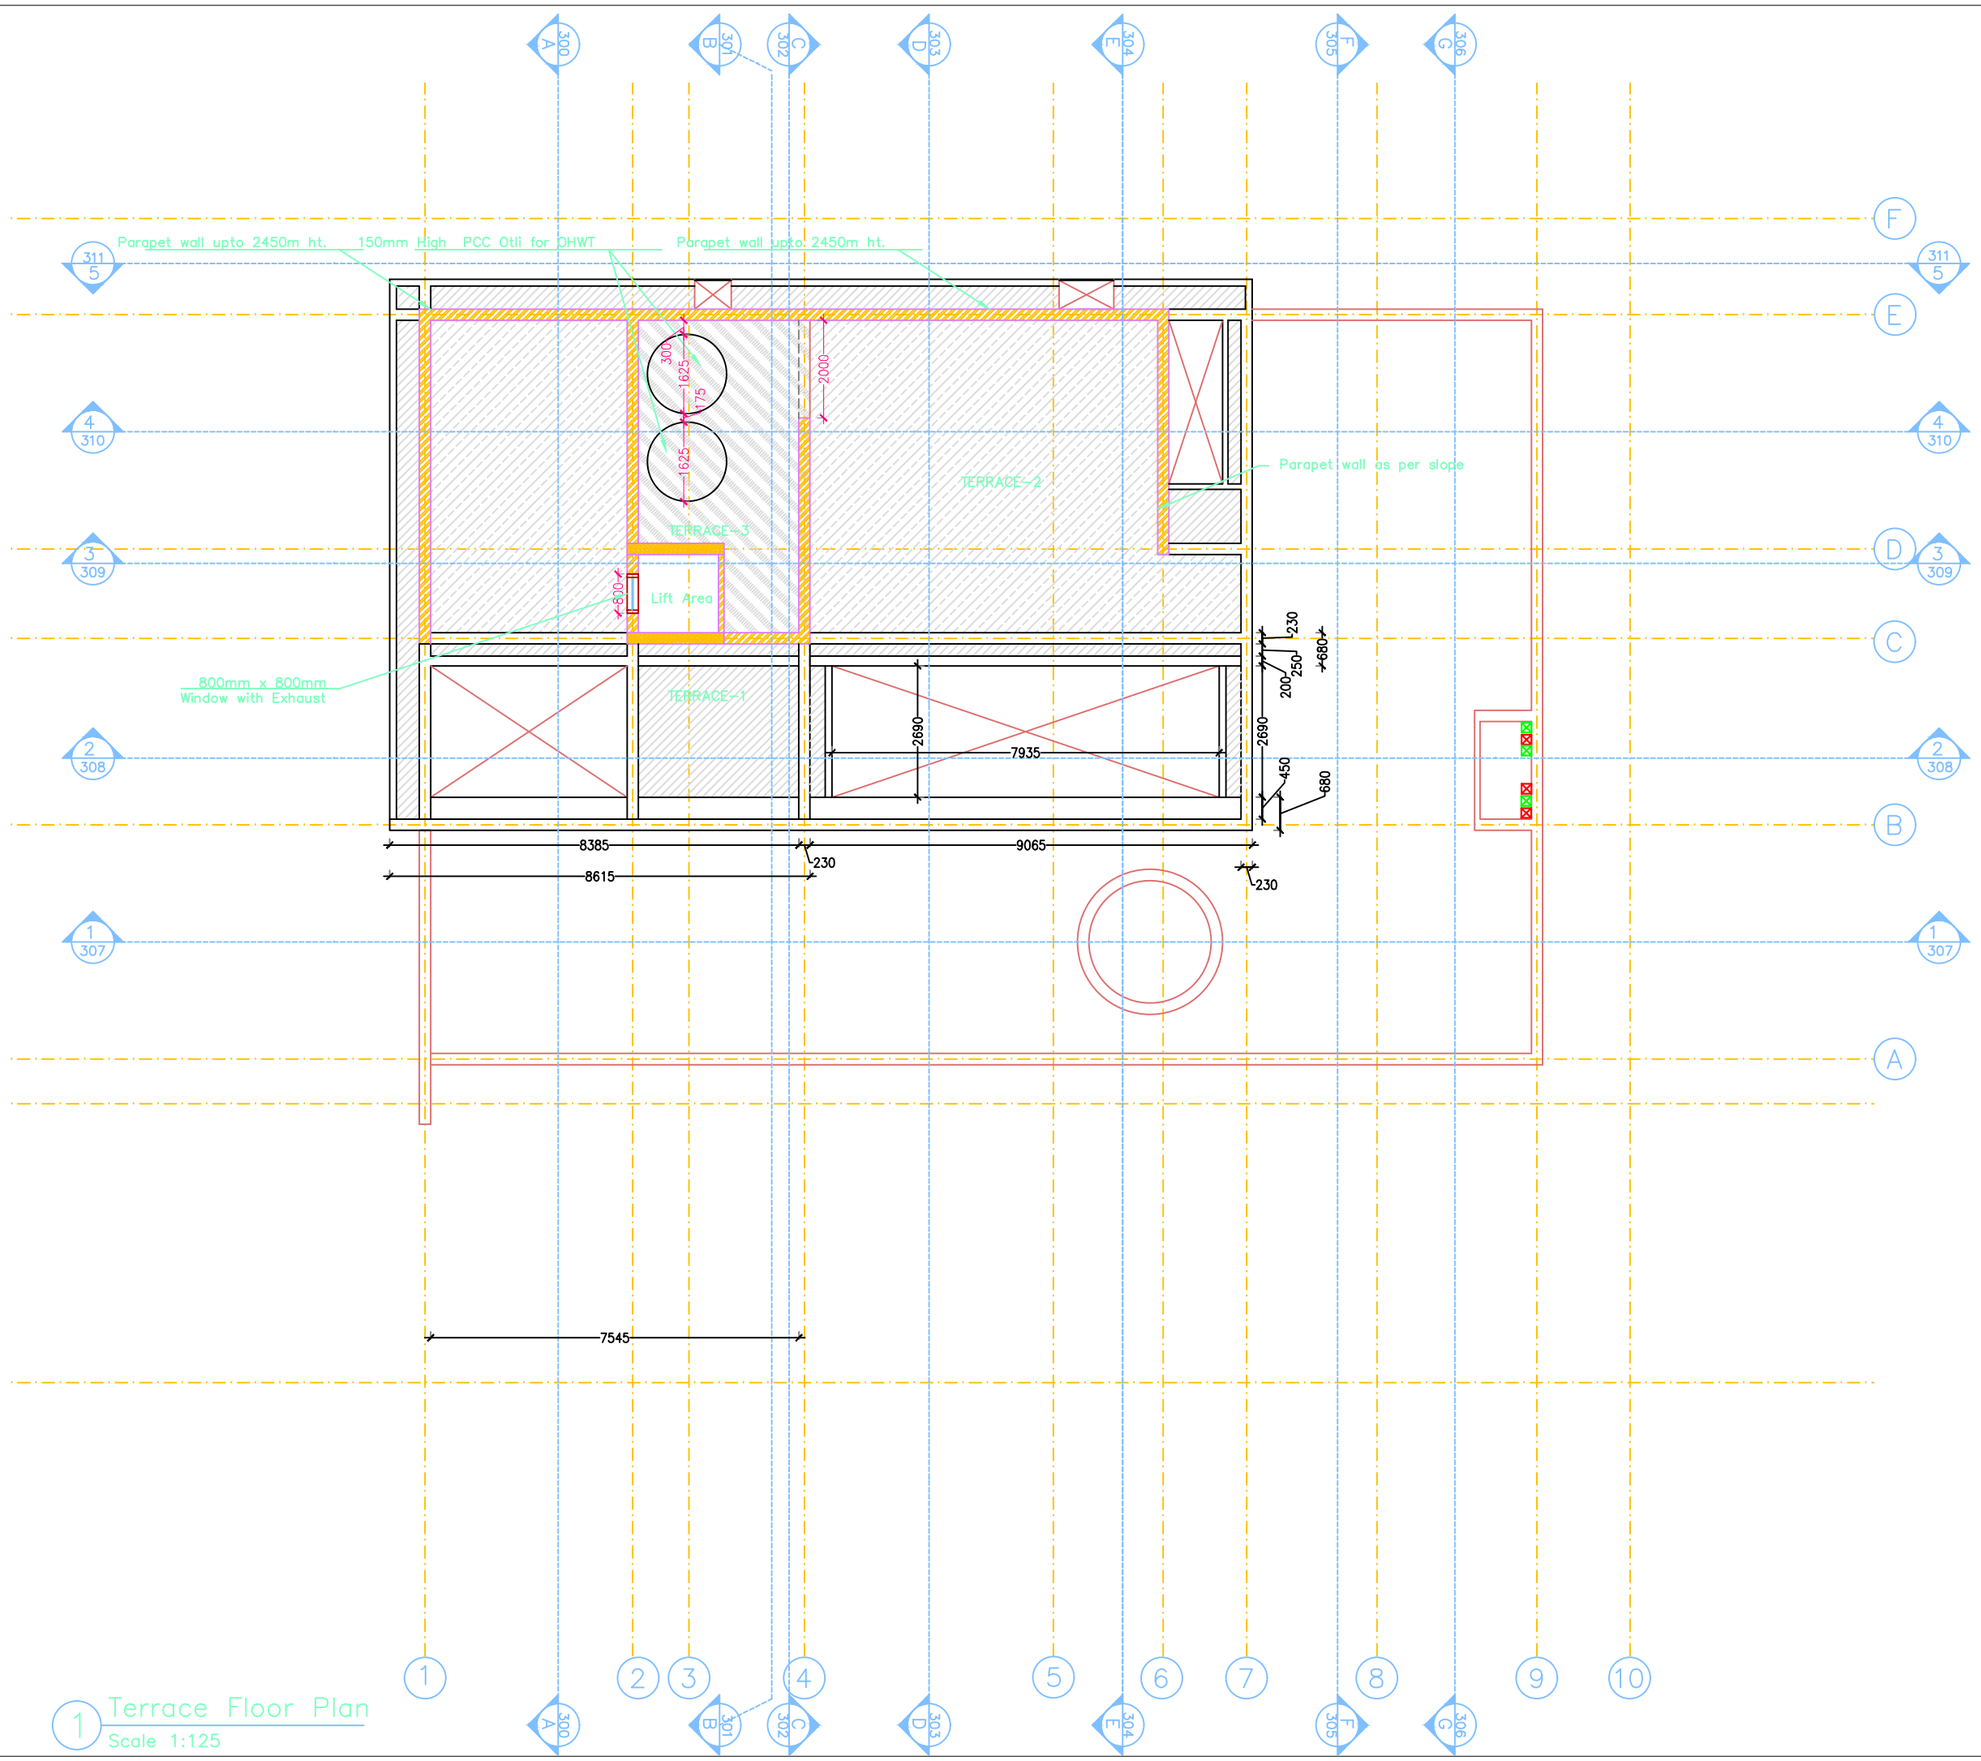


1 Terrace Floor Plan
Scale 1:125

PLOT DATE /TIME: 2023-02-15 14:55:12
DESIGN FILE : 200908-A-P-103_00

Notes:
1. All dimensions are in MM. Do not scale
2. Contractor to Check all dimensions and report omissions and errors to the Architect

Drawing Revision Table

No	Revision	Date	Initial	Chkd

Drawing Issue Table

Date	Issued to	Mode	Purpose

LEGEND

- TERRACE-1 (From road Level) LVL +12.710
- TERRACE-2 (From road Level) LVL +13.010
- TERRACE-3 (From road Level & space for OHWT & its services) LVL +13.160

NOTE: This drawing and the design it covers is the property of PVDRS. It is merely loaned on the borrower's express agreement that it will not be reproduced, copied, loaned, exhibited nor used except in a limited way and private use as permitted by any written consent given by the lender to the borrower.

Firm Name
PVDRS

Project Name
Bhattacharya House

Project Location
Ahmedabad

Drawing Title
Terrace Floor Plan

Purpose	25/04/2022
For Construction	Drg by: HM Chk by: KV

Drawing Number: 200908-A-P-103
Revision Number: 00