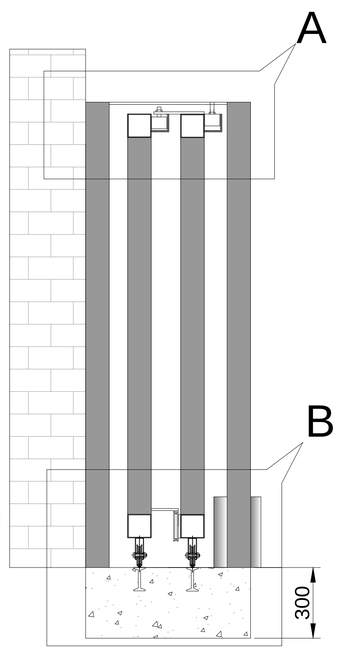
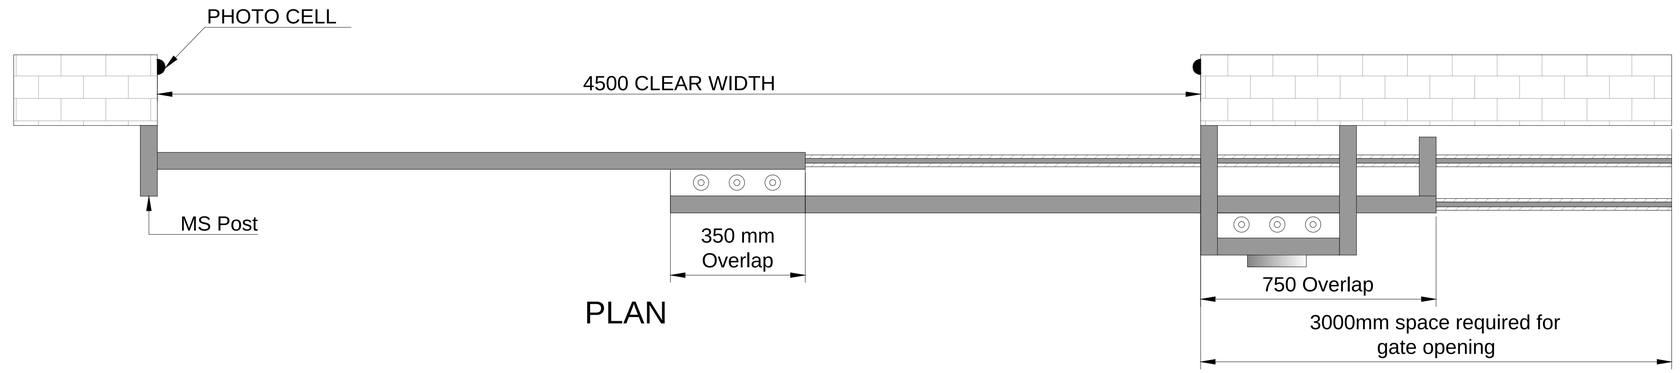


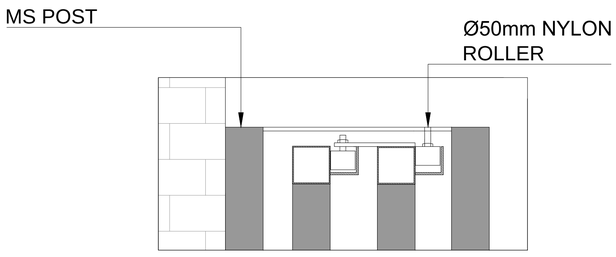

INSIDE ELEVATION



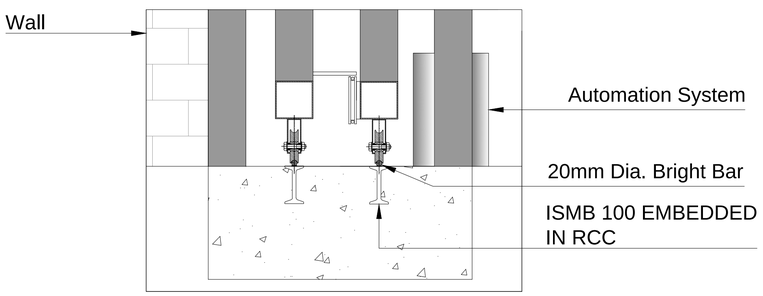

SIDE VIEW




PLAN




DETAILED VIEW A




DETAILED VIEW B

This drawing & designing is the property of NIHVA TECHNOLOGIES. Not to be sold or copied to any other concern.

| | | |
|---|---|---|
| TITLE | 2 LEAF TELESCOPIC GATE 4500X1800mm | |
| | SIGN | DATE |
| DRAWN | OMKAR | 14/03/17 |
| CHECKED | SAGAR P. | 14/03/17 |
| REV. | | |
| APPROVED | R.K. | 14/03/17 |

NIHVA TECHNOLOGIES PVT. LTD.
NIHVA TECHNOLOGIES PVT. LTD. PUNE
Tel : 020 66304033
Email:- info@nihva.com
Website:- www.nihva.com

CLIENT - SHIMZU CORPORATION INDIA PVT.LTD.

PROJECT - GSK

SITE - KOLAR, KARNATAKA

DWG. NO. : NIHVA/16-17/177

If any queries contact : projects@nihva.com

SCALE: NTS | WT: | SHEET: 01 OF 01

ALL DIMENSION ARE IN mm