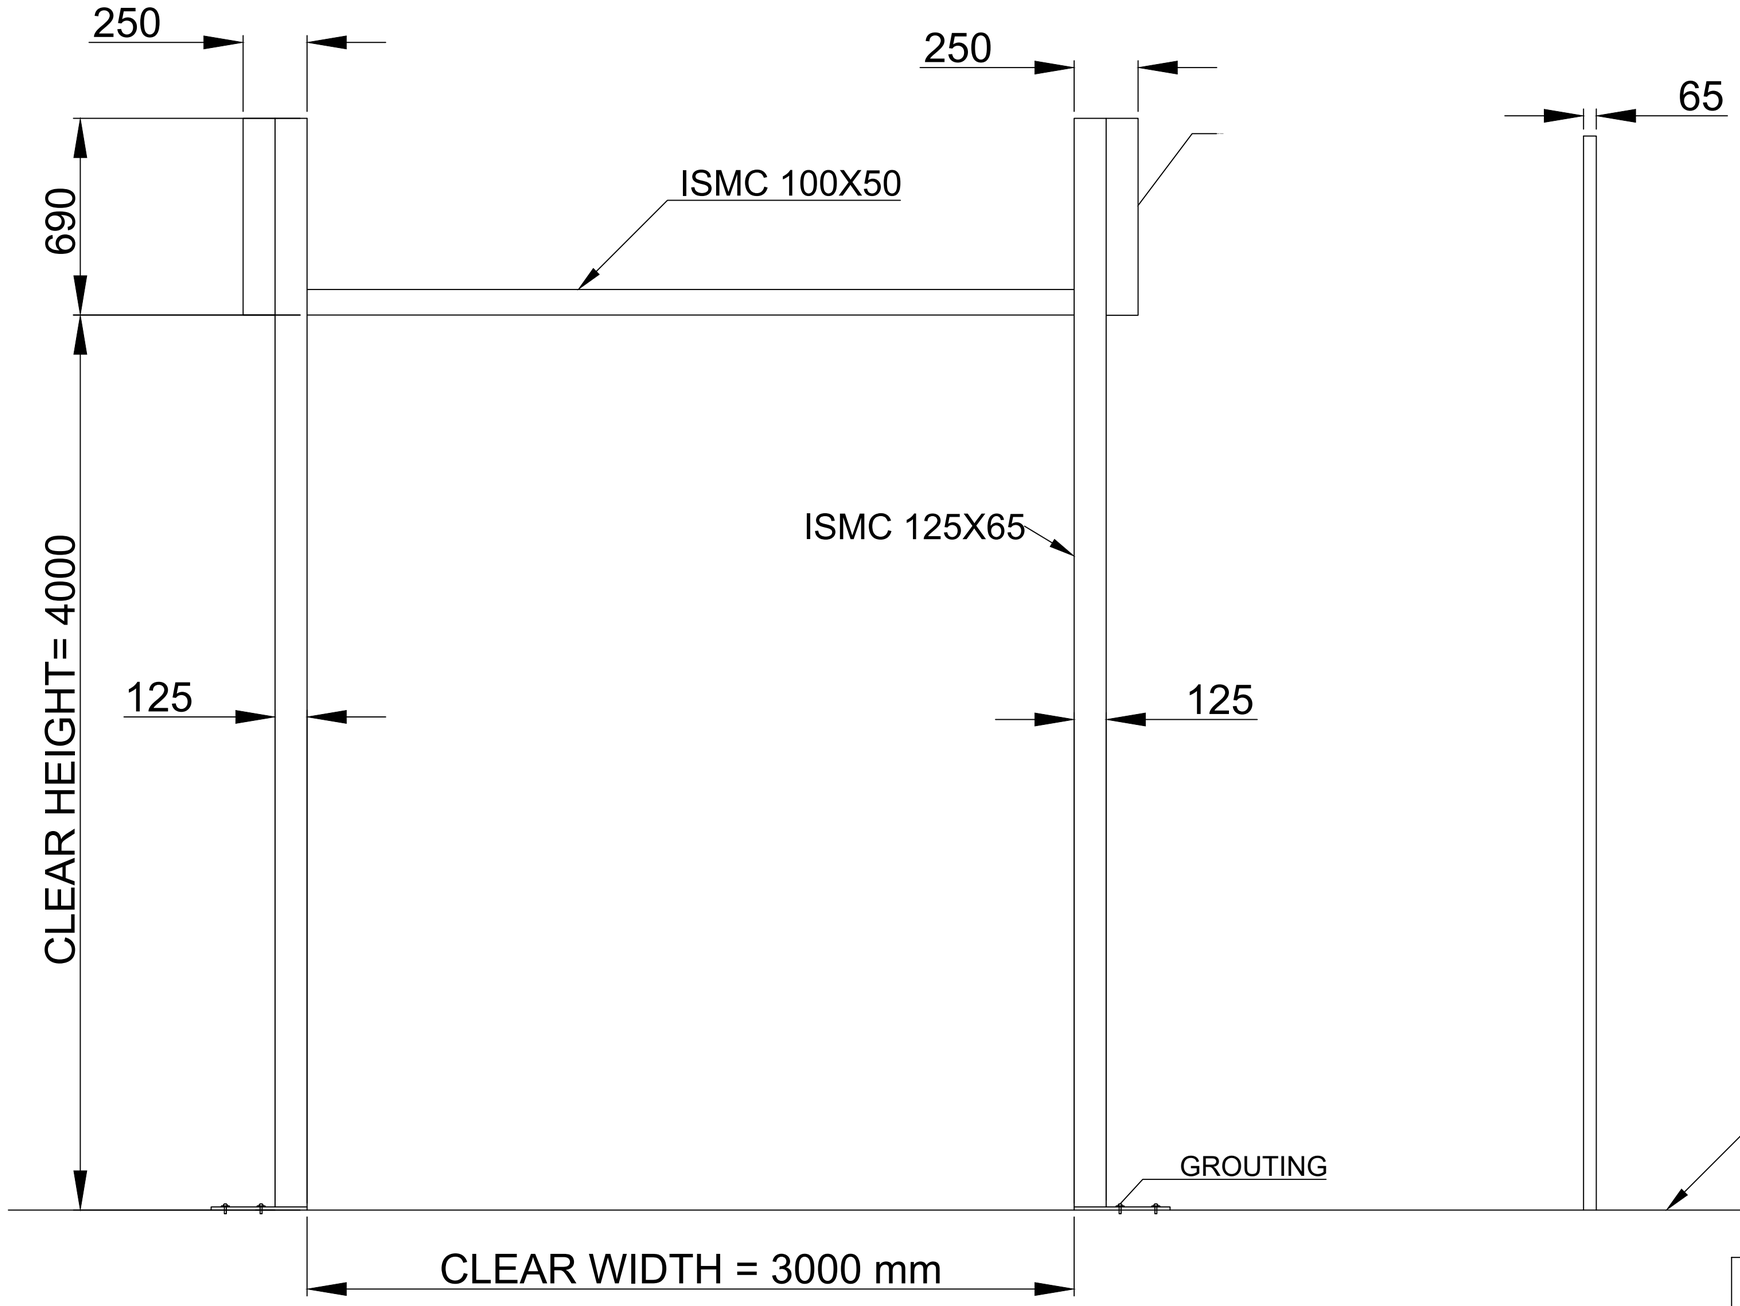


QTY : 1 NO

NOTE -
(1) ALL REQUIRED TECHNICAL MS STRUCTURE & FITTING IN CLIENT SCOPE .
(2) ALL CIVIL WORK IN CLIENT SCOPE .

This drawing & design is the property of NIHVA TECHNOLOGIES. Not to be sold or copied to any other concern.

TITLE	ALUMINUM HIGH SPEED ROLLING SHUTTER STRUCTURE DWG			NIHVA TECHNOLOGIES PVT. LTD.
	NAME	SIGN	DATE	
DRAWN	MAHESH S.		24.08.2022	CLIENT - AMULYA TRADERS
CHECK	MAHESH S.		24.08.2022	PROJECT - JOHN DEERE
APPRD.	AMIT K.		24.08.2022	SITE LOCATION - PUNE

NIHVA TECHNOLOGIES PVT. LTD. PUNE
Tel : 020 66304033
Email:- info@nihva.com
Website:- www.nihva.com

If any queries contact : projectsupport@nihva.com	DWG. NO. : NIHVA/22-23/MFG/0070		REV- 0
ALL DIMENSION ARE IN mm	SCALE: NTS	WT:	SHEET: 01 OF 01