

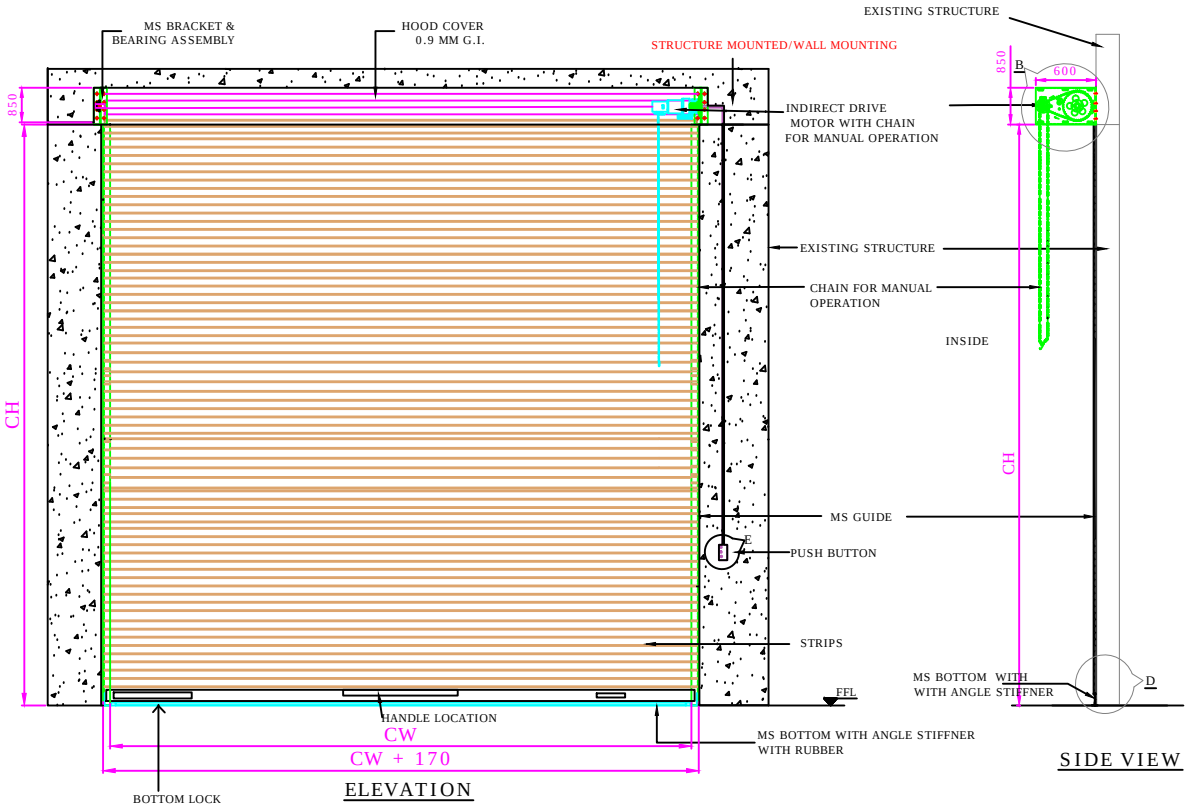


ELEVATION


SIDE VIEW

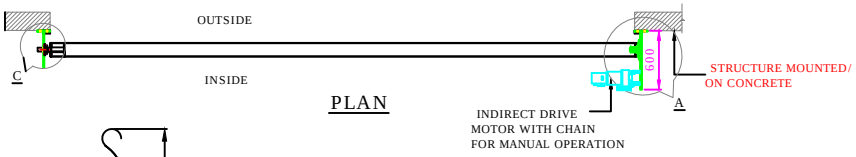


PLAN

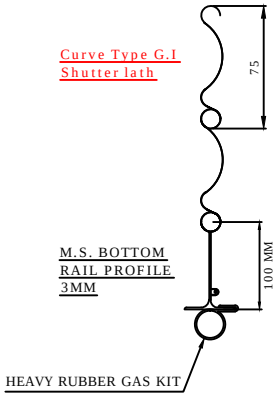

DETAILS : D

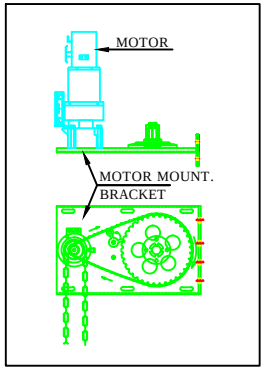


DETAILS : A & B

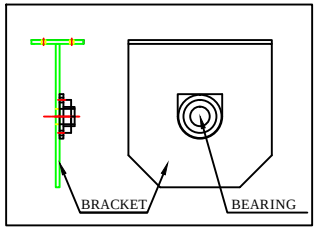

DETAILS : C

NOTE:
(1) IF REQUIRED M.S.TECHNICAL STRUCTURE & FITTING IN CLIENT SCOPE.
(2) ALL CIVIL WORK IN CLIENT SCOPE.
(3) SHUTTER WILL BE ONLY INSTALLED AFTER STRUCTURE READY AS PER DRAWING PROVIDED IF REQUIRED .
(4) PLEASE REFER FOLLOWING TABLE & MENTION YOUR REQUIREMNT IN TABLE.

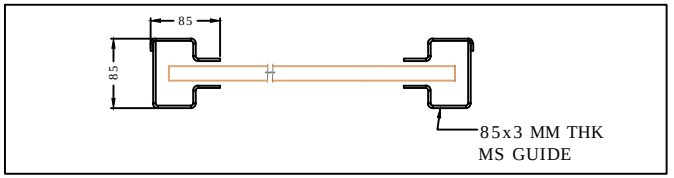

SR NO	PARAMETER	DESCRIPTION	CUSTOMER REMARK
1	SHUTTER MOUNTING	ON STRUCTURE / ON CONCRETE	
2	SURFACE FINISH	RAL CODE FOR POWDER COATING	

RAL CODE	SHADE	COLOUR
RAL 9001	CREAM	
RAL 9002	GREY WHITE	
RAL 9010	PURE WHITE	
RAL 5002	ULTRAMARINE BLUE	
RAL 7035	LIGHT GREY	
RAL 7001	SILVER GREY	

3400	3950	2	
CLEAR WIDTH (CW)	CLEAR HEIGHT (CH)	QUANTITY	RAL COLOR POWDER COATED

This drawing & design is the property of NIHVA TECHNOLOGIES. Not to be sold or copied to any other concern.

TITLE: MOTORIZED ROLLING SHUTTER

	NAME	SIGN	DATE
DRAWN	S.M.S.		9.11.2020
CHECK	K.P.		9.11.2020
APPRD.			

NIHVA TECHNOLOGIES PVT. LTD.
NIHVA TECHNOLOGIES PVT. LTD. PUNE
Tel : 020 66304033
Email:- info@nihva.com
Website:- www.nihva.com

CLIENT - SEZ BIOTECH SERVICES PVT LTD

PROJECT - SEZ BIOTECH SERVICES PVT LTD

SITE LOCATION - PUNE

If any queries contact : projectsupport@nihva.com

DWG. NO. : NIHVA/20-21/0082 REV- R00

ALL DIMENSION ARE IN mm | SCALE: NTS | WT: | SHEET: