

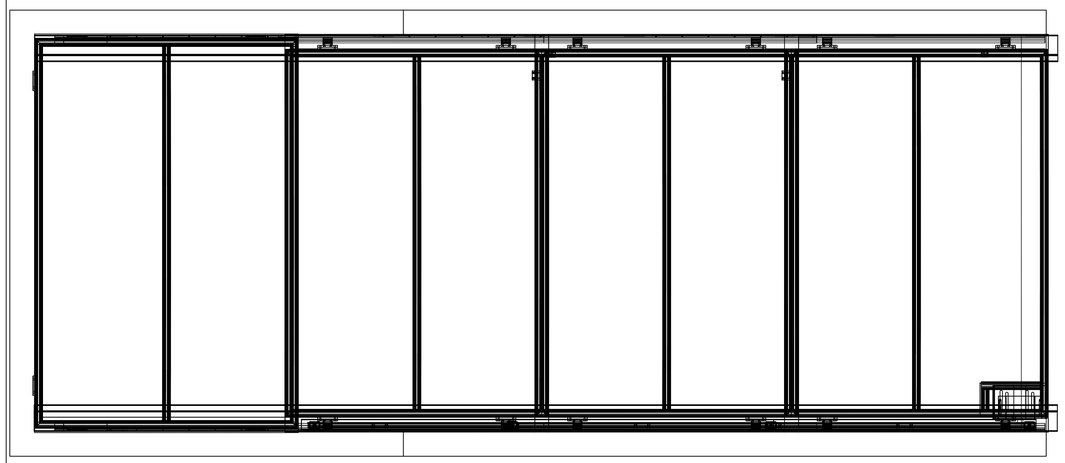


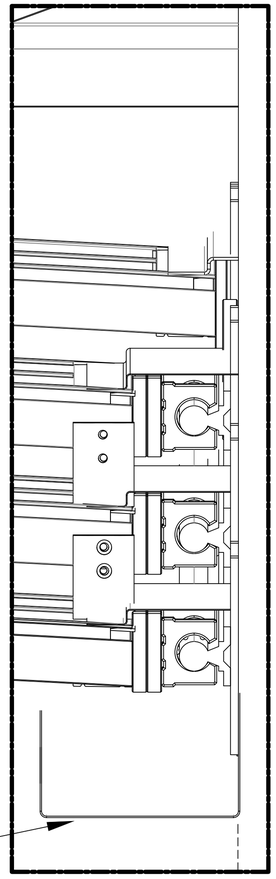


DRAINAGE GUTTER

DETAIL - "A"


FLASHING AROUND 3 SIDES - TO AVOID LEAKAGE

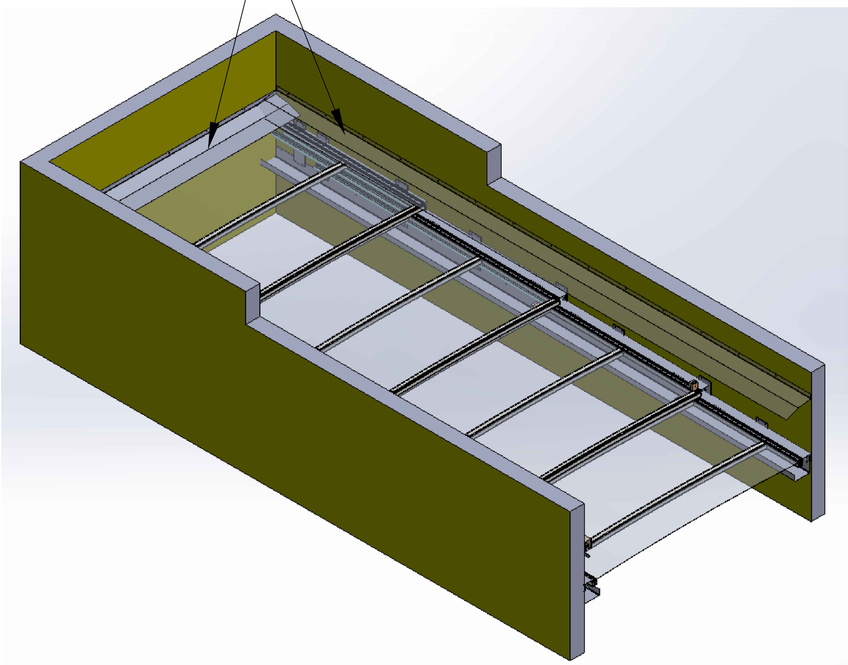


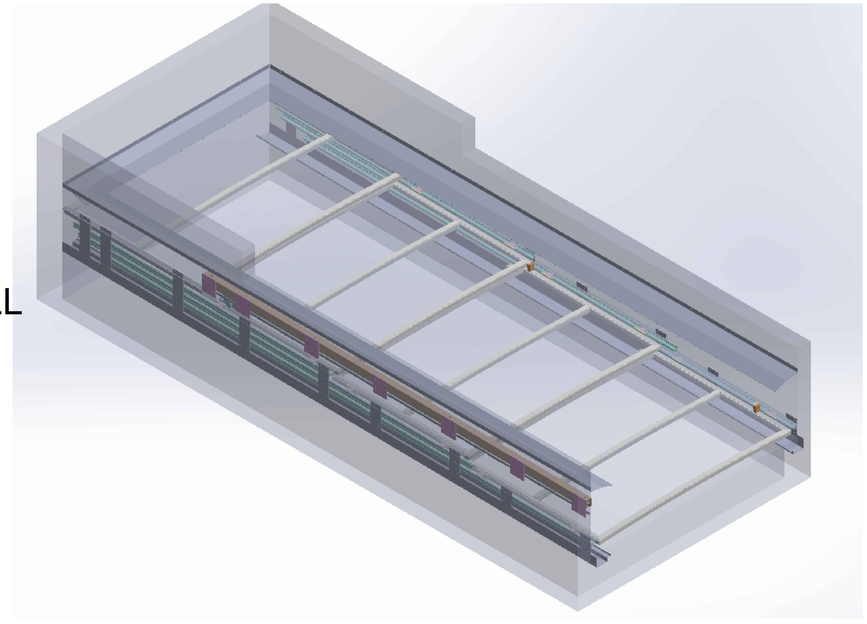

FLASHING AROUND 3 SIDES

WALL

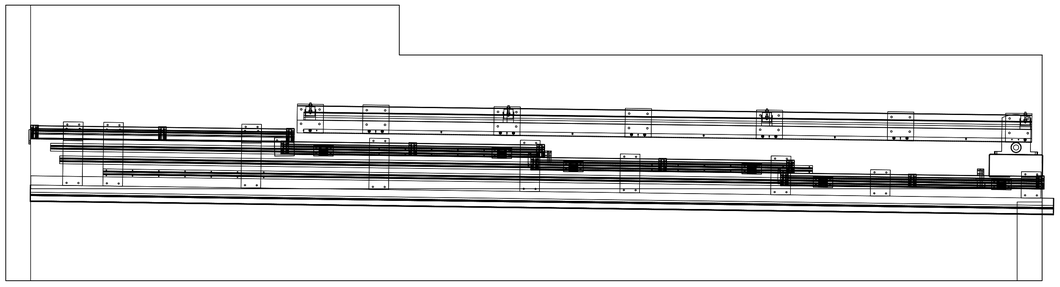


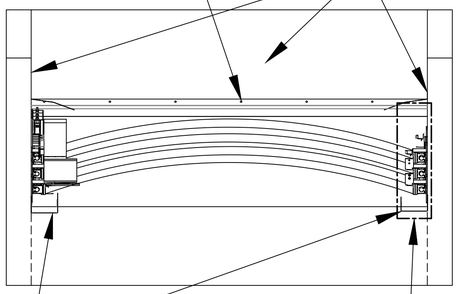

DRAINAGE GUTTER

SEE DETAIL - "A"

REV NO.	DESCRIPTION	Date	Revised By

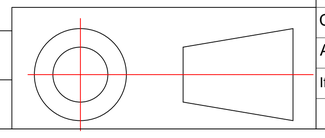

±0.90

TITLE:-

WALL MOUNT REF DWG

	NAME	DATE	SIGN
DRAWN	MAHESH S.	16/12/22	
CHECK	MAHESH S.	16/12/22	
APPRD.	VIJAY T.	16/12/22	

NIHVA TECHNOLOGIES PVT. LTD.

NIHVA TECHNOLOGIES PVT. PUNE
Tel : 020 66304033
Email:- info@nihva.com
Website:- www.nihva.com

CLIENT - NIHVA TECHNOLOGIES PVT.LTD

LOCATION - HYDERABAD

PRODUCT: WALLMOUNT- RETRACTABLE ROOF

If any queries contact : design@nihva.com | DWG NO:-NIHVA/22-23/ref | REV- 0

ALL DIMENSION ARE IN mm | SCALE: NTS | SCALE:-- 1:1 | SHEET: 01 OF 01