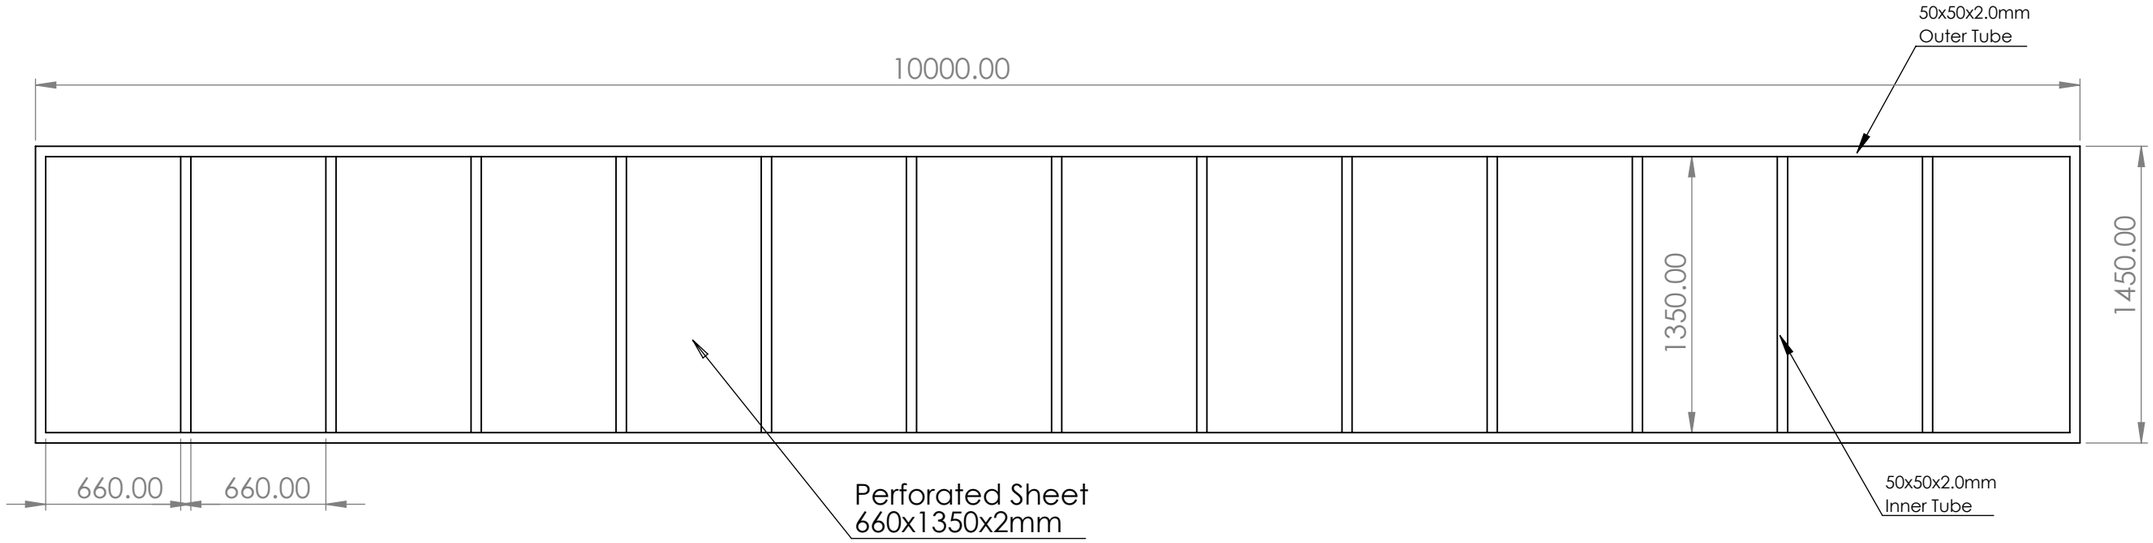

Note :

1. **Perforated Sheet To Weld After Bending.**
2. **Weld Only From Back Side.**

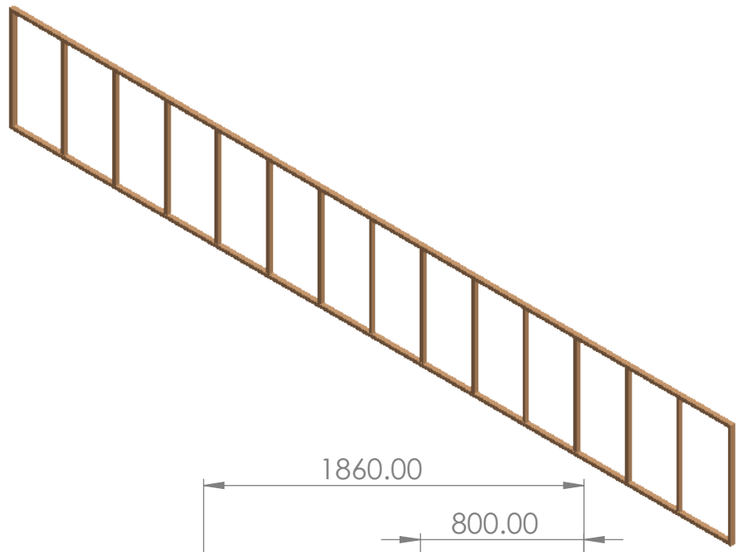

TITLE - Gate Outer Frame				NIHVA TECHNOLOGIES PVT.LTD.PUNE Website - www.nihva.com
	NAME	SIGNATURE	DATE	CLIENT - Reward
DRAWN	S.J		04.03.2024	PRODUCT -
CHK'D	A.K		04.03.2024	SITE LOCATION -
APPV'D	V.T		04.03.2024	QTY - 01 NOS
if any queries contact - design2@nihva.com				DWG NO - NIHVA/23-24/NTPL-218/01000 / REVISION -
ALL DIMENSION ARE IN mm		A3		SCALE - / SHEET 1 OF 1