




SLIDING ROLLER DETAIL 'A'

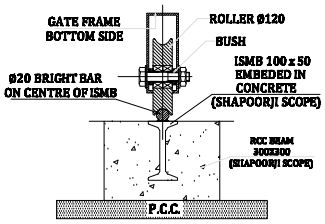


SLIDING ROLLER DETAIL 'A'

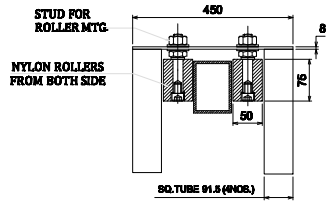



SLIDING BRACKET DETAIL 'B'

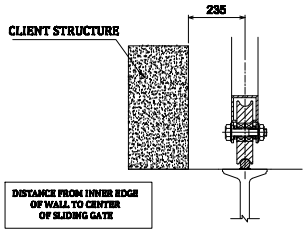


DETAIL 'C'

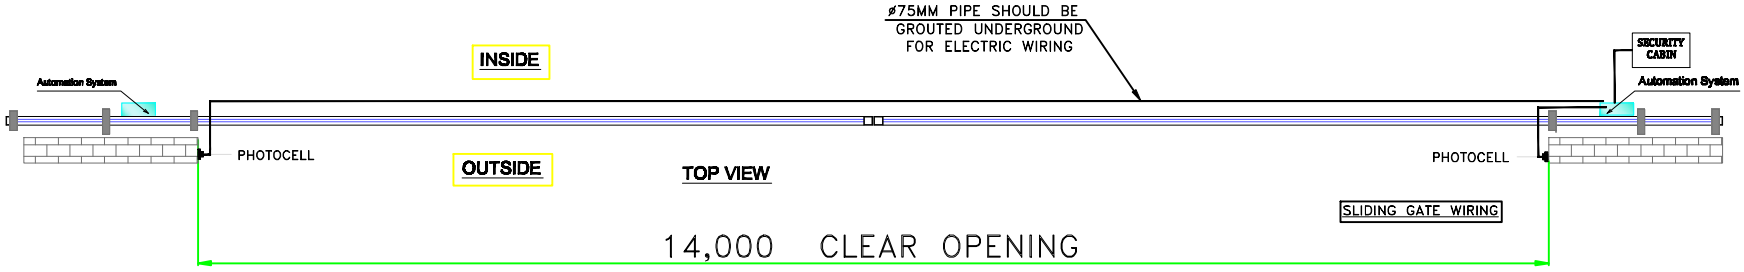

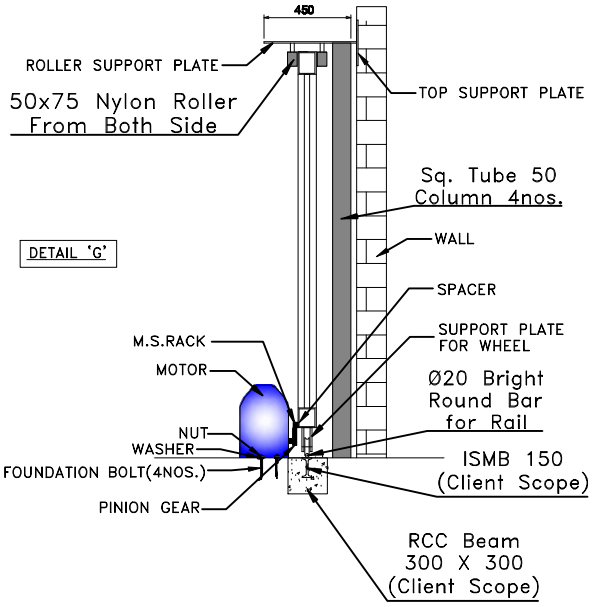

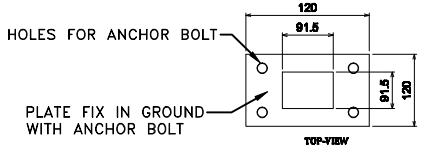

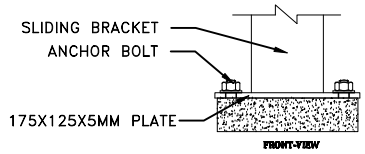

CLEAR OPENING GATE SIZE	14,000 (W) X 1800 (H)
TOTAL BI-PARTING SLIDING GATE SIZE	17,000(W) X 1800 (H)
OUTER FRAME	91.5 X 91.5 X 3.5 mm
INNER FRAME	40 X 40 X 2.5 mm
GAP B/W FRAME	150 c/c
C'COLUMN(V) SUPPORT	8 NOS.

This drawing & designing is the property of NIHVA TECHNOLOGIES. Not be sold or copy to any other concern.

TITLE

SLIDING GATE

CLIENT APPROVAL

ALL DIMENSION ARE IN mm

	SIGN	DATE
DRAWN	ABHIJIT	20/03/15
CHECK	ANIL	20/03/15
REV.	01	
APPRD.		
MFG		
Ref. No.		

NIHVA TECHNOLOGIES PVT. LTD.

NIHVA TECHNOLOGY PVT. LTD. PUNE
Tel : 020 66304033
Email:- info@nihva.com
Website:- www.nihva.com

CLIENT - SHAPOORJI

PROJECT -ALSTOM

SITE -SANAND, GUJRAT

DWG. NO. - NIHVA/15-16/022

SCALE: 01 | WT: | SHEET: 02 OF 02

If any queries contact : projects@nihva.com