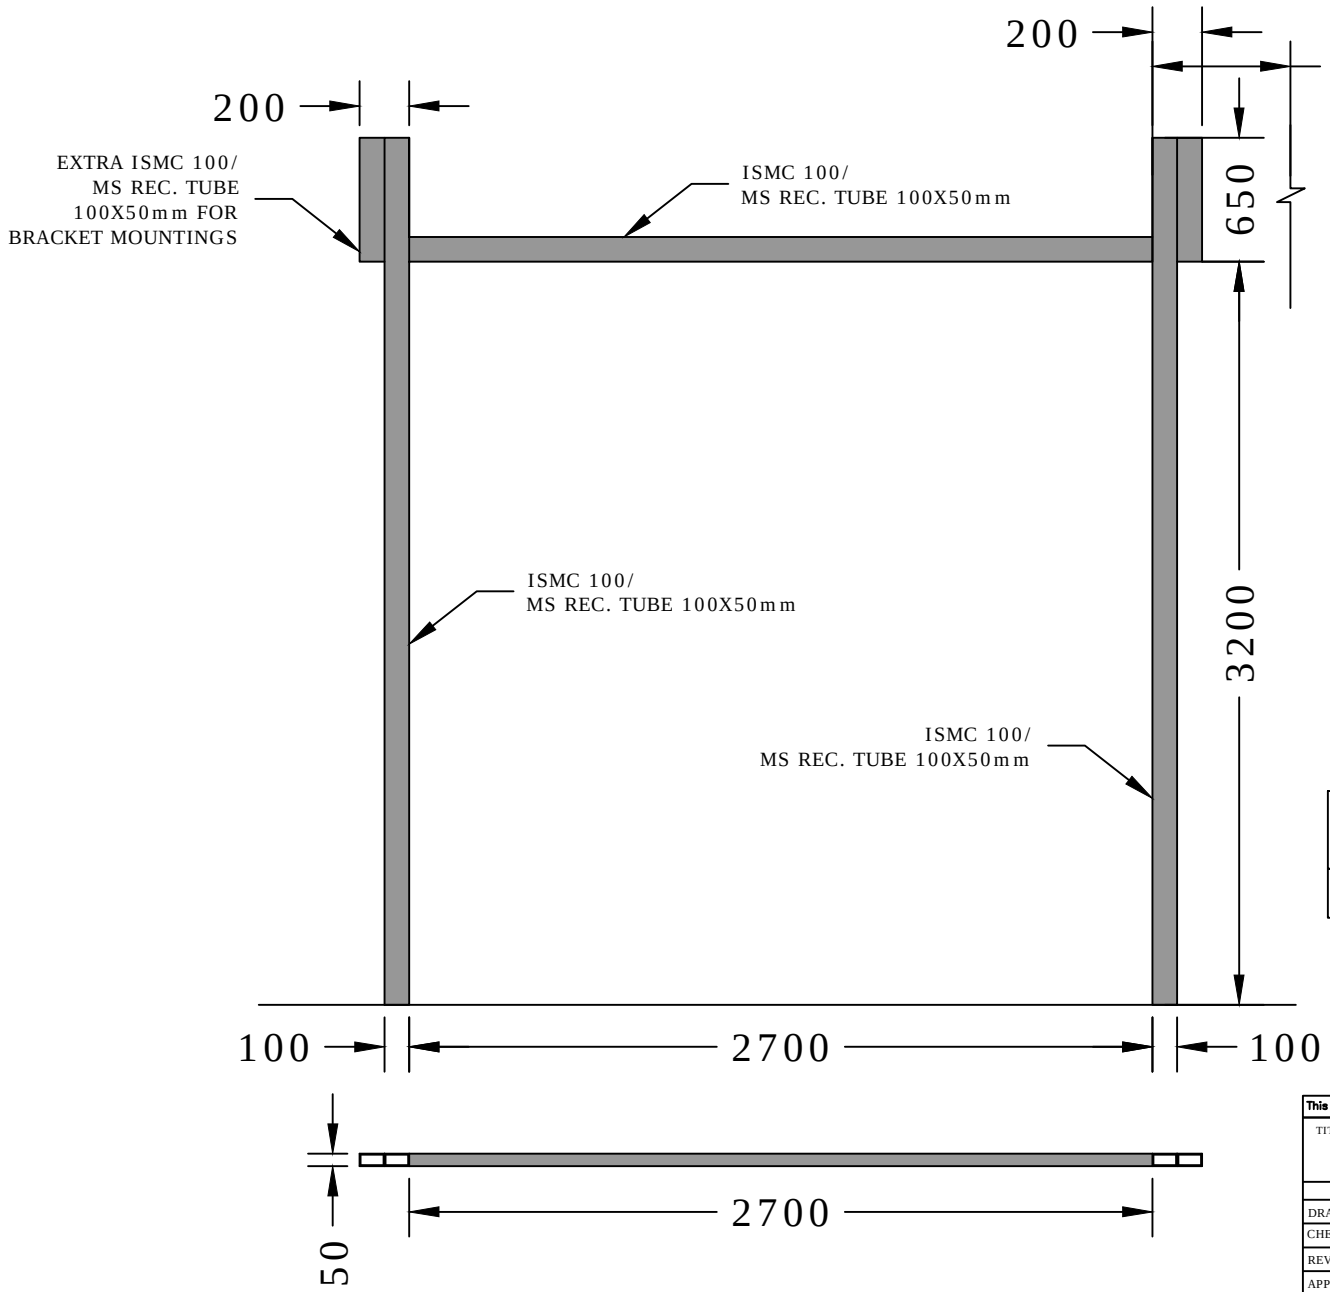

CLEAR WIDTH (CW)	CLEAR HEIGHT (CH)	QUANTITY
2700 mm	3200 mm	2 NOS

This drawing & design is the property of NIHVA TECHNOLOGIES. Not to be sold or copied to any other concern.

TITLE: MS STRUCTURE FOR DOUBLE WALL ROLLING SHUTTER

	SIGN	DATE
DRAWN	SURAJ	15/10/17
CHECK	SHEKHAR	15/10/17
REV.		
APPROVAL	SHEKHAR	15/10/17

If any queries contact : projects@nihva.com

ALL DIMENSION ARE IN mm

NIHVA TECHNOLOGIES PVT. LTD.
NIHVA TECHNOLOGIES PVT. LTD. PUNE
Tel : 020 66304033
Email:- info@nihva.com
Website:- www.nihva.com

CLIENT -FERRERO INDIA PVT. LTD

PROJECT -

SITE -BARAMATI.

DWG. NO. : NIHVA/17-18/0245

SCALE: NTS | WT: | SHEET: 01 OF 01