

DRAWING

REV DESCRIPTION	DATE	REV NO
	28-08-2025	REV 00
1.		

ITEM NO.	PART NUMBER	DESCRIPTION	QTY.
1	HWM UNIT WALKWAY-2_W 1122 X L 13096 MM LONG	MS SQ TUBE 30X30X2.6 MM THK	1
2	CHEQUERED_MS PLATE_W1122 X L13096 X 3 MM THK-13096 MM LONG	MS CHEQUERED PLATE W1122XL13096X3 MM THK	1

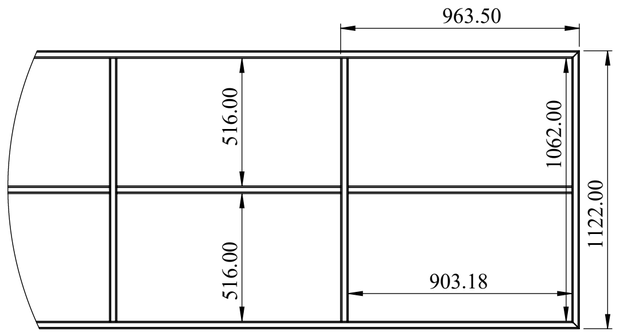

DETAIL B
SCALE 2 : 35

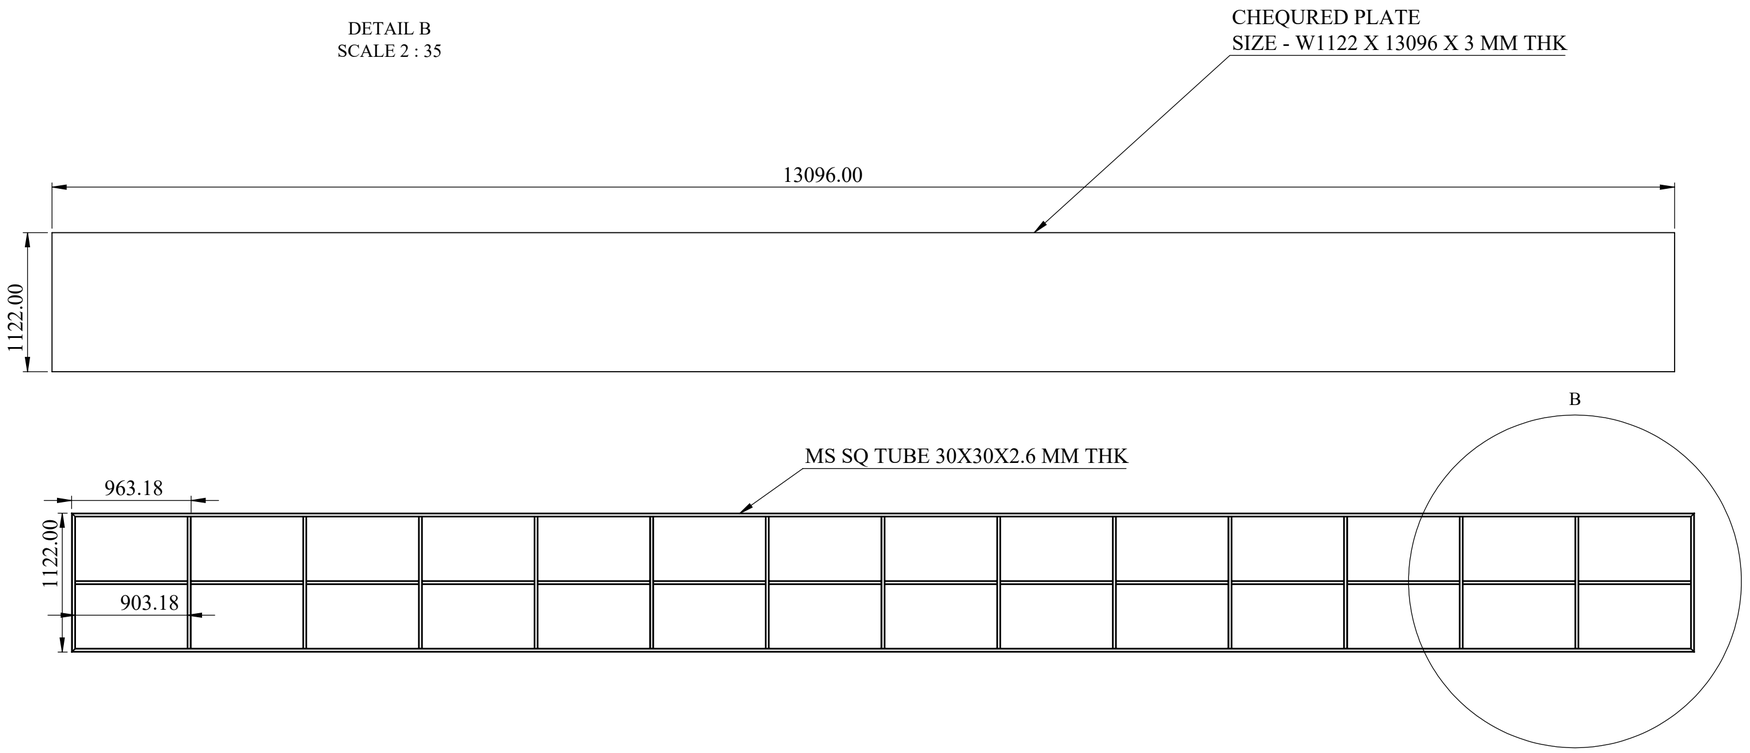

NOTE :

NAME: WALKWAY'S
SIZE : 1122 x13096 MM LONG
MTL : MS
QTY : 01 NOS

SPECIAL INSTRUCTION'S :

TITLE - ROOF AUTOMATION

DWG NO - NTPL-244-PM-001-00-00-00

NIHVA Technologies Pvt. Ltd.

NIHVA TECHNOLOGIES PVT.LTD.PUNE
Website - www.nihva.com

	NAME	SIGNATURE	DATE
DRAWN	V.W.		28-08-2025
CHK'D	S.P.		04-09-2025
APPV'D	V.T.		05-09-2025

PRODUCT - RETRACTABLE ROOF
PROJECT NO - NTPL-244-PM
REVISION - 00
SITE LOCATION - GUJARAT
WEIGHT -
MATRIAL -
QTY - 1
PROJECTION METHOD:
SCALE :
SHEET 3 OF 4

If any queries contact - Design@nihva.com
ALL DIMENSION ARE IN mm
A2