




SIDE VIEW

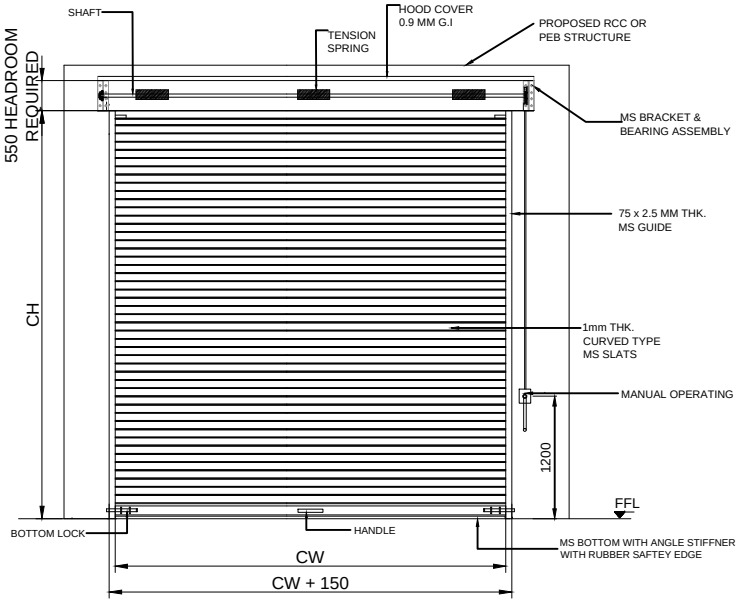


INSIDE ELEVATION

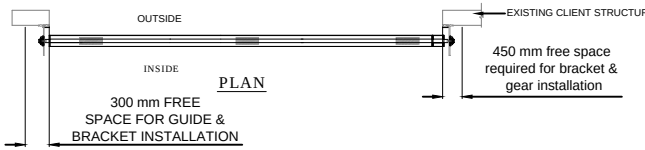


PLAN

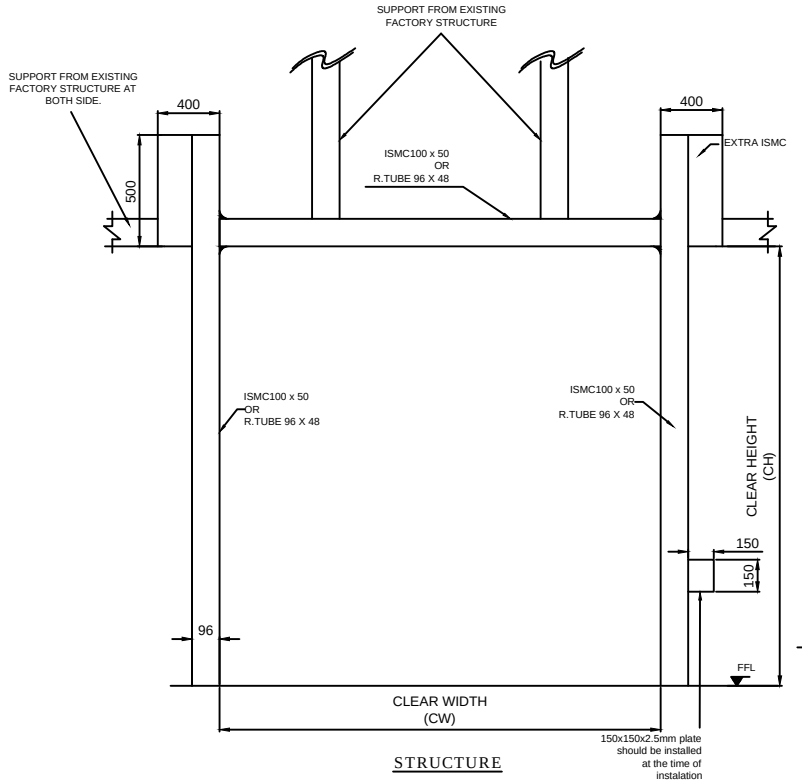

STRUCTURE

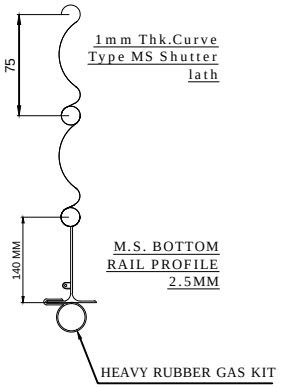

M.S. BOTTOM RAIL PROFILE 2.5MM

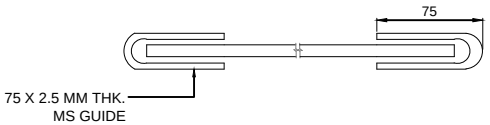

TOLERANCE - ±10mm

RAL 9007	GREY ALUMINIUM	APPROVED
RAL CODE	RAL COLOR	APPROVED

This drawing & design is the property of NIHVA TECHNOLOGIES. Not to be sold or copied to any other concern.

SR NO	(CW) CLEAR WIDTH	(CH) CLEAR HEIGHT	QUANTITY
1	2000	3600	01 NO

NOTE-
1. ALL CIVIL WORK WILL BE CLIENT'S SCOPE.
2.IF TECHNICAL STRUCTURE REQUIRED FOR SHUTTER IS IN CLIENT'S SCOPE.

	NAME	SIGN	DATE
DRAWN	P.A		03.09.2020
CHECK	G.J		03.09.2020
APPRD.			

TITLE
GEAR OPERATED ROLLING SHUTTER

NIHVA TECHNOLOGIES PVT. LTD.
NIHVA TECHNOLOGIES PVT. LTD. PUNE
Tel : 020 66304033
Email:- info@nihva.com
Website:- www.nihva.com

CLIENT - RMK INFRASTRUCTURE

PROJECT -

SITE LOCATION - TALEGAON,PUNE.

If any queries contact : design@nihva.com

DWG. NO. : NIHVA/ 20-21/0048 REV- R00

ALL DIMENSION ARE IN mm

SCALE: NTS WT: SHEET: 01 OF 01