

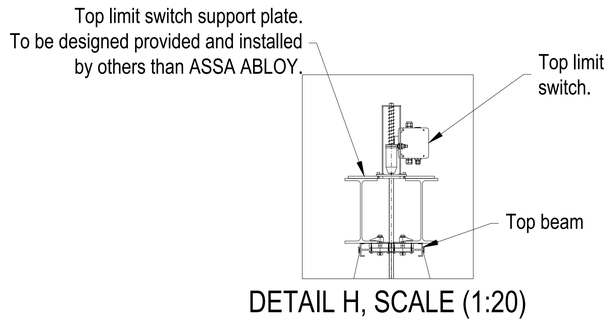



DETAIL H, SCALE (1:20)

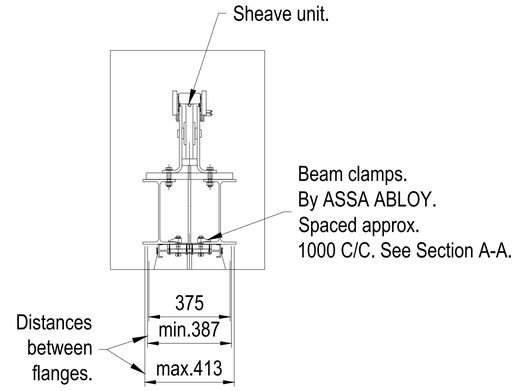


DETAIL J, SCALE (1:20)

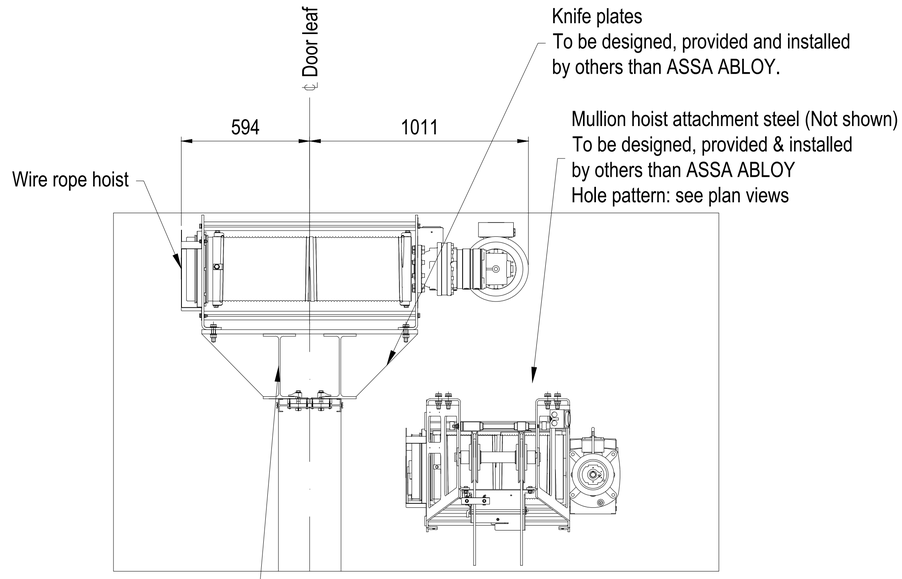


DETAIL G, SCALE (1:20)

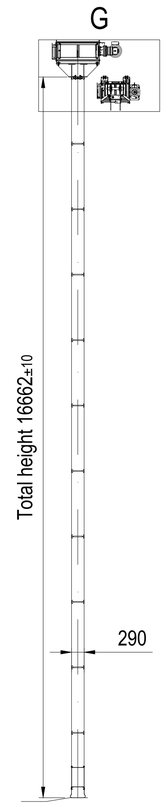

SECTION D-D

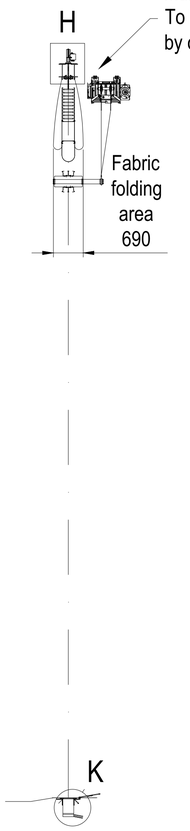


SECTION E-E

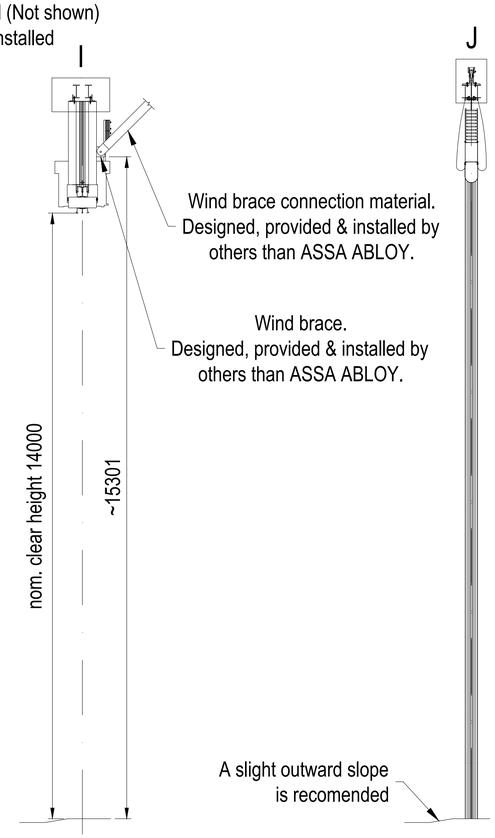


SECTION F-F

SECTION G-G

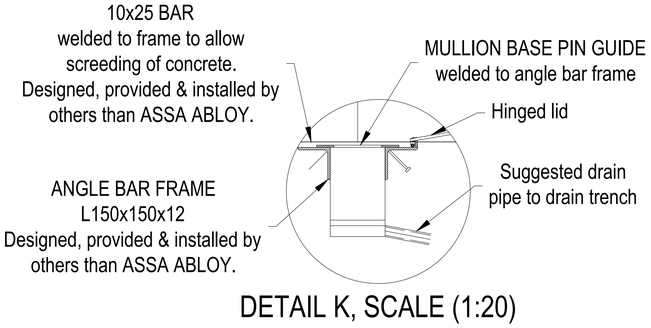

DETAIL K, SCALE (1:20)

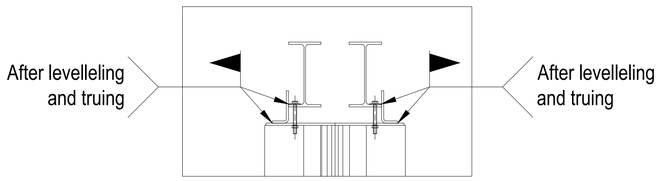

DETAIL I, SCALE (1:20)

DOOR IDENTITY NUMBER: 84801001

LOAD DIAGRAM & NOTES, ref. to drwng. no. 77450

INTERFACE, PLAN VIEWS ref. to drwng. no. 77448

INTERFACE, ELEVATION ref. to drwng. no. 77447

DESIGNED EB		SIZE A2	SCALE 1:100
CODE 84801	If not otherwise stated: Tolerances ISO 2768-m EN ISO 13920-B	GMR Aero Technic Hangar2	
ITEM NO	Cutting class ISO 9013-442	India	
DATE 2022-08-31	Weld class ISO 5817-C	Megadoor 99000x14700/14000	PLOT DATE
ASSA ABLOY	Surface finish Smooth raw surface	Interface, sections	
		DRAWING NO 77449	REVISION --

This document is the property of ASSA ABLOY Entrance Systems AB and shall not without our written permission be copied, imparted to a third party or used for any other unauthorized purpose.