
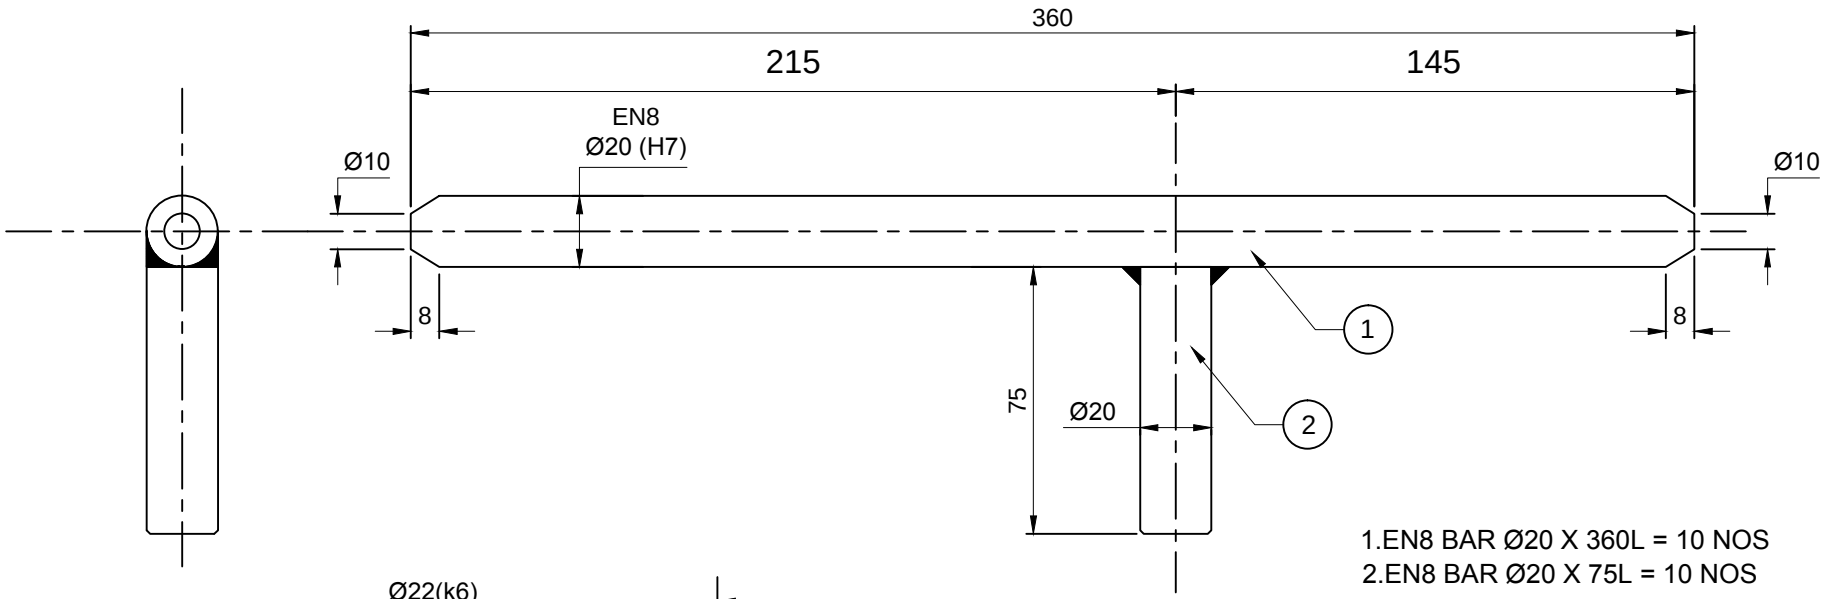


1.EN8 BAR Ø20 X 360L = 10 NOS
2.EN8 BAR Ø20 X 75L = 10 NOS

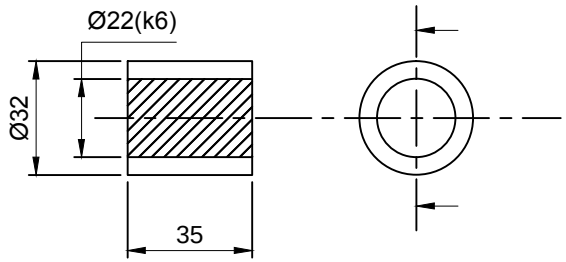

3. M.S BUSH
OD32 X ID22 X 35L = 30 NOS

This drawing & design is the property of NIHVA TECHNOLOGIES. Not to be sold or copied to any other concern.

TITLE: TOWER BOLT			NIHVA TECHNOLOGIES PVT. LTD. PUNE Tel : 020 66304033 Email:- info@nihva.com Website:- www.nihva.com
	NAME	SIGN	DATE
DRAWN	P.A		30.12.2020
CHECK	G.J		30.12.2020
APPRD.			
CLIENT -			
PROJECT -			
SITE LOCATION -			
If any queries contact : design@nihva.com	DWG. NO. : NIHVA/19-20/VDR/285		REV- R00
ALL DIMENSION ARE IN mm	SCALE: NTS	WT:	SHEET: 01 OF 01