


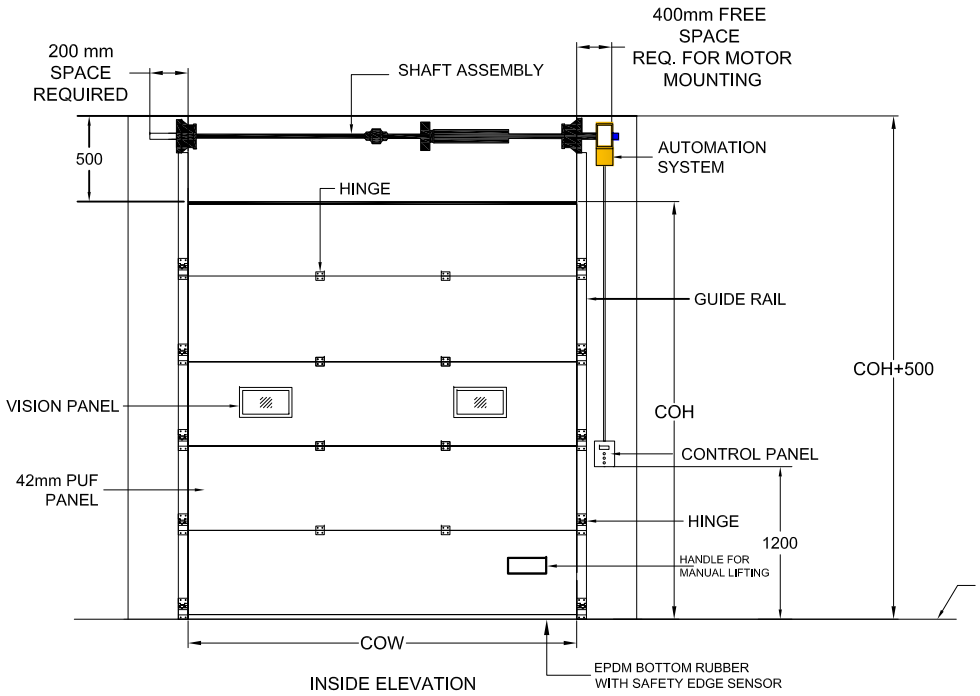


INSIDE ELEVATION

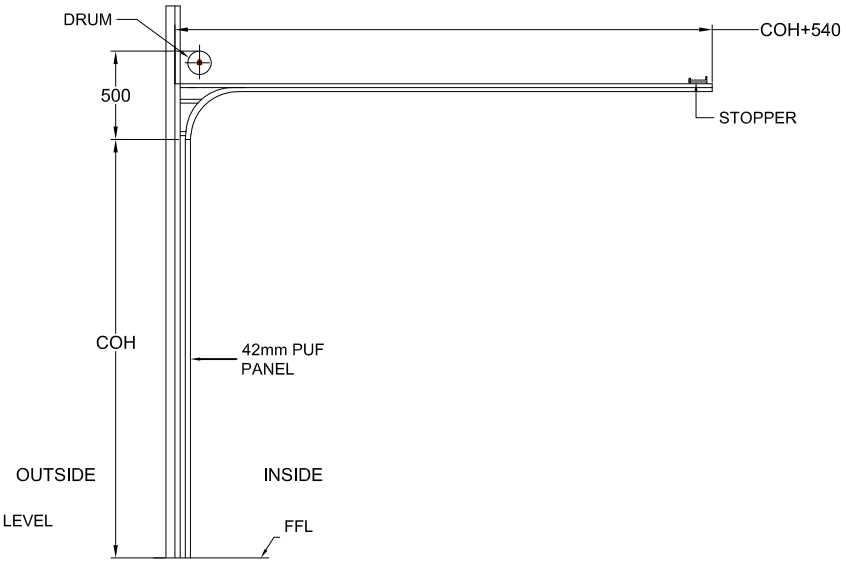

SIDE VIEW

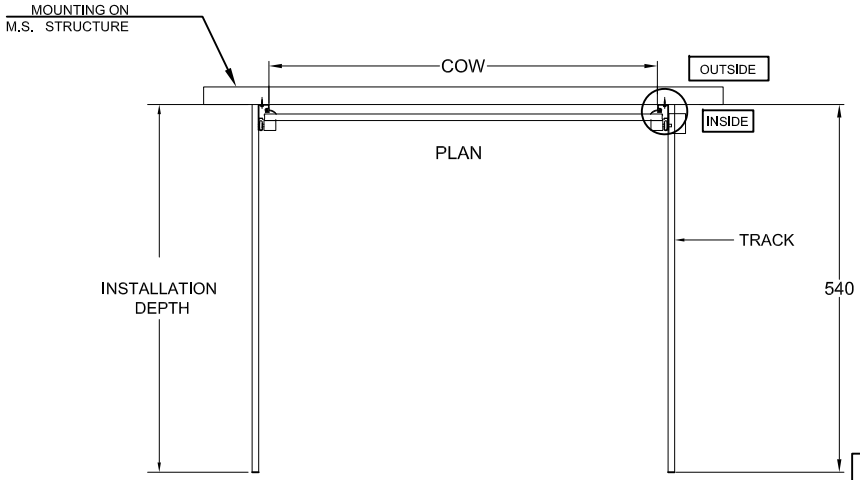

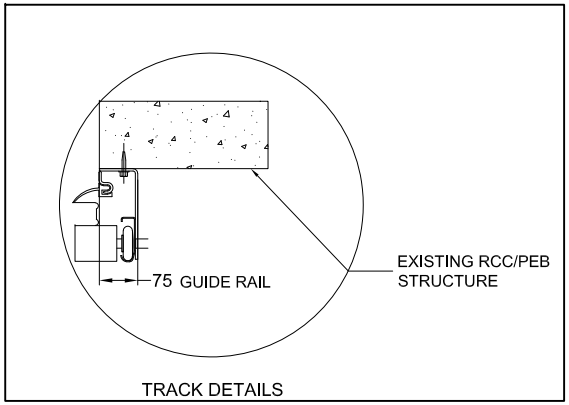

TRACK DETAILS

SR NO	CLEAR OPENING WIDTH(COW)	CLEAR OPENING HEIGHT(COH	QTY	MOUNTING	MOTOR SIDE
2	2500	3070	1	INSIDE	RH
1	2480	2980	1	INSIDE	RH

PANEL RAL CODE- RAL 9002 GREY WHITE

KINDLY NOTE THAT REQUIRED M.S. STRUCTURE , FITTING & ALL CIVIL WORK IS IN CLIENT SCOPE.

TOLERANCE:±10mm

This drawing & design is the property of NIHVA TECHNOLOGIES. Not to be sold or copied to any other concern.

TITLE	SECTIONAL DOOR HL STANDARD			NIHVA TECHNOLOGIES PVT. LTD. PUNE Tel : 020 66304033 Email:- info@nihva.com Website:- www.nihva.com
	NAME	SIGN	DATE	
DRAWN	S.M.S.		15.1.2021	CLIENT -SCON PROJECTS PVT LTD
CHECK	S.M.		15.1.2021	PROJECT -INNOVATECH INDIA PVT LTD
APPROVAL				SITE LOCATION - SANAND
If any queries contact : design@nihva.com				DWG. NO. : NIHVA/20-21/0137 REV: 0
ALL DIMENSION ARE IN mm				SCALE: NTS WT: SHEET: 01 OF 02