
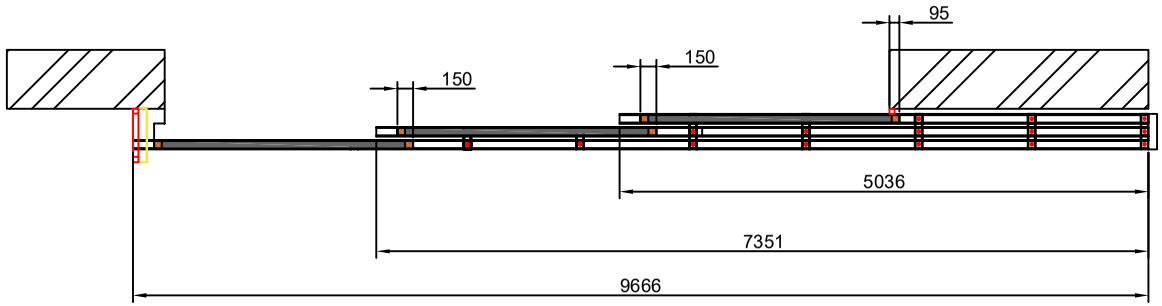


Client scope
*Front Gutter need to be shift. * roof need to be shifted by 300 mm approx. *Civil foundation need to be done for tracks

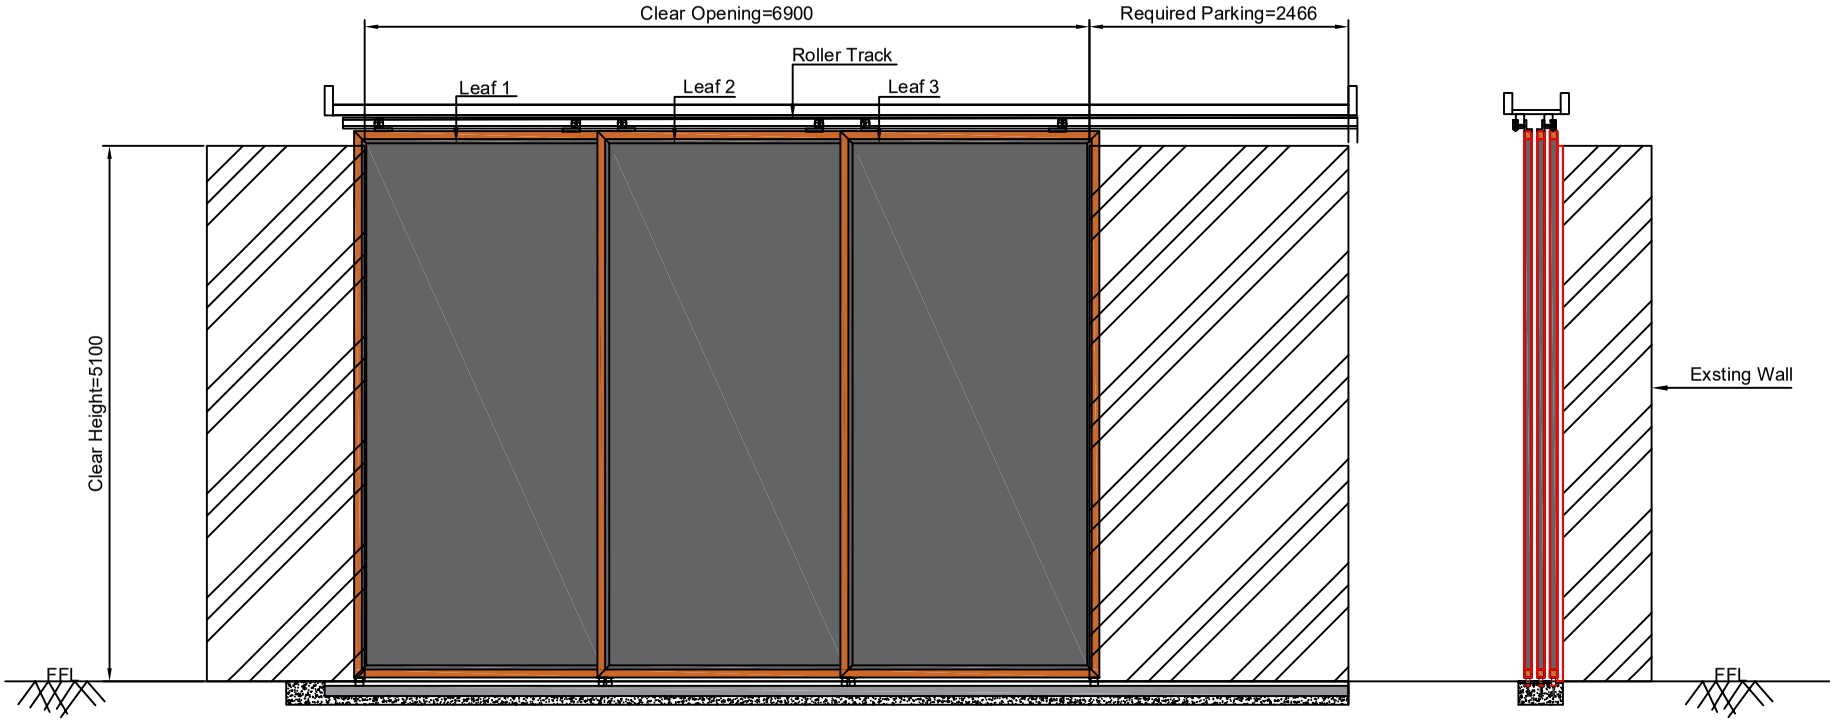

Note:--

1.All dimension are in MM

2.All Civil work will be in client scope

3.Required Parking space will be 2465

This drawing & design is the property of NIHVA TECHNOLOGIES. Not to be sold or copied to any other concern.

TITLE:- 4 LEAF RIGHT SIDE CRM DOOR 11

NIHVA TECHNOLOGIES PVT. LTD.

NIHVA TECHNOLOGIES PVT. LTD. PUNE
Tel : 020 66304033
Email:- info@nihva.com
Website:- www.nihva.com

	NAME	DATE	SIGN
DRAWN	SUJATA	20/04/2022	
CHECK	M.SUTAR	20/04/2022	
APPRD.	V.TARAK	20/04/2022	

CLIENT - LESTECH

LOCATION - POSCO MANGAON

PRODUCT - SLIDING DOOR

If any queries contact : design@nihva.com

DWG NO:-NIHVA/22-23/CLT/0016 REV- 0

ALL DIMENSION ARE IN mm

SCALE: NTS SCALE:-- 1:1 SHEET: 01 OF 01

Rev No.	Revision	Date	Revised By