
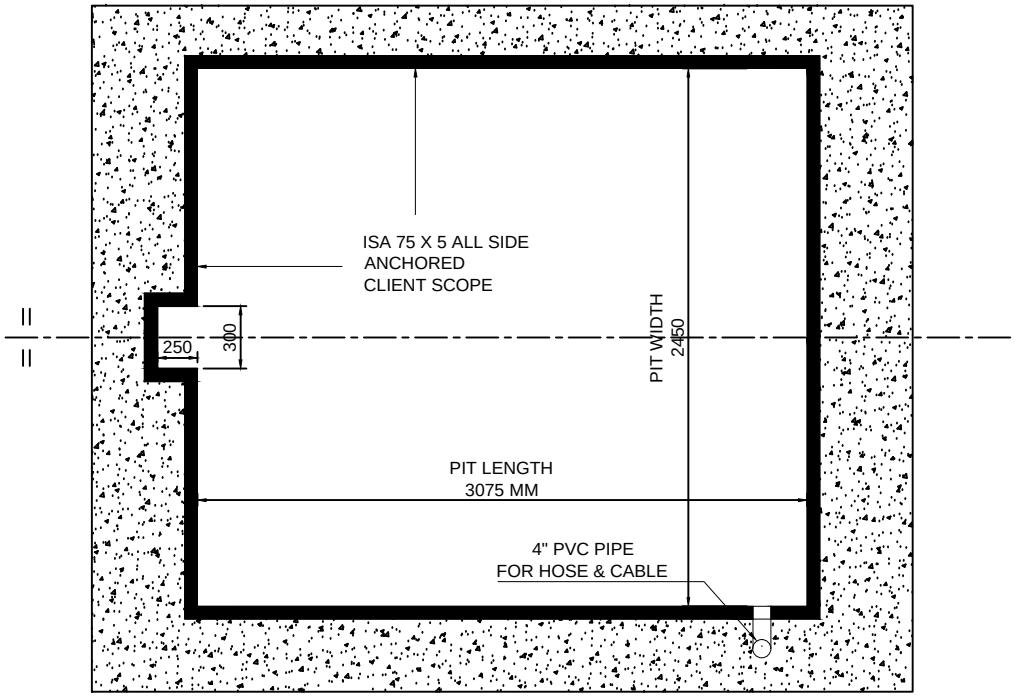


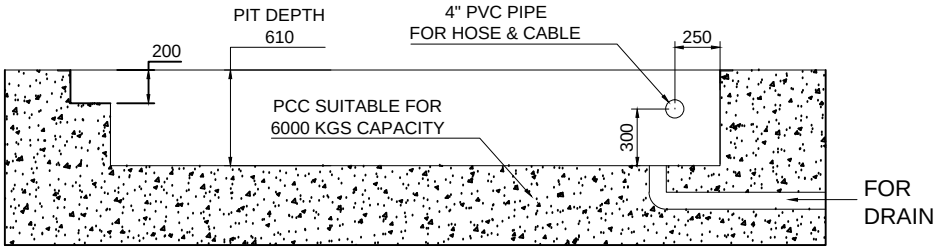

PIT DRAWING

NOTE :

1. HYDRAULIC HOSE LENGTH : 12 MTR
2. ELECTRICAL CABLE : 12 MTR
3. PIT / CIVIL / PVC PIPE WILL BE IN CLIENT SCOPE.
4. COLOR : a. GOLDEN YELLOW.
   b. ULTRA MARINE BLUE.
5. INPUT SUPPLY : 3 PHASE 400 VOLT WITH NEUTRAL.

This drawing & design is the property of NIHVA TECHNOLOGIES. Not to be sold or copied to any other concern.

TITLE	ELECTRO HYDRAULIC SCISSOR LIFT PIT DRG			NIHVA TECHNOLOGIES PVT. LTD.
	NAME	SIGN	DATE	
DRAWN	P.V.A		15.11.2019	CLIENT - IKEA
CHECK	V.M.T		15.11.2019	PROJECT -
APPRD.				SITE LOCATION -
If any queries contact : design@nihva.com				DWG. NO. : NIHVA/19-20/0153 REV- 0
ALL DIMENSION ARE IN mm				SCALE: NTS WT: SHEET: 01 OF 01

NIHVA TECHNOLOGIES PVT. LTD. PUNE
Tel : 020 66304033
Email:- info@nihva.com
Website:- www.nihva.com