

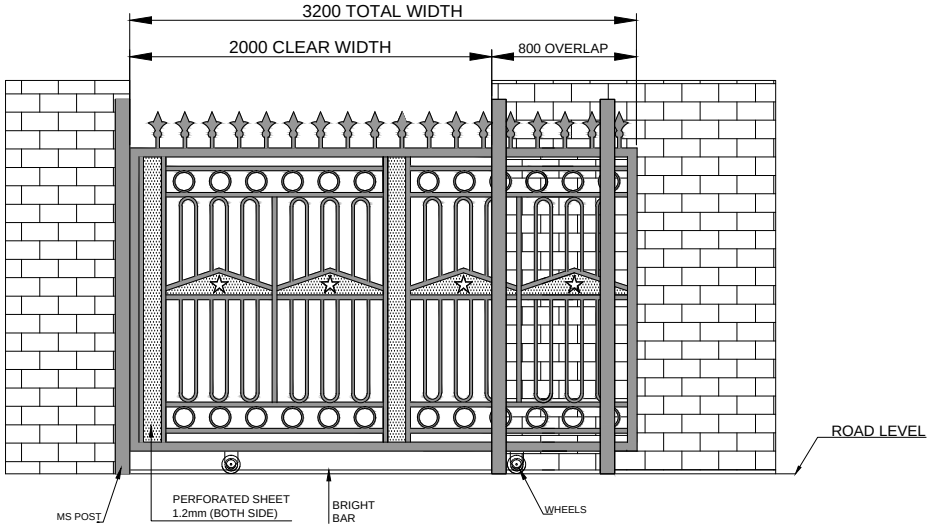



ELEVATION

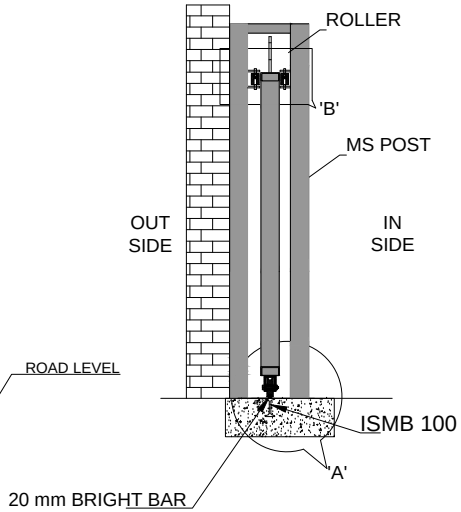

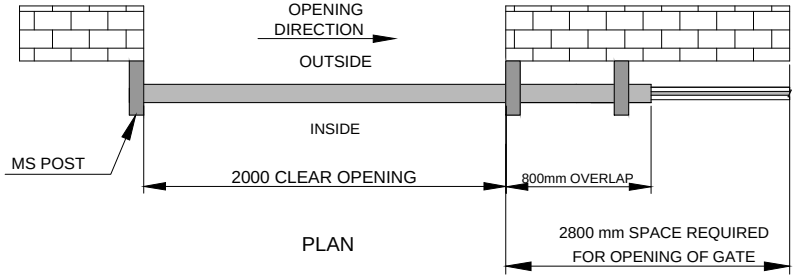


PLAN

RACK AND
PINION MECHANISM

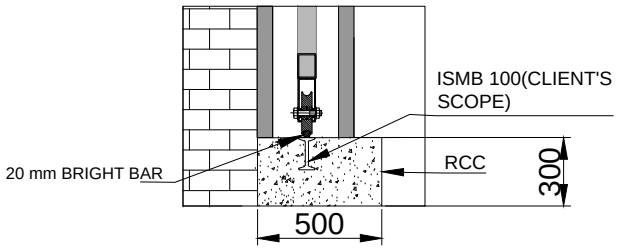

DETAIL VIEW OF A

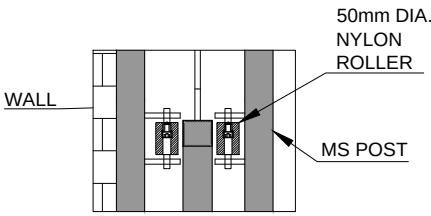

DETAIL VIEW OF B

TOTAL NO OF POST ARE 6.
TOLERANCE- ±10mm

CLEAR WIDTH	CLEAR HEIGHT	QTY.
2000mm	2000mm	03 NOS

SR NO	GATE SPECIFICATION	MATERIAL	
1	100X50X3.2mm	MS	OUTER FRAME
2	50X25X2mm	MS	INNER DESIGN
3	25X25X2mm	MS	INNER DESIGN
4	15mm Dia. round pipe	MS	INNER DESIGN
5	1.2mm THK. perforated sheet	MS	INNER DESIGN
6	special spikes at top	MS	INNER DESIGN

DIMENSION :

CLEAR WIDTH	CLEAR HEIGHT	QUANTITY
2000mm	2000mm	03 NOS

MATERIAL:

THICKNESS :

NOTE-
1. ALL REQUIRED CIVIL WORK WILL BE IN CLIENTS SCOPE.
2. ONE COAT OF RED OXIDE & TWO COAT OF APPROVED RAL SHADE WILL BE GIVEN TO THE GATE.
3.GATE LEAF WILL BE IN TWO PARTS FOR TRANSPORTATION & WILL BE WELD TOGETHER ON SITE.

NIHVA TECHNOLOGIES PVT. LTD.
NIHVA TECHNOLOGIES
PVT. LTD. PUNE
Email:- info@nihva.com
Website:- www.nihva.com

TITLE:

MANUAL SLIDING GATE
2X2m

CLIENT'S APPROVAL :

CLIENT - L&T CONSTRUCTION

PROJECT -

SITE LOCATION -KARNATAKA

DWG. NO. : NIHVA/17-18/0290 | REV- 0

SCALE: NTS | WT: | SHEET:1 OF 1

		DATE	SIGN.
DRAWN	SURAJ.	21-11-2017	
CHECK	OMKAR.	21-11-2017	
APPRD	SHEKHAR.	21-11-2017	

If any queries contact : design@nihva.com

NOTE: ALL DIMENSIONS ARE IN mm

THIS DRAWING & DESIGN IS THE PROPERTY OF NIHVA TECHNOLOGIES. NOT TO BE SOLD OR COPIED TO ANY OTHER CONCERN.