


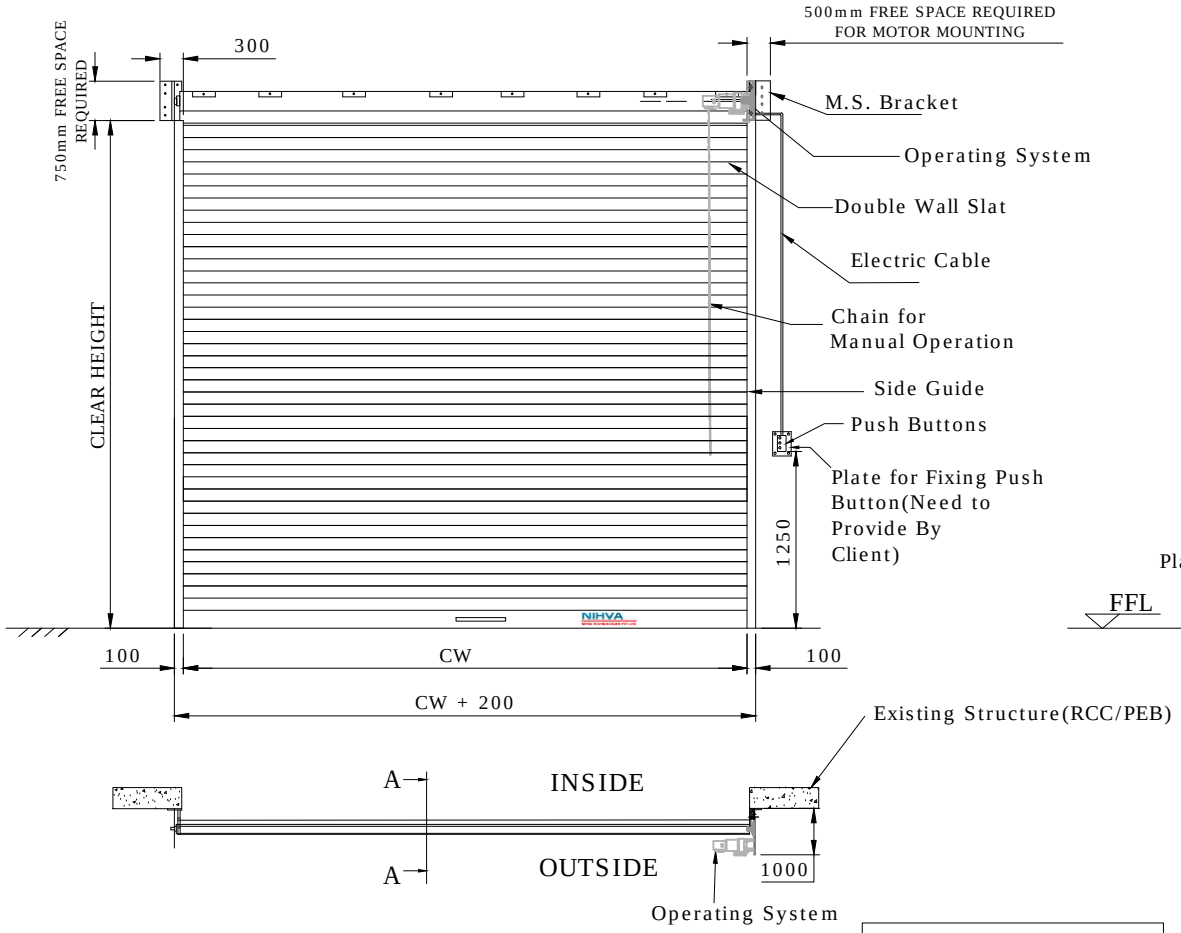


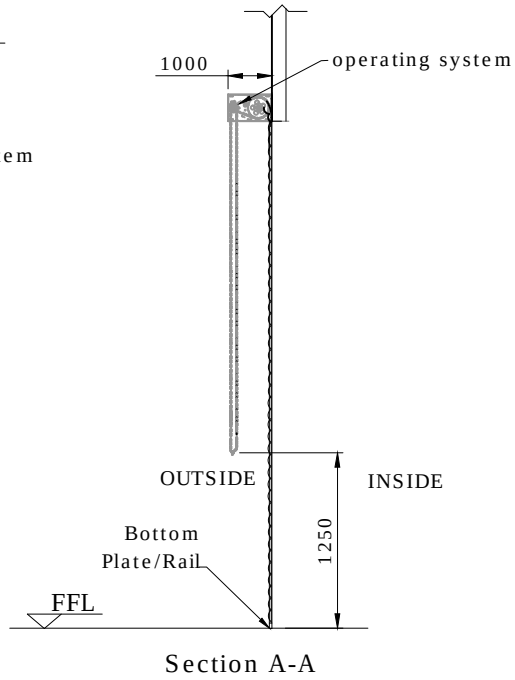

Section A-A

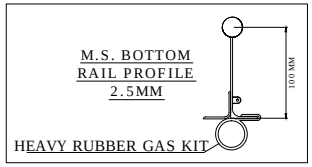

Main Slats
Double Wall Rolling Shutter

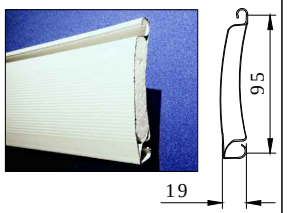

CLEAR WIDTH (CW)	CLEAR HEIGHT (CH)	QUANTITY
3000mm	4500mm	4 NOS
2850mm	4500mm	4 NOS

NOTE: COLOUR OF THE SHUTTER WILL BE OFF WHITE

DIMENSION :

CLEAR WIDTH	CLEAR HEIGHT	QUANTITY
3000mm	4500mm	4NOS
2850mm	4500mm	4NOS

MATERIAL :

THICKNESS :

NOTE-
01.REQUIERD STRUCTURE FOR ROLLING SHUTTER WILL BE IN CLIENT'S SCOPE.
02.IF WALL FOR GUIDE AND RCC LINTEL FOR MS BRACKET IS PRESENT AT SITE THEN THIS MS STRUCTURE WILL NOT BE REQUIRED.
03.SINGLE PHASE SUPPLY IS REQUIRED.

NIHVA TECHNOLOGIES PVT. LTD. PUNE
Email:- info@nihva.com
Website:- www.nihva.com

TITLE:
DOUBLE WALL ROLLING SHUTTER

CLIENT'S APPROVAL :

CLIENT - IPS

PROJECT - LUPIN

SITE LOCATION -NAGPUR.

DWG. NO. : NIHVA/17-18/0030

SCALE: NTS	WT:	SHEET:1 OF 1

DRAWN BY: SURAJ	DATE: 17-05-2017
CHECK BY: SAGAR P.	DATE: 17-05-2017
APPROVED BY : S.S	DATE: 17-05-2017

If any queries contact : projects@nihva.com

NOTE: ALL DIMENSIONS ARE IN mm

THIS DRAWING & DESIGN IS THE PROPERTY OF NIHVA TECHNOLOGIES. NOT TO BE SOLD OR COPIED TO ANY OTHER CONCERN.