
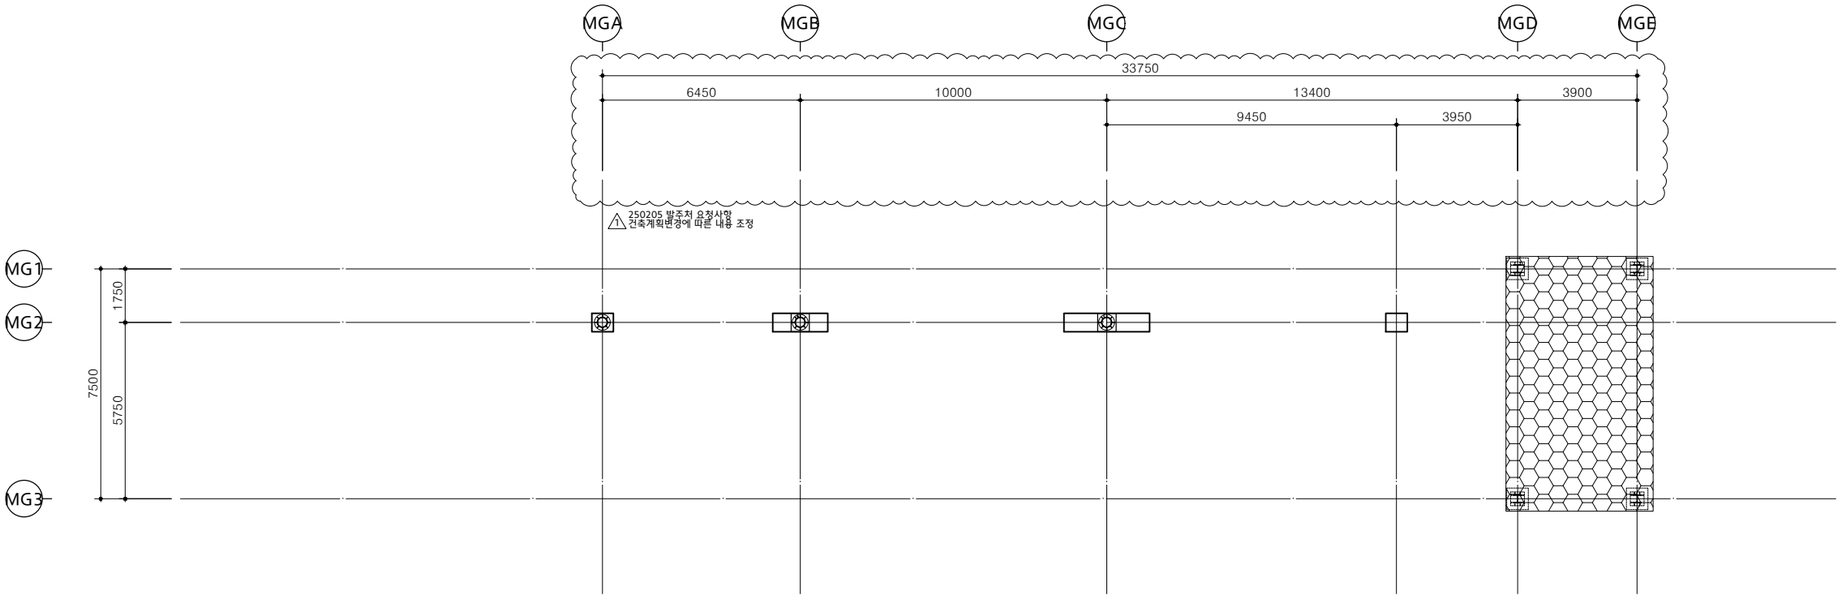


1 GROUND FLOOR LOADING PLAN

SCALE : 1/100

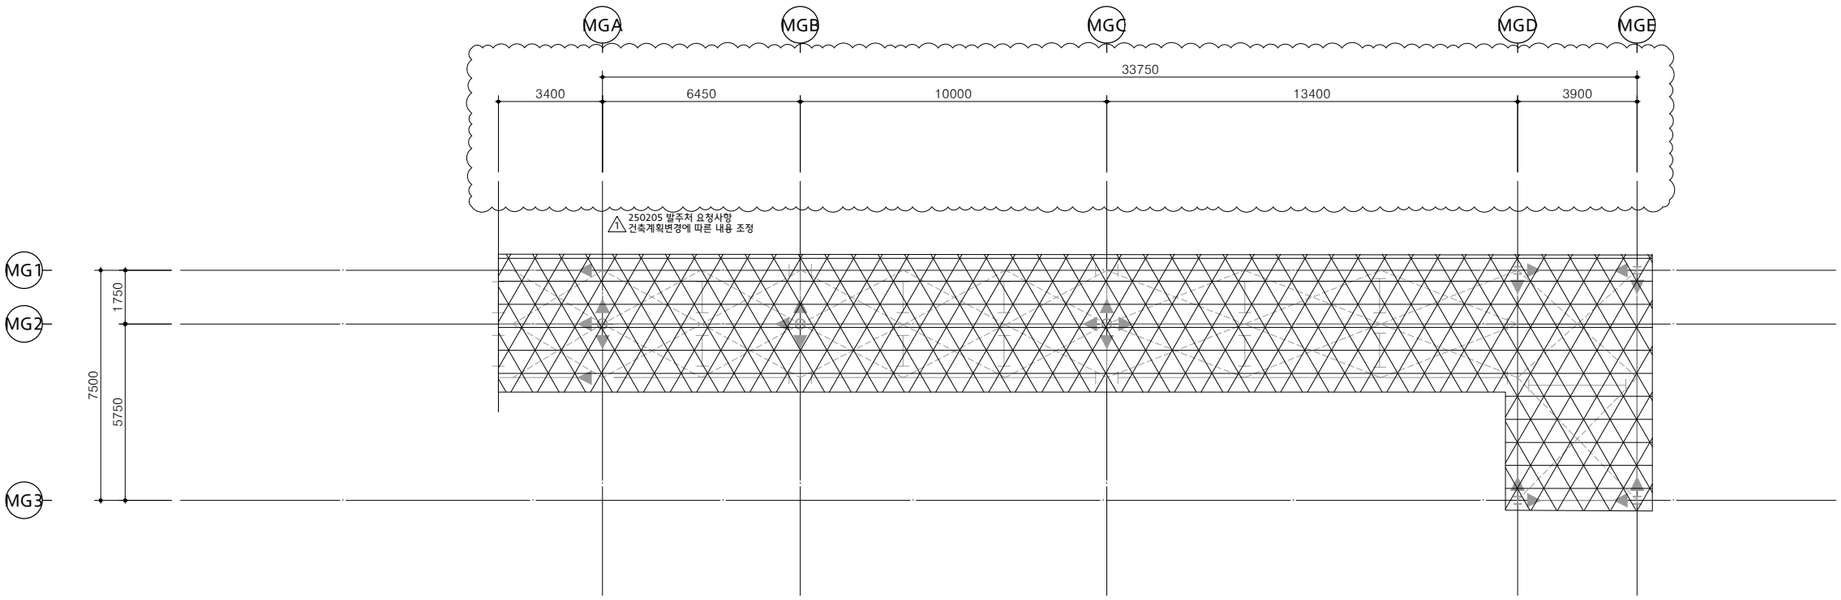

2 ROOF LOADING PLAN

SCALE : 1/100

KEY PLAN

NOTE:

1. THIS DRAWING IS MAINLY FOR THE BASIC INFORMATION AND GUIDANCE FOR THE DESIGN AND ENGINEERING FOR THE PROJECT. DO NOT USE THIS FOR CONSTRUCTION.
2. THE INFORMATIONS ON THIS DRAWING CAN BE CHANGED ACCORDING TO THE CLIENT'S UPDATED DECISION.
3. THIS DRAWING CAN BE ADJUSTED AND REVISED ACCORDING TO THE LOCAL CONDITIONS AND REGULATIONS SUPPLIED BY THE LOCAL ARCHITECTS ENGINEERS AND THE INSURANCE UNDERWRITER.
4. ALL STRUCTURAL, MECHANICAL, ELECTRICAL ITEMS ARE ONLY FOR INFORMATION. FURTHER COORDINATION IS NEEDED.
5. LIVE LOAD LEGEND
   - LIVE LOAD : 5.0 kN/m²
   - LIVE LOAD : 0.75(ROOF) kN/m²

REV.	DESCRIPTION	DRAWN	DATE
1	CD Rev.1	OH,J.S	2025. 02.14
0	CONSTRUCTION DRAWING	OH,J.S	2024. 07.30
Δ	DESIGN DEVELOPMENT	OH,J.S	2024. 06.28

CLIENT

HYUNDAI

ARCHITECTS & ENGINEERS

JUNGLIM ARCHITECTURE

PROJECT TITLE

PUNE HMI PROJECT

DRAWING TITLE

[MAIN GATE]
LOADING PLAN

SCALE	DRAWN	CHECKED	REVIEWED	APPROVED	APPROVED
A1: 1/100 A3: 1/200	OH,J.S	HONG,G.D	LEE,S.L	HEC INDIA	PARK,T.S
DATE					
14 FEB,2025					

MAIN CONTRACTOR

HEC INDIA LLP

DRAWING NO. WA-IPB-640-S-0201

REV. 1

A1 SIZE (841mm x 594mm)