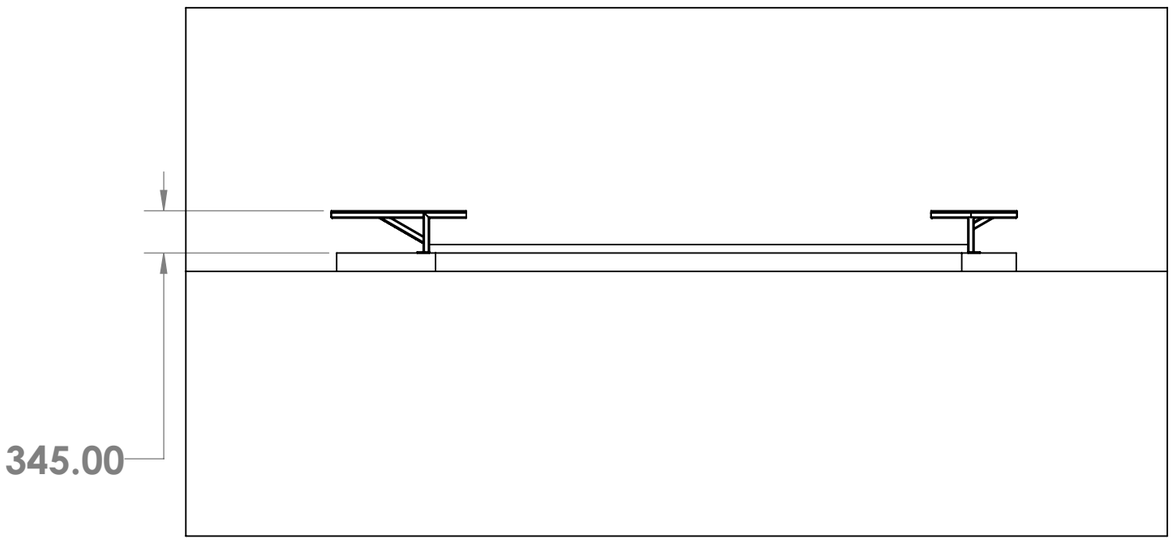
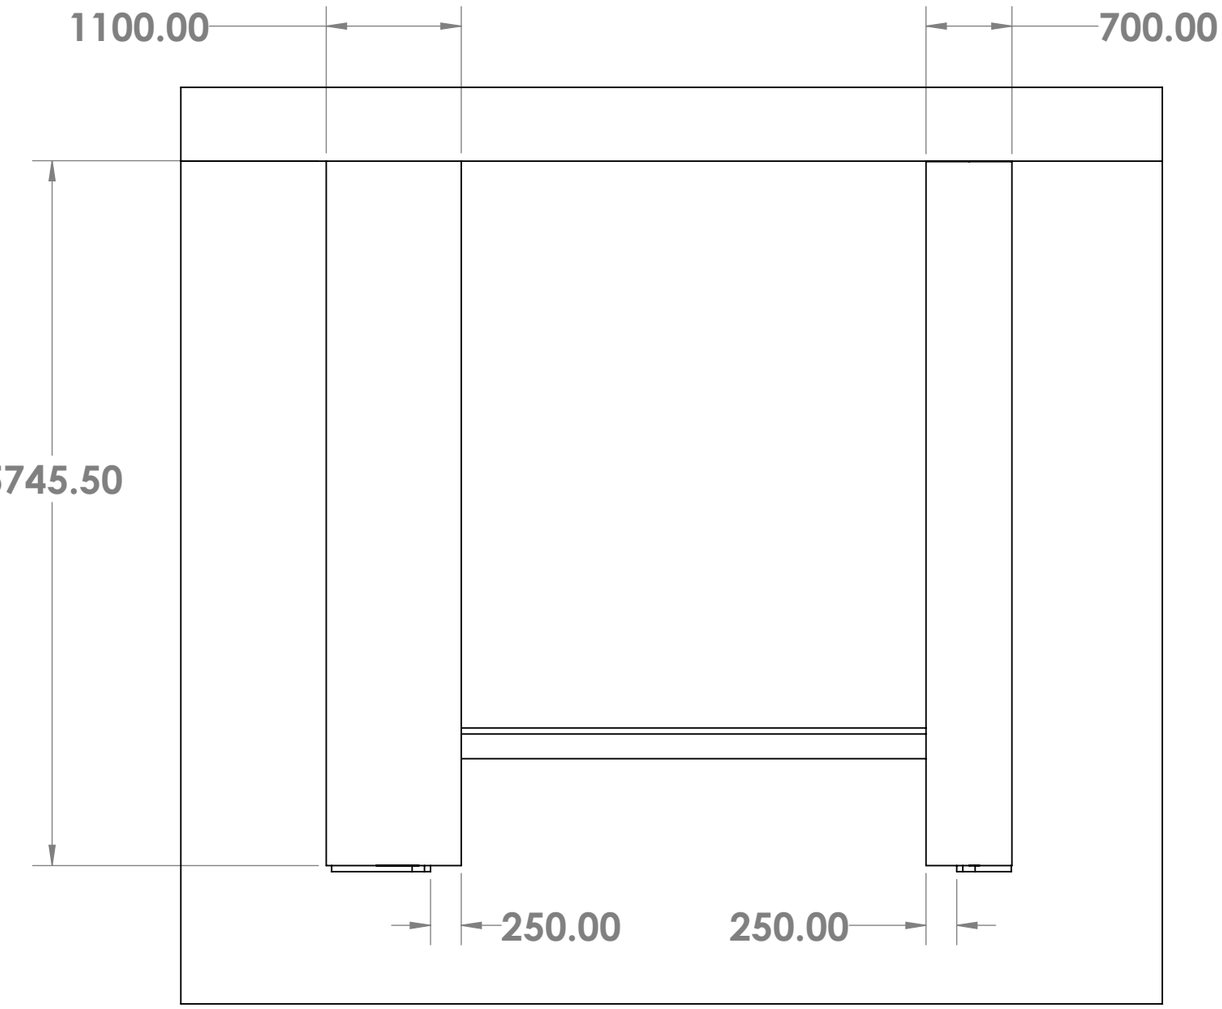
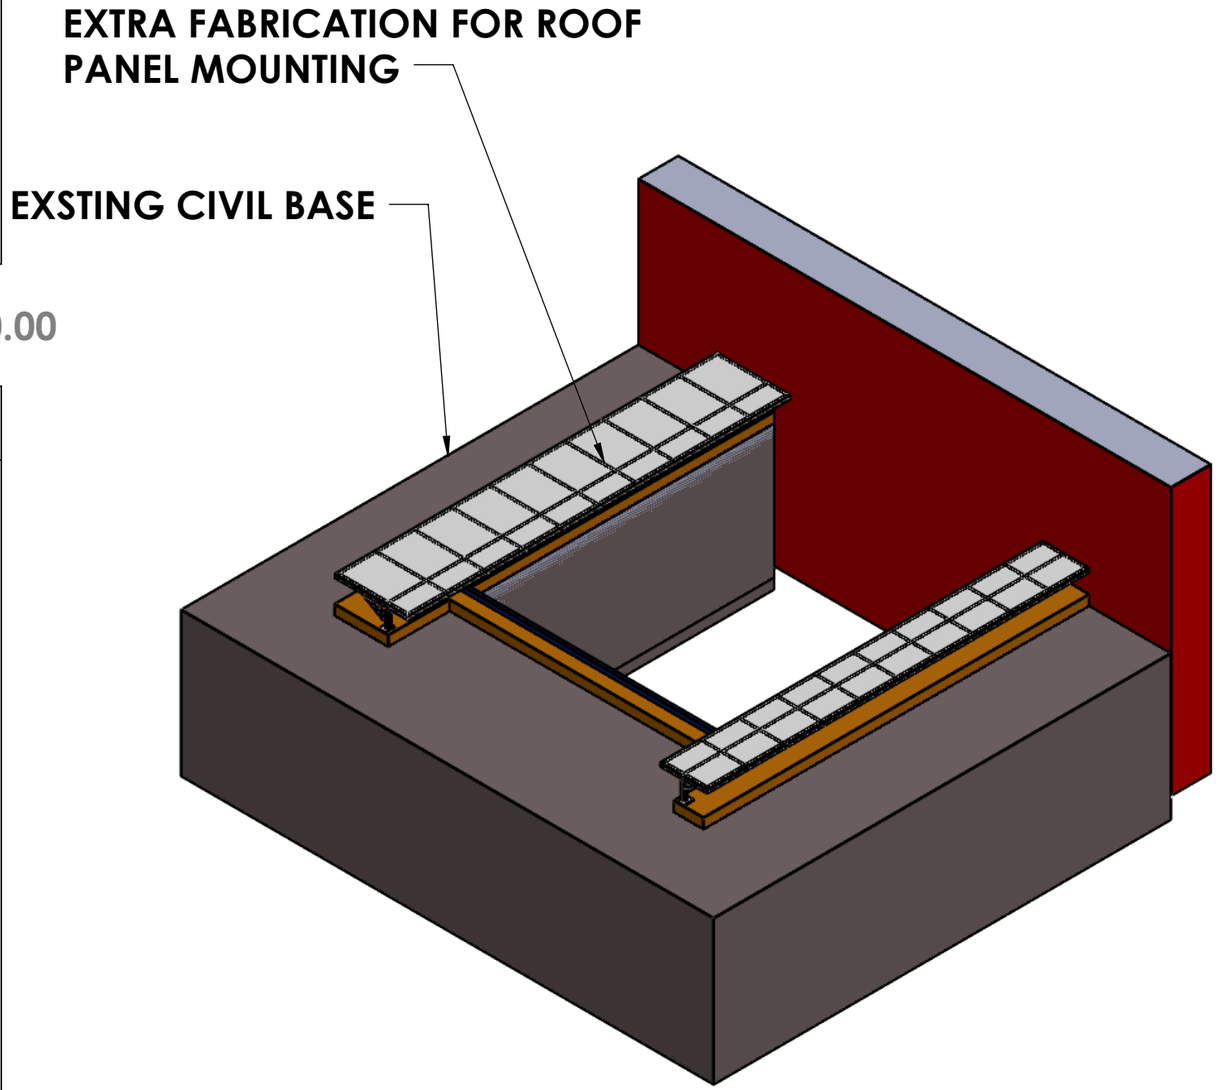
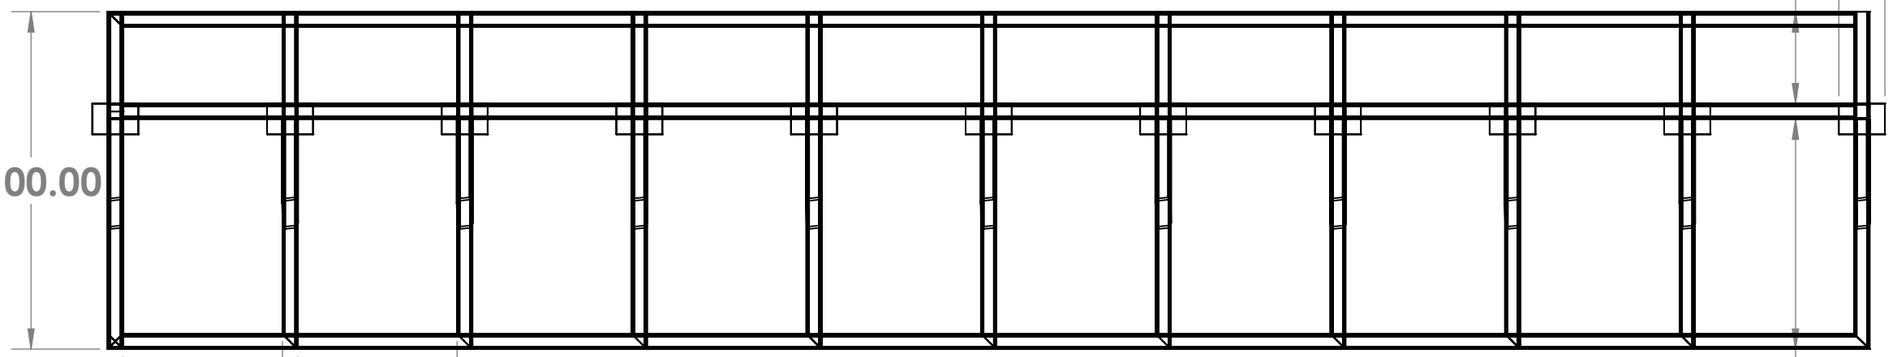
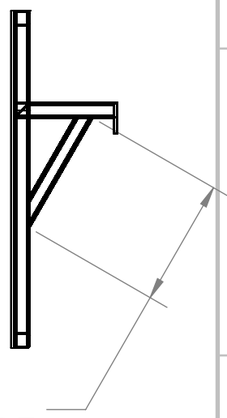



| | | | | |
|---|---|---|---|---|
| TITLE - PROPOSED PLAN LAYOUT | | | | NIHVA TECHNOLOGIES PVT.LTD.PUNE Website - www.nihva.com |
| | NAME | SIGNATURE | DATE | CLIENT - |
| DRAWN | S.W | | 29.08.2024 | PRODUCT - RETRACTABLE ROOF |
| CHK'D | P.M. | | 29.08.2024 | SITE LOCATION - |
| APPV'D | V.T. | | 29.08.2024 | |
| if any queries contact - supportautomation@nihva.com | | | | REVISION - 0 |
| ALL DIMENSION ARE IN mm | | A3 | | SCALE - 1.1 SHEET 1 OF 3 |

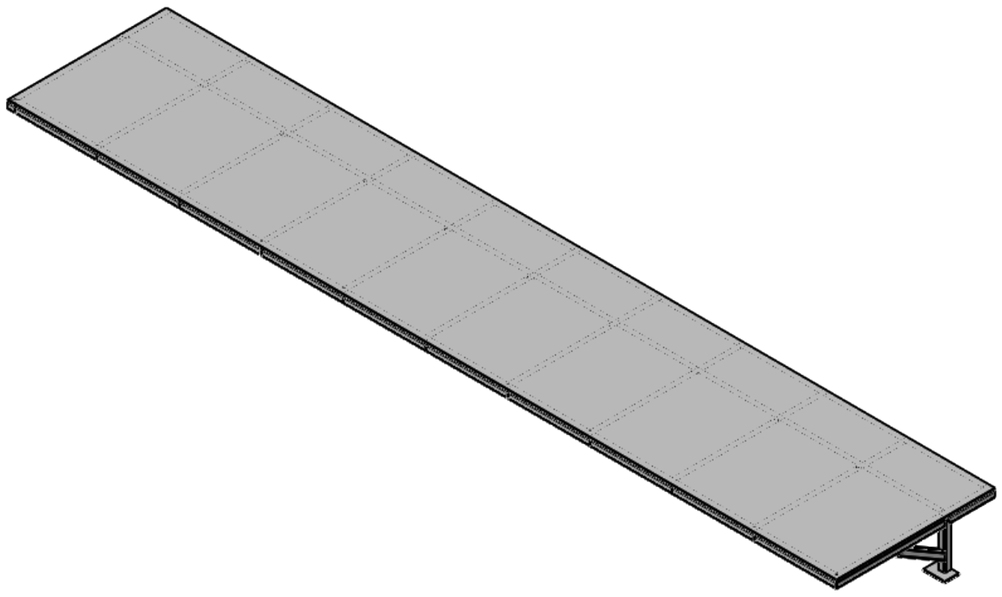


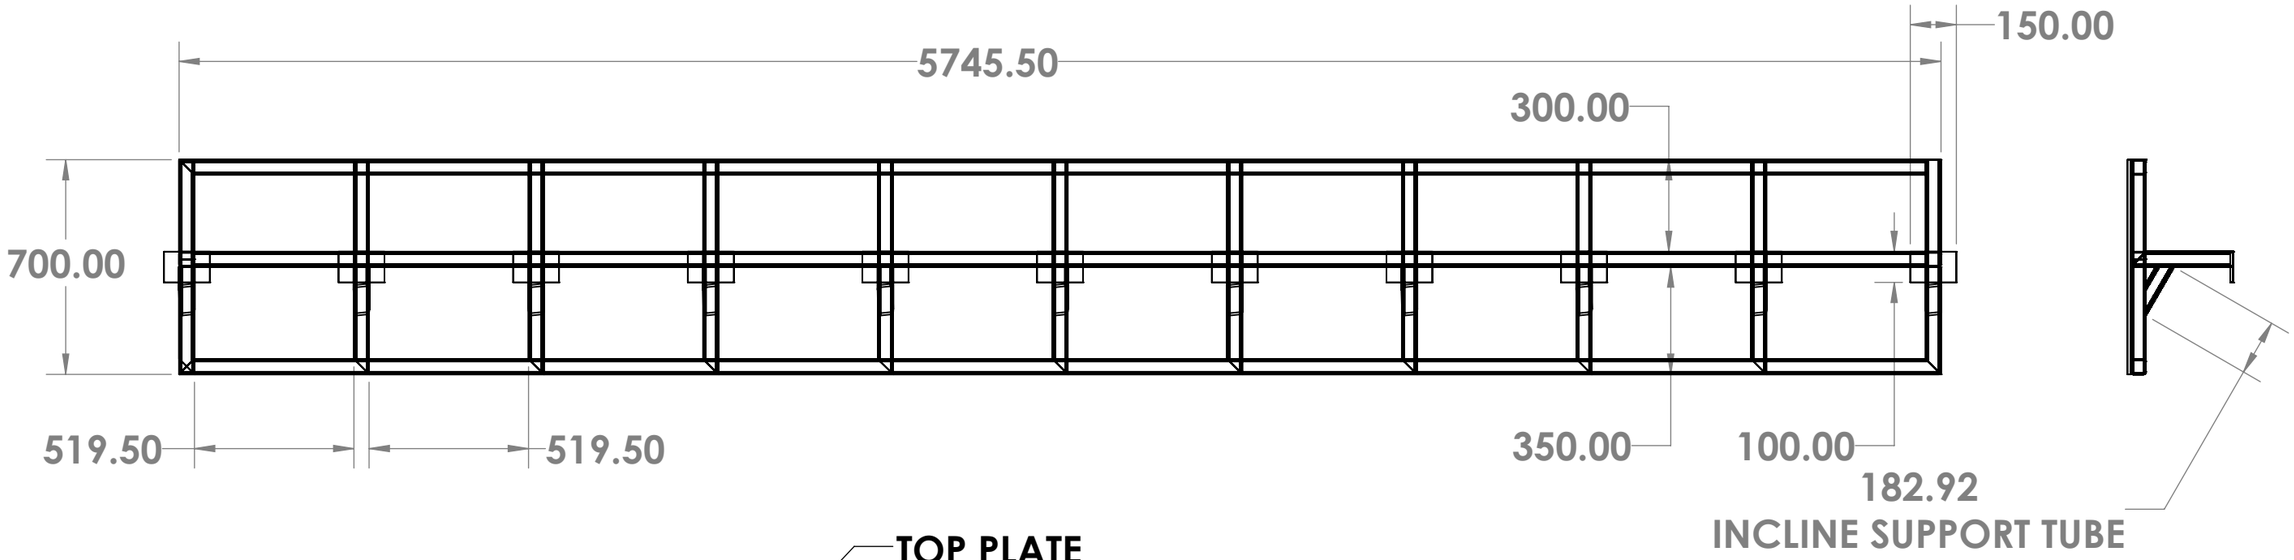

TOP PLATE
5745X850X10THK MM

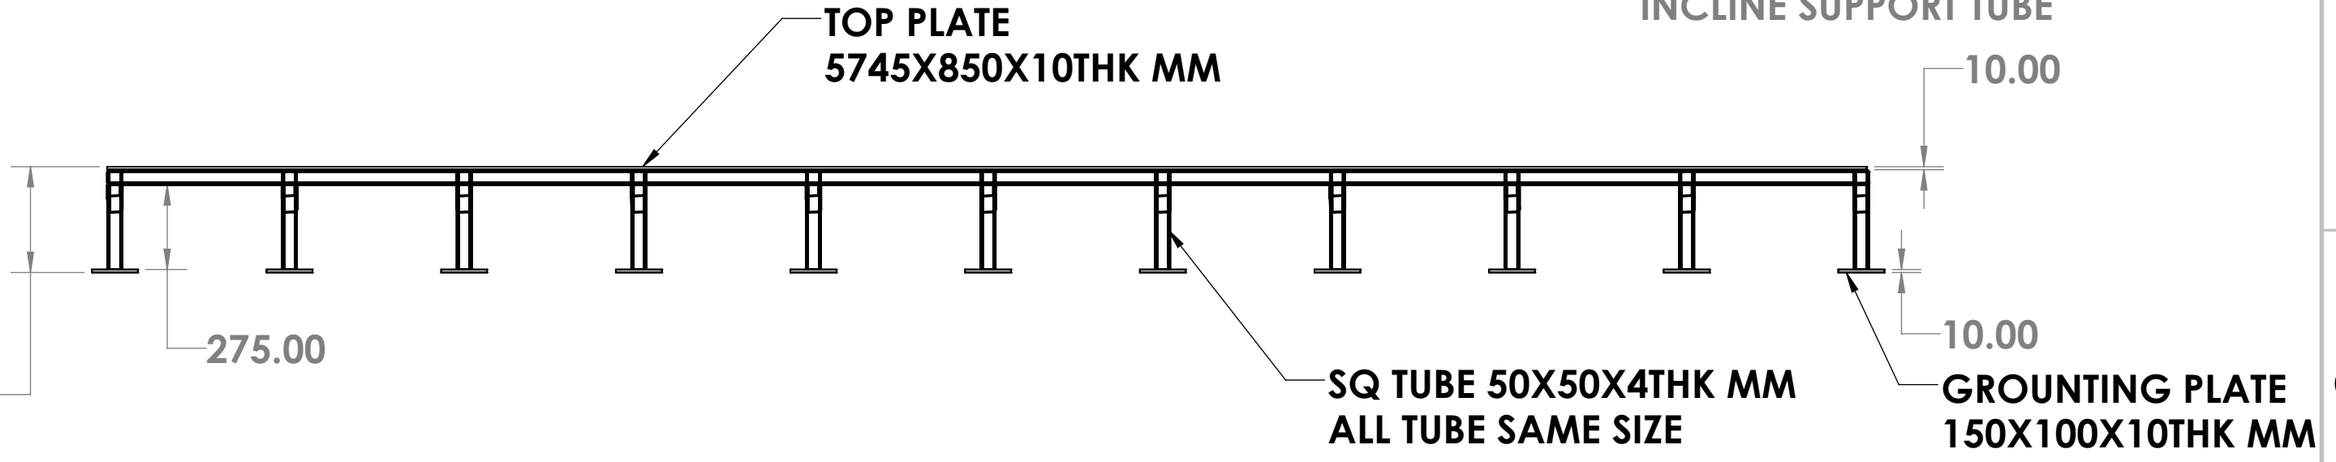
SQ TUBE 50X50X4THK MM
ALL TUBE SAME SIZE

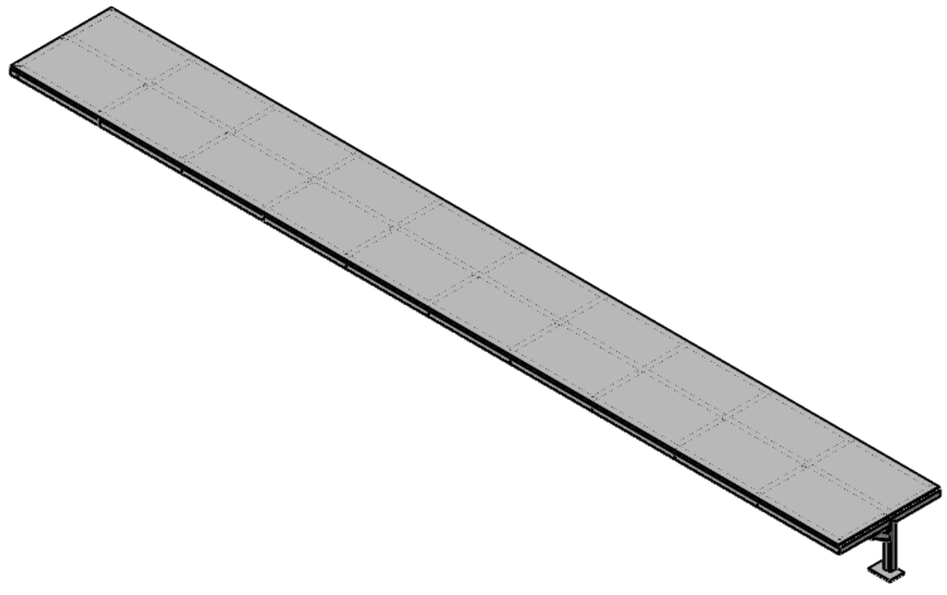
GROUNTING PLATE
150X100X10THK MM



| | | | | |
|---|---|---|---|---|
| TITLE - PROPOSED PLAN LAYOUT | | | | NIHVA TECHNOLOGIES PVT.LTD.PUNE Website - www.nihva.com |
| | NAME | SIGNATURE | DATE | CLIENT - |
| DRAWN | D.V. | | 25.07.2023 | PRODUCT - RETRACTABLE ROOF |
| CHK'D | P.M. | | 25.07.2023 | SITE LOCATION - |
| APPV'D | V.T. | | 25.07.2023 | |
| if any queries contact - supportautomation@nihva.com | | | | REVISION - 0 |
| ALL DIMENSION ARE IN mm | | A3 | | SCALE - 1.1 SHEET 2 OF 3 |



| | | | | |
|---|---|---|---|---|
| TITLE - PROPOSED PLAN LAYOUT | | | | NIHVA TECHNOLOGIES PVT.LTD.PUNE<br>Website - www.nihva.com |
| | NAME | SIGNATURE | DATE | CLIENT - |
| DRAWN | D.V. | | 25.07.2023 | PRODUCT - RETRACTABLE ROOF |
| CHK'D | P.M. | | 25.07.2023 | SITE LOCATION - |
| APPV'D | V.T. | | 25.07.2023 | |
| if any queries contact - supportautomation@nihva.com | | | | REVISION - 0 |
| ALL DIMENSION ARE IN mm | | A3 | | SCALE - 1.1 SHEET 3 OF 3 |