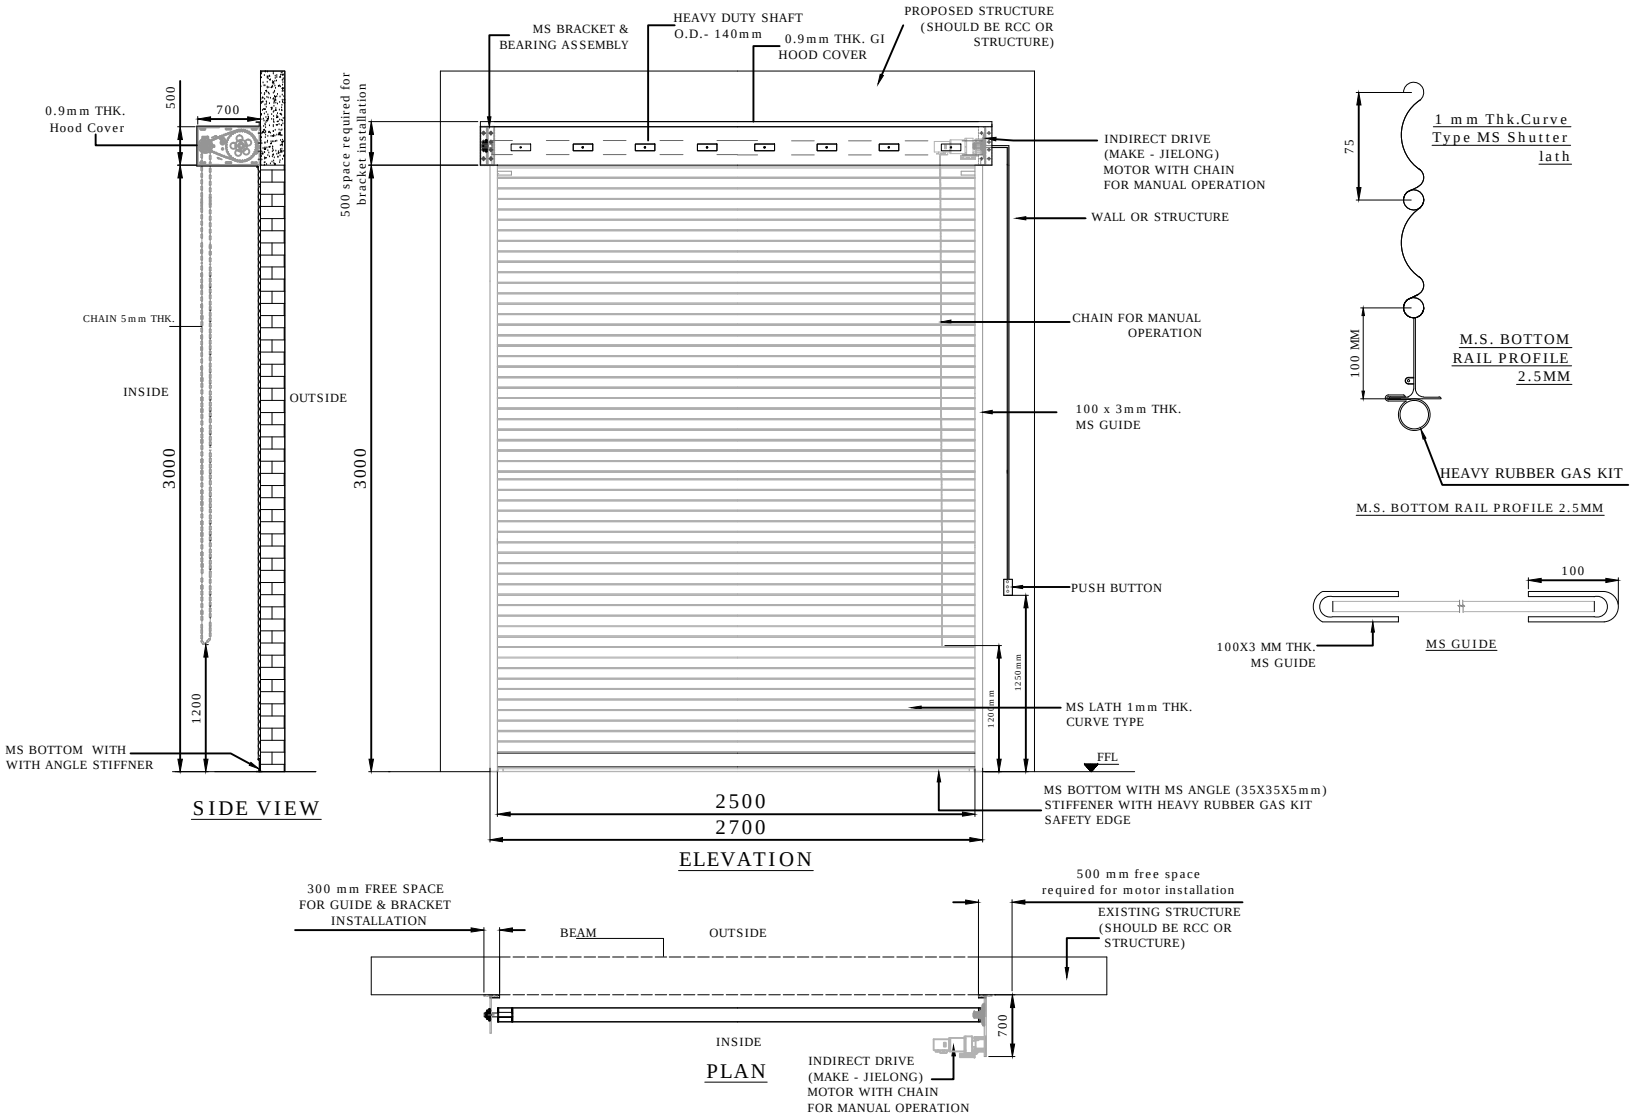


SHUTTER SPEED- APPROX. 0.05m/s

SHUTTER TYPE	CLEAR WIDTH (CW)	CLEAR HEIGHT (CH)	GUIDE SIZE	BRACKET SIZE	SHAFT SIZE (O.D)	QUANTITY	LOCATION
RSD	2500	3000	100X3mm	375X375X5mm	140mm	5	MAIN BUILDING

DIMENSION :

CLEAR WIDTH	CLEAR HEIGHT	QUANTITY
2500	3000	05 NOS

NOTE:
1.REQUIRED STRUCTURE FOR ROLLING SHUTTER WILL BE CLIENT'S SCOPE.
2.SINGLE PHASE. 3 CORE 1.5 SQ. CABLE REQUIRE AT SITE(CLIENT'S SCOPE)
3. SHUTTER WILL BE POWDER COATED CLIENT SHOULD CONFIRM RAL COLOR SHADE.
4.POWER SUPPLY LOCATION WILL BE ACTUAL SITE CONDITION.

NIHVA TECHNOLOGIES PVT. LTD.
NIHVA TECHNOLOGIES PVT. PUNE
Email:- info@nihva.com
Website:- www.nihva.com

TITLE:

MOTORIZED ROLLING SHUTTER 2.5X3m

CLIENT'S APPROVAL :

CLIENT -

PROJECT -

SITE LOCATION -

DWG. NO. : NIHVA/17-18/VDR/0197 | REV.:-0

SCALE: NTS | WT: | SHEET:1 OF 1

		DATE	SIGN.
DRAWN	OMKAR	08-01-2018	
CHECK	SHEKHAR	08-01-2018	
APPRD	SHEKHAR	08-01-2018	

If any queries contact : design@nihva.com

NOTE: ALL DIMENSIONS ARE IN mm

THIS DRAWING & DESIGN IS THE PROPERTY OF NIHVA TECHNOLOGIES. NOT TO BE SOLD OR COPIED TO ANY OTHER CONCERN.