
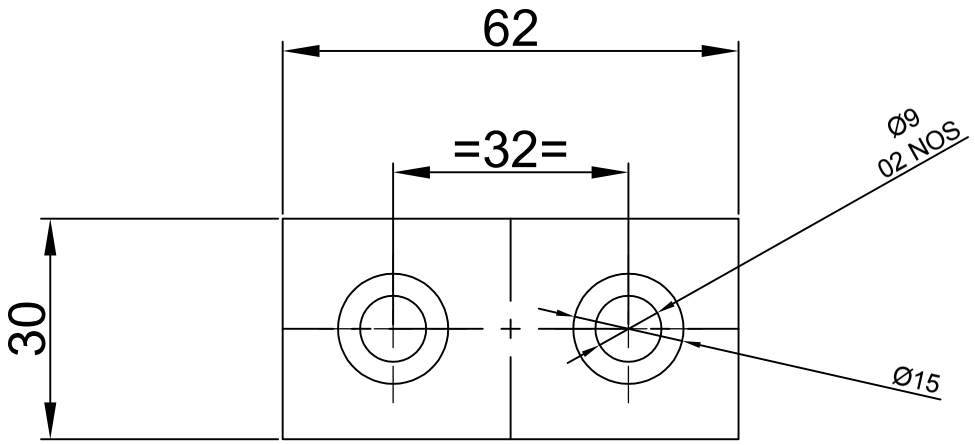


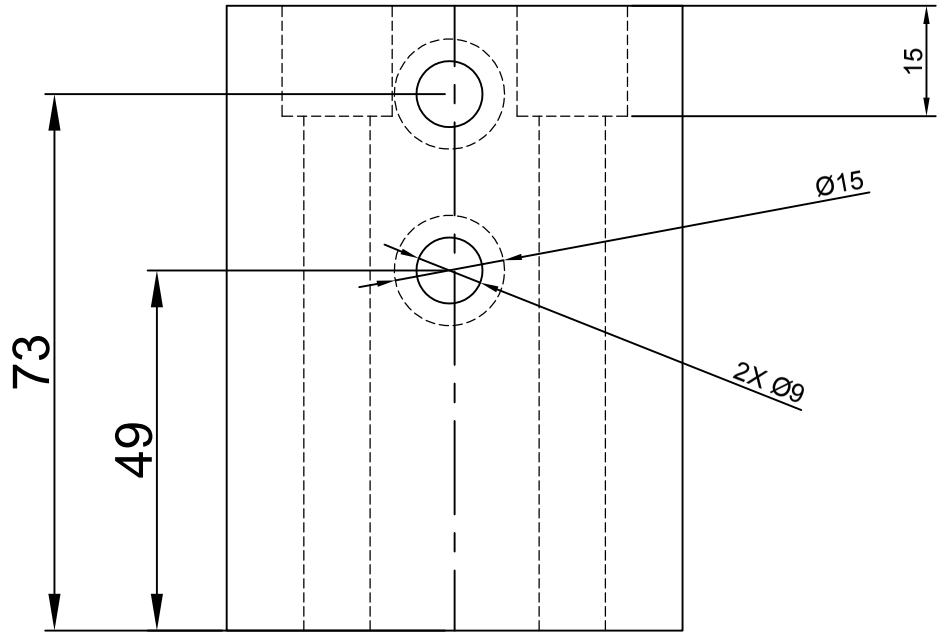

INTERLOCKING BLK-02
MATL-MS
QTY-02
DRG NO-01-24

REV NO.	DESCRIPTION	Date	Revised By

TITLE:-
INTERLOCKING BLK -02

	NAME	DATE	SIGN
DRAWN	KISHAN	05/08/22	
CHECK	GAURAV J.	05/08/22	
APPRD.	V. TARAK	05/08/22	

If any queries contact : design@nihva.com

ALL DIMENSION ARE IN mm

NIHVA
NIHVA TECHNOLOGIES PVT. LTD.

NIHVA TECHNOLOGIES PVT. LTD. PUNE
Tel : 020 66304033
Email:- info@nihva.com
Website:- www.nihva.com

CLIENT - NIHVA TECHNOLOGIES PVT.LTD
LOCATION -
PRODUCT: RETRACTABLE ROOF
DWG NO:-NIHVA/22-23/MFG/0048 | REV- 0
SCALE: NTS | SCALE:-- 1:1 | SHEET: 01 OF 01