




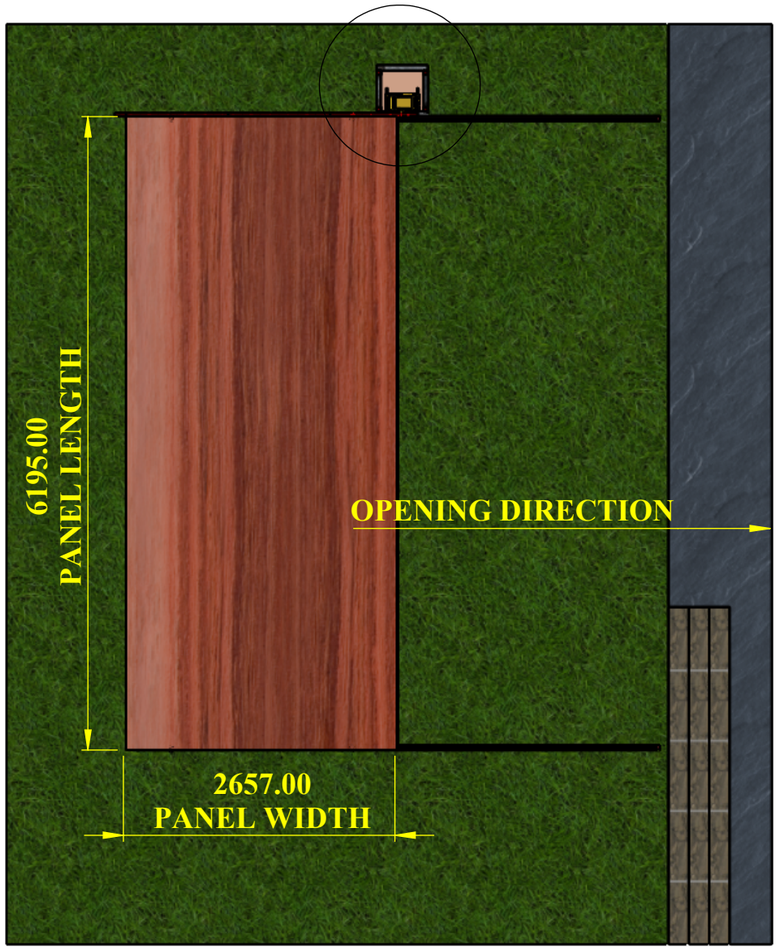


DETAIL A
SCALE 1 : 24
MOTOR ARRANGEMENT

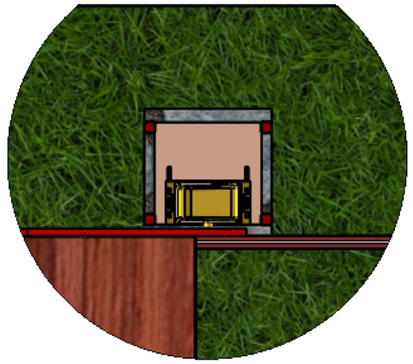


DETAIL B
SCALE 1 : 5
WHEEL MOUNTING
ARRANGEMENT

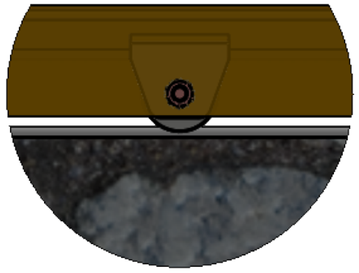

OPEN POSITION

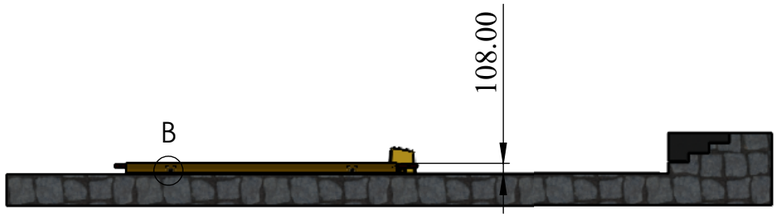



CLOSE POSITION

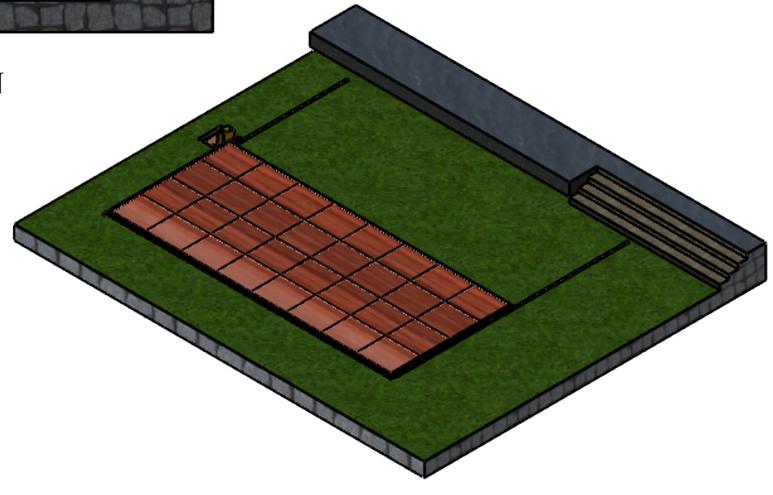


GA DRAWING

TITLE - ROOF AUTOMATION				NIHVA TECHNOLOGIES PVT.LTD.PUNE Website - www.nihva.com
DWG NO - NTPL-000-PM-001-00-00-00				
	NAME	SIGNATURE	DATE	PROJECT NO - NTPL-000-PM
DRAWN	V.W		11-06-2025	PRODUCT - SWIMMING POOL DECK
CHK'D	S.W.		11-06-2025	SITE LOCATION - PUNE
APPV'D	V.T.		11-06-2025	
if any queries contact - supportautomation@nihva.com				REVISION - QTY - 1
ALL DIMENSION ARE IN mm		A3		SCALE SHEET 1 OF 2

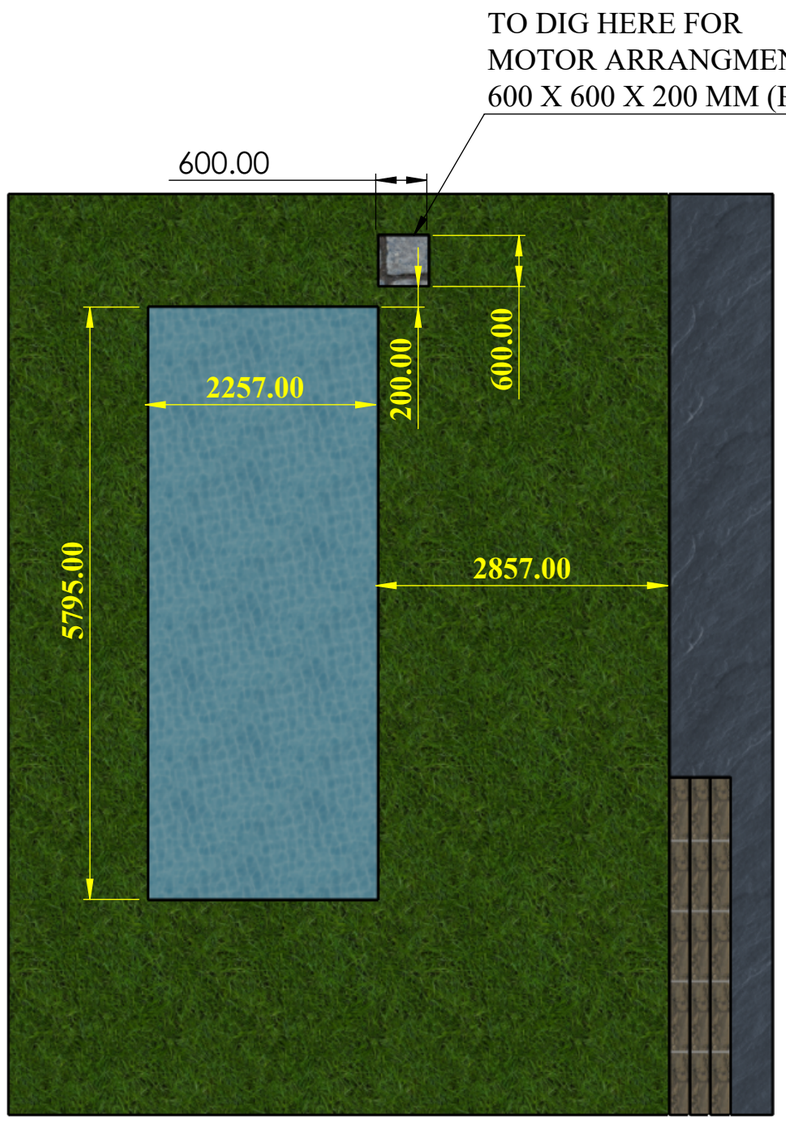


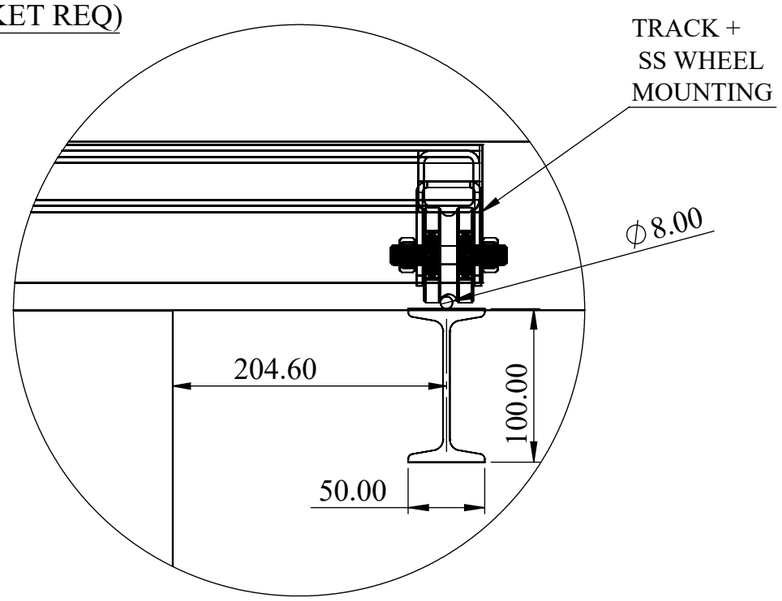


DETAIL C
SCALE 1 : 4

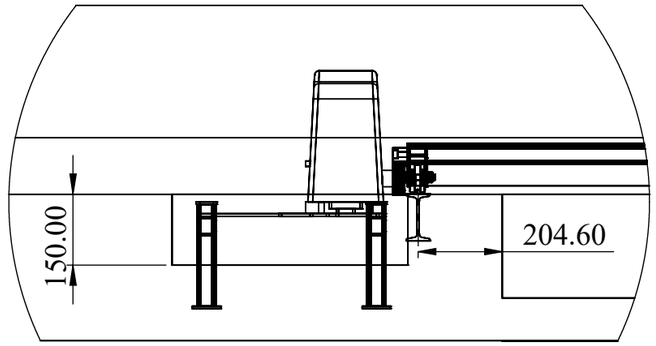

DETAIL D
SCALE 1 : 13

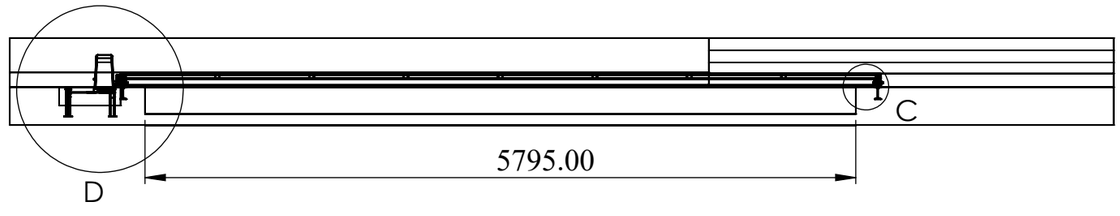

CIVIL DRAWING

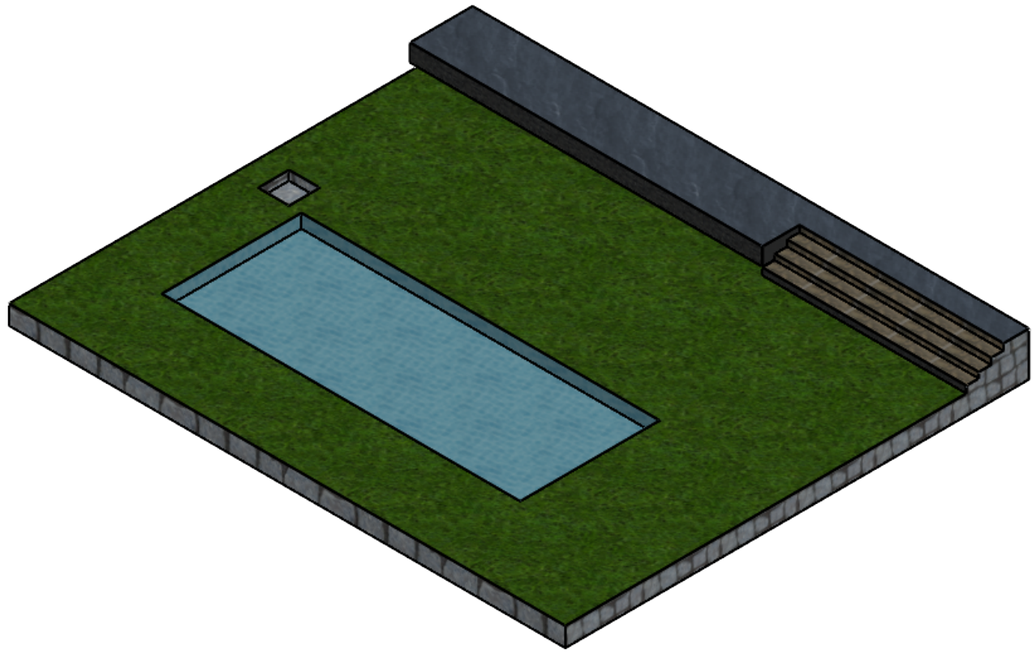

TITLE - ROOF AUTOMATION				NIHVA TECHNOLOGIES PVT.LTD.PUNE
DWG NO - NTPL-000-PM-001-00-00-00				Website - www.nihva.com
	NAME	SIGNATURE	DATE	PROJECT NO - NTPL-000-PM
DRAWN	V.W		11-06-2025	PRODUCT - SWIMMING POOL DECK
CHK'D	S.W.		11-06-2025	SITE LOCATION - PUNE
APPV'D	V.T.		11-06-2025	
if any queries contact - supportautomation@nihva.com				REVISION - / QTY - 1
ALL DIMENSION ARE IN mm		A3		SCALE / SHEET 2 OF 2