

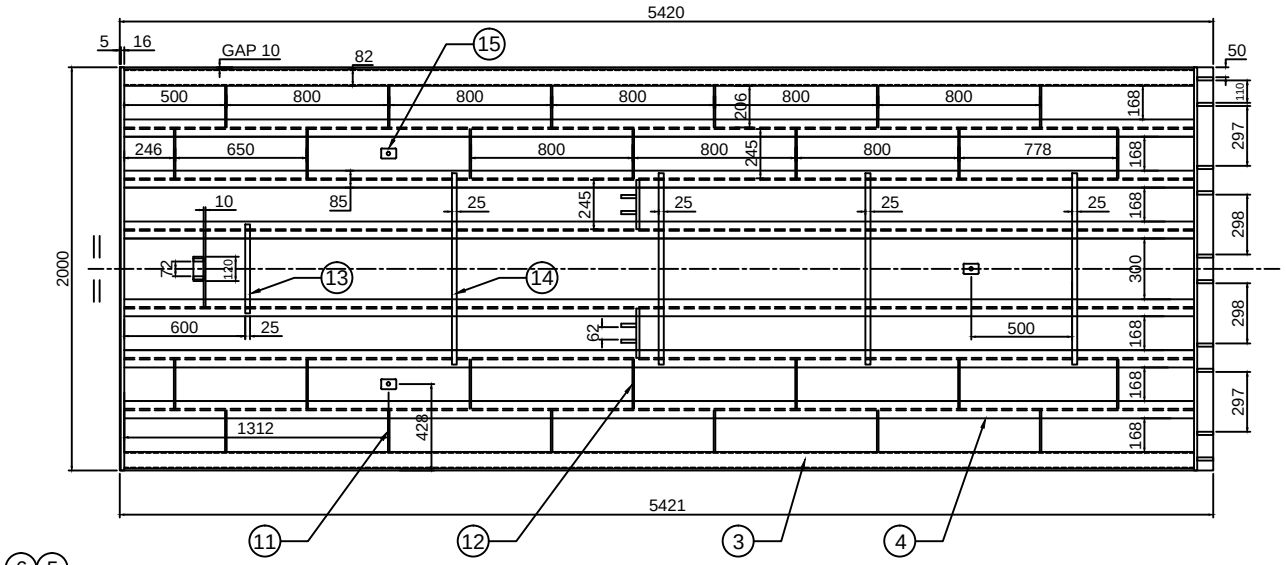


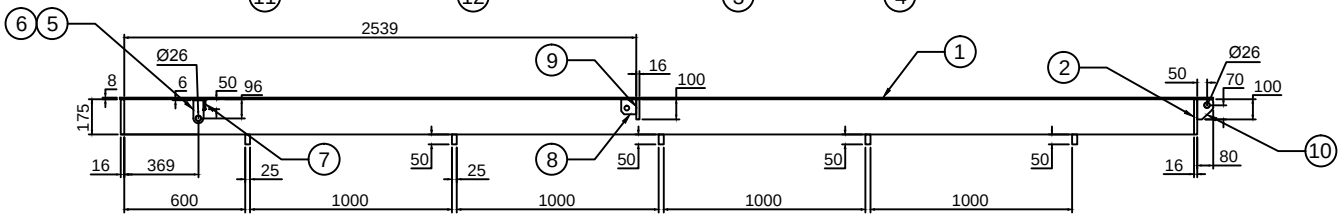

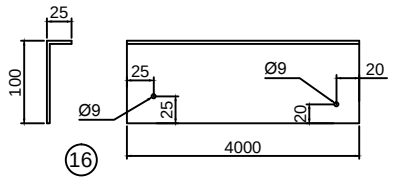

1. CHEQ.SHEET 2000 X 8 THK X 5420L = 1 NO
2. FLAT 175 X 16 X 2000L = 2 NOS
3. R.TUBE 145 X 82 X 4.8 THK X 5304L = 2 NOS
4. ISMB 175 X 85 X 5304L = 6 NOS
5. FLAT 50 X 16 X 115L = 2 NOS
6. FLAT 50 X 5 X 120L = 1 NO
7. FLAT 50 X 10 X 375L = 1 NO
8. PROFILE 75 X 16 X 75L = 4 NOS
9. FLAT 100 X 16 X 245L = 2 NOS
10. PROFILE 80 X 16 X 100L = 10 NOS
11. FLAT 145 X 8 X 200L = 12 NOS
12. FLAT 150 X 8 X 240L = 12 NOS
13. R.TUBE 50 X 25 X 3 X 440L = 1 NO
14. R.TUBE 50 X 25 X 3 X 950L = 4 NOS
15. PROFILE 50 X 16 X 75L = 3 NOS
16. L BEND 100 X 3 X 4000L = 2 NOS
17. SIDE COVER = 4 NOS

TOLERANCE :- ± 10mm

This drawing & design is the property of NIHVA TECHNOLOGIES. Not to be sold or copied to any other concern.

TITLE: DECK ASSLY

	NAME	SIGN	DATE
DRAWN	P.A		08.08.2020
CHECK	G.J		08.08.2020
APPRD.			

NIHVA TECHNOLOGIES PVT. LTD.
NIHVA TECHNOLOGIES PVT. LTD. PUNE
Tel : 020 66304033
Website:- www.nihva.com
Email:- info@nihva.com

CLIENT -

PROJECT -

SITE LOCATION -

If any queries contact : design@nihva.com

DWG. NO. : NIHVA/20-21/VDR/0026 | REV- R00

ALL DIMENSION ARE IN mm

SCALE: NTS | WT: | SHEET: 01 OF 01