




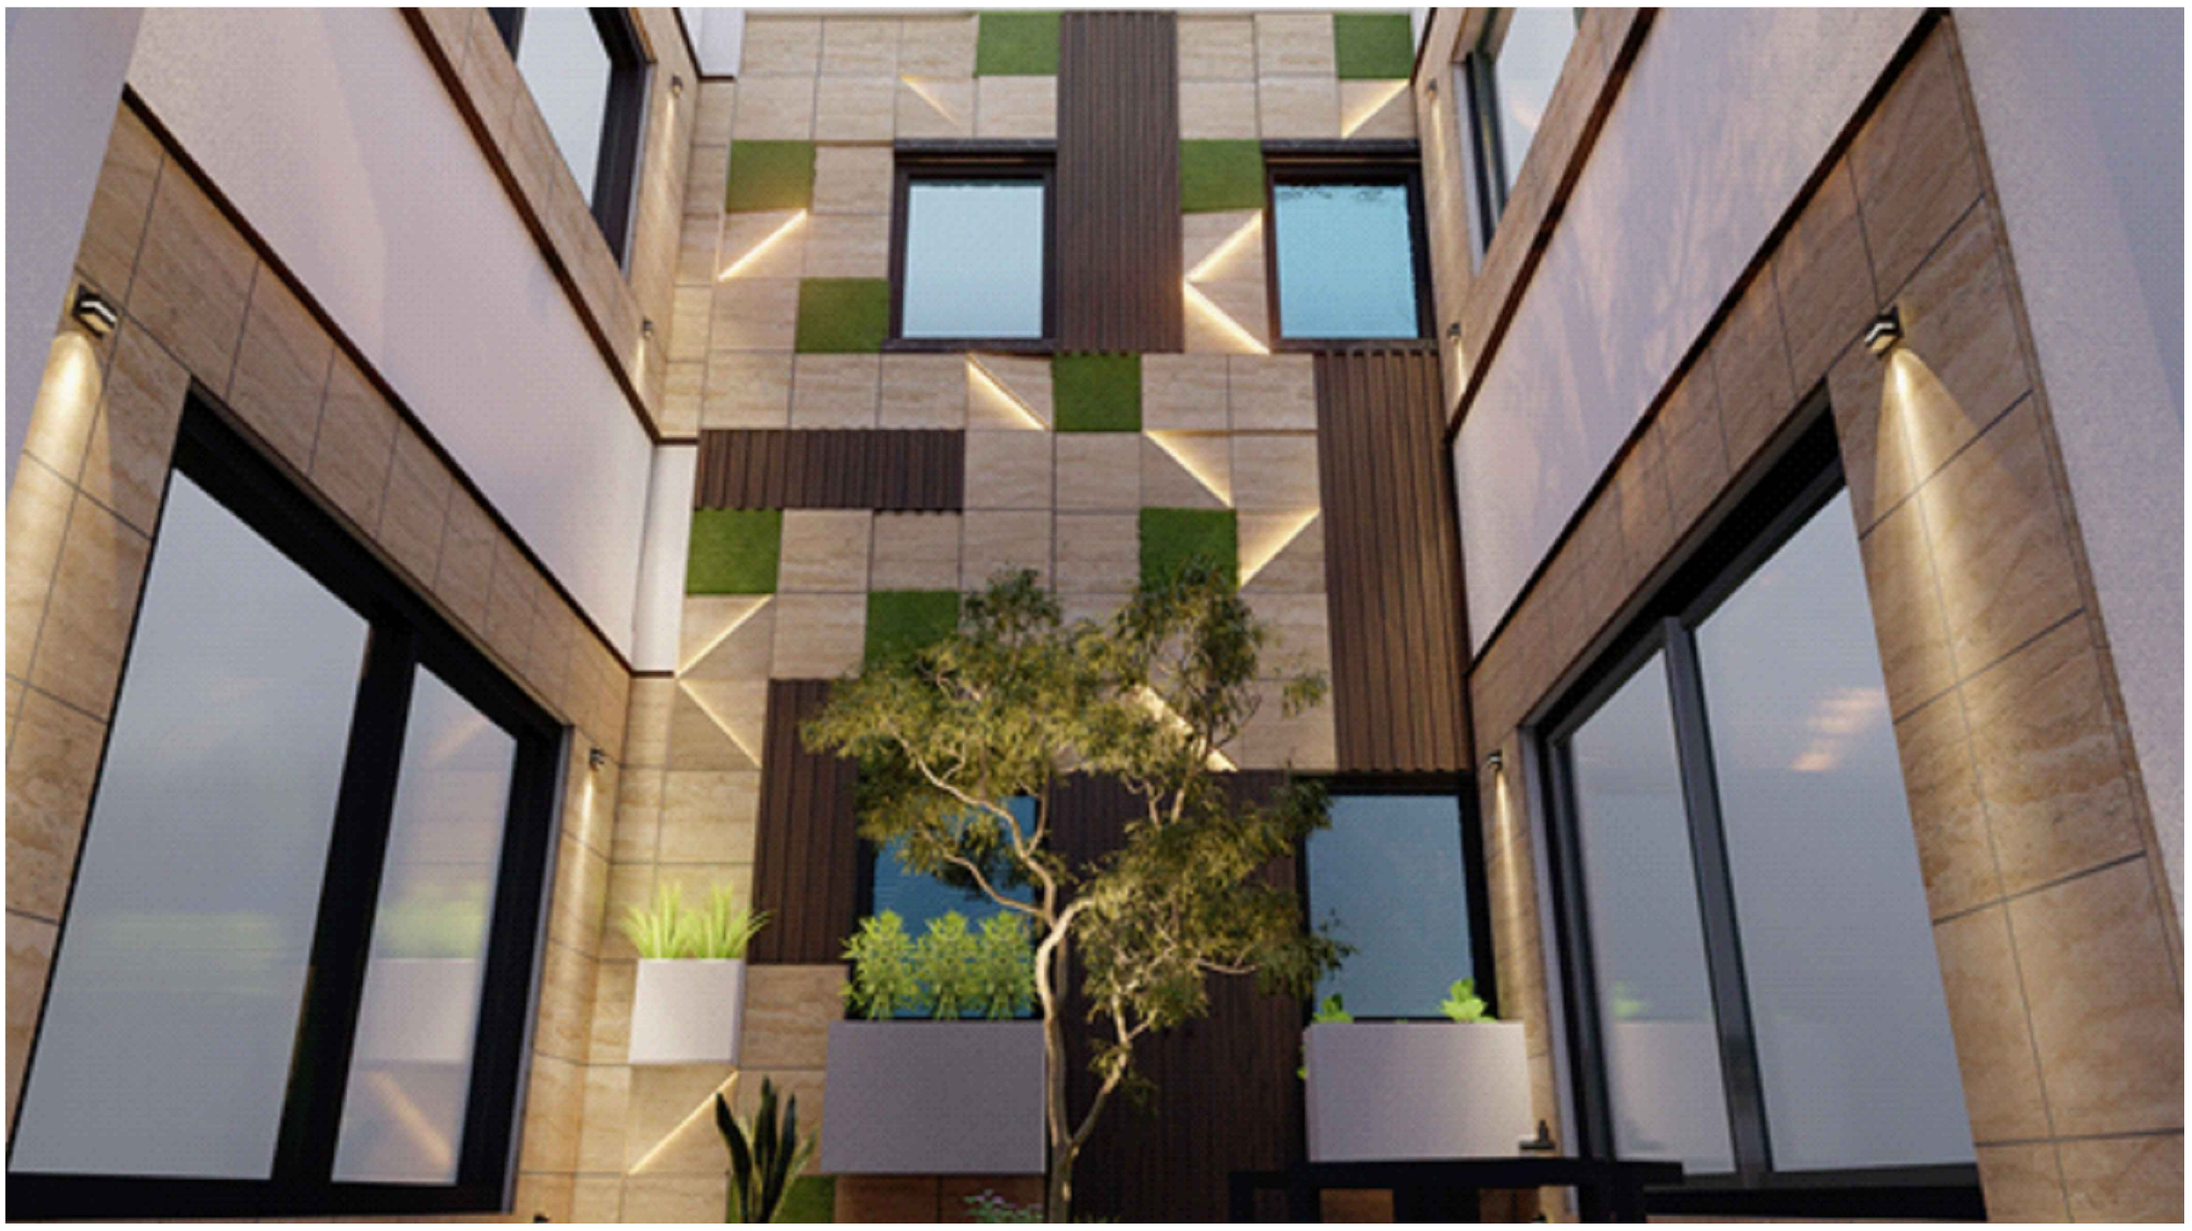

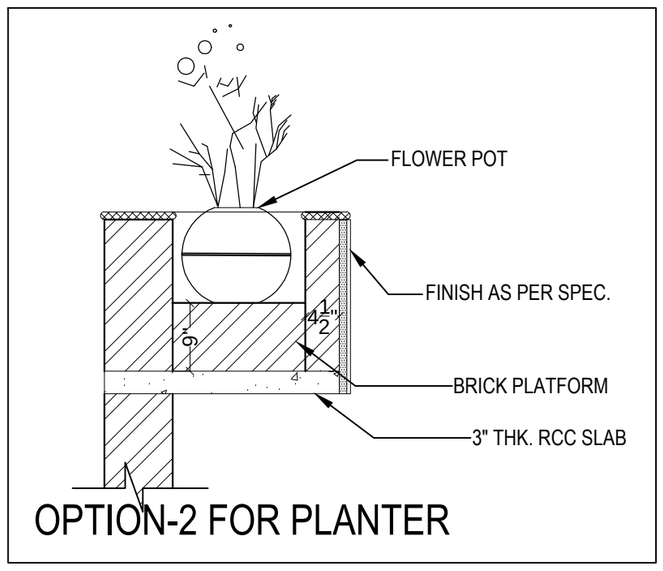

OPTION-2 FOR PLANTER

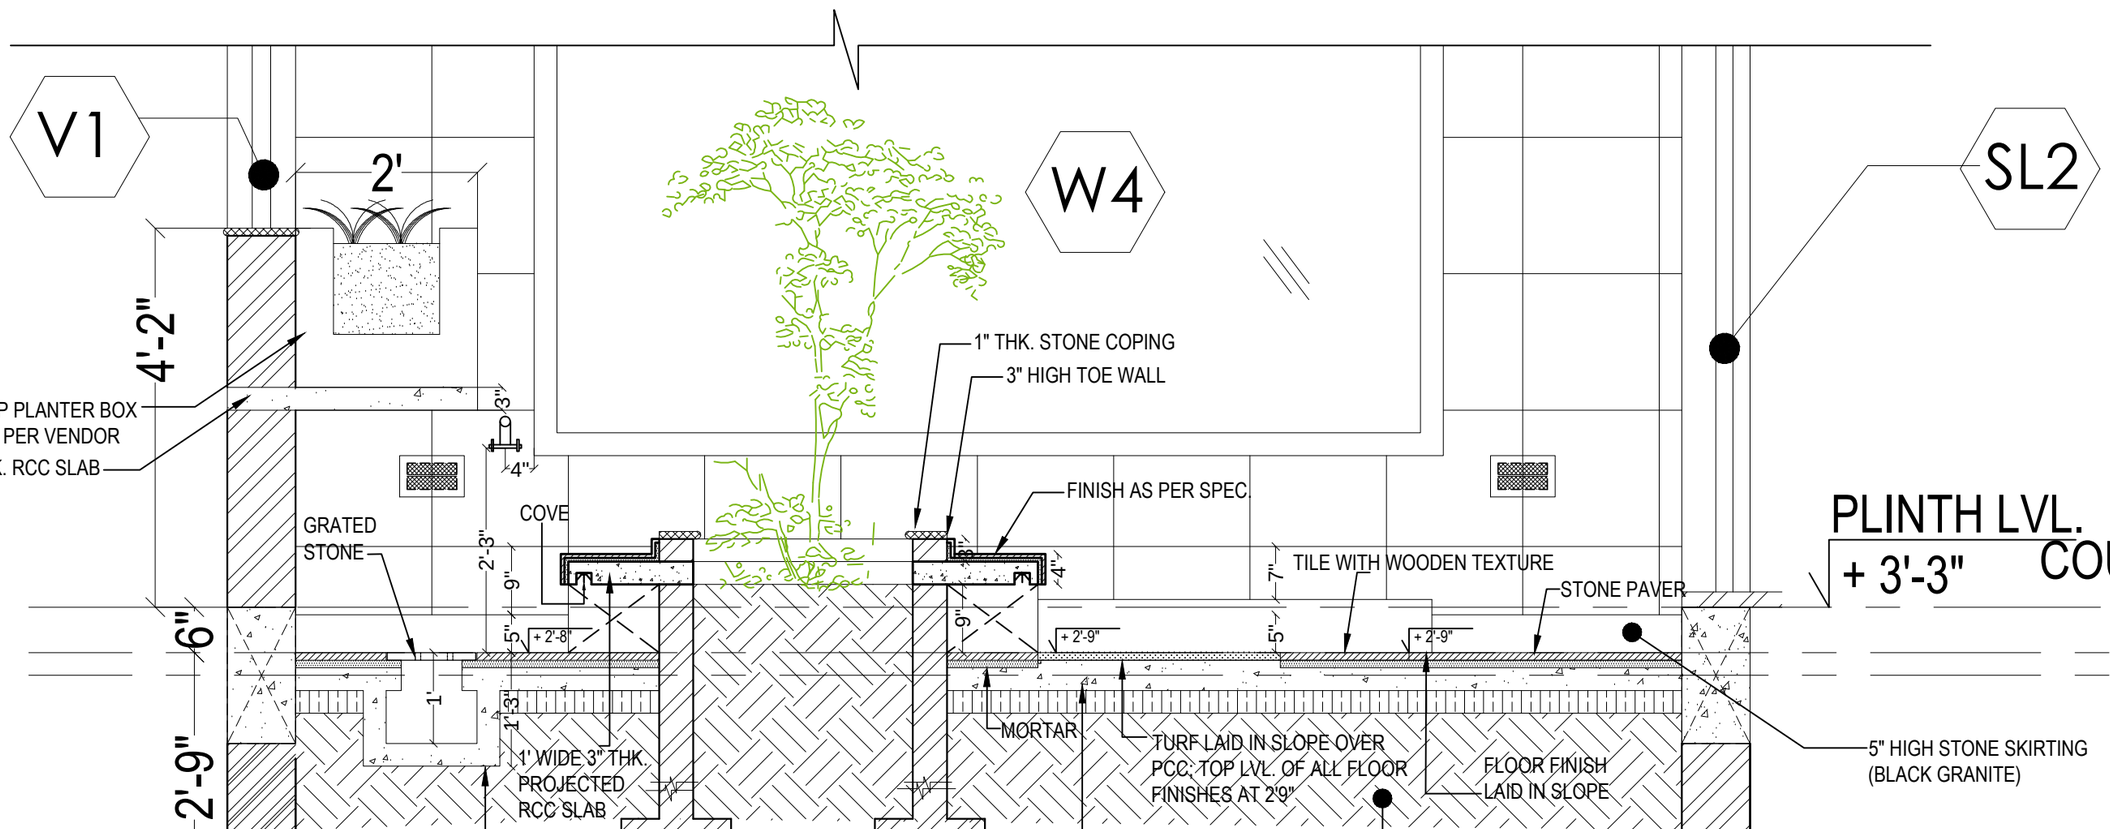

ARCHITECTS AND CONSULTANTS

AE STUDIO

an architectural design studio

A-6, GREEN PARK EXT.,
NEW DELHI-110016 , Ph.- 011 47350369
E-Mail : info@aestudio.in , Web.: www.aestudio.in

THIS DRAWING IS A "COPYRIGHT" OF THE ARCHITECT AND SHOULD NOT BE CHANGED, COPIED, REPRODUCED OR USED FOR ANY OTHER PURPOSE OR PROJECT OTHER THAN FOR WHICH IT IS ISSUED WITHOUT THE WRITTEN CONCENT OF THE ARCHITECT

NOTES -

1. READ THIS DRAWING IN CONJUNCTION WITH OTHER DRAWINGS FOR THIS PROJECT.
2. DO NOT SCALE THIS DRAWING, ONLY WRITTEN DIMENSIONS ARE TO BE FOLLOWED.
3. DISCREPANCY IF ANY MUST BE BROUGHT TO THE NOTICE OF THE ARCHITECT IMMEDIATELY.
4. ALL THE DIMENSIONS HAS TO BE TAKEN FROM FINISH FLOOR LEVEL

CLIENT: MR. DHAMIJA

PROJECT: DHAMIJA RESIDENCE

DRAWING TILTLE: COURTYARD SECTION BB'

BUILDING BLOCK/FLOOR: COURTYARD

S.NO.	DATE	REVISION / COMMENTS

PROJECT NO.: 271

DRAWN BY: SHITI

CHECKED BY: SANDEEP

SCALE: N.T.S.

DATE: ----

DRAWING TYPE: GFC

SHEET NO.: 18 OF

DRAWING NAME.: FB~SD~COURTYARD.dwg

FILE LOCATION: \\dataserver\Project New\RESIDENCE CIVIL\Ongoing\FARIDABAD\DHAILASH DHAMIJA (PROJECT NO 271)\WORKING\DHAMIJA RES.MARKING PLAN