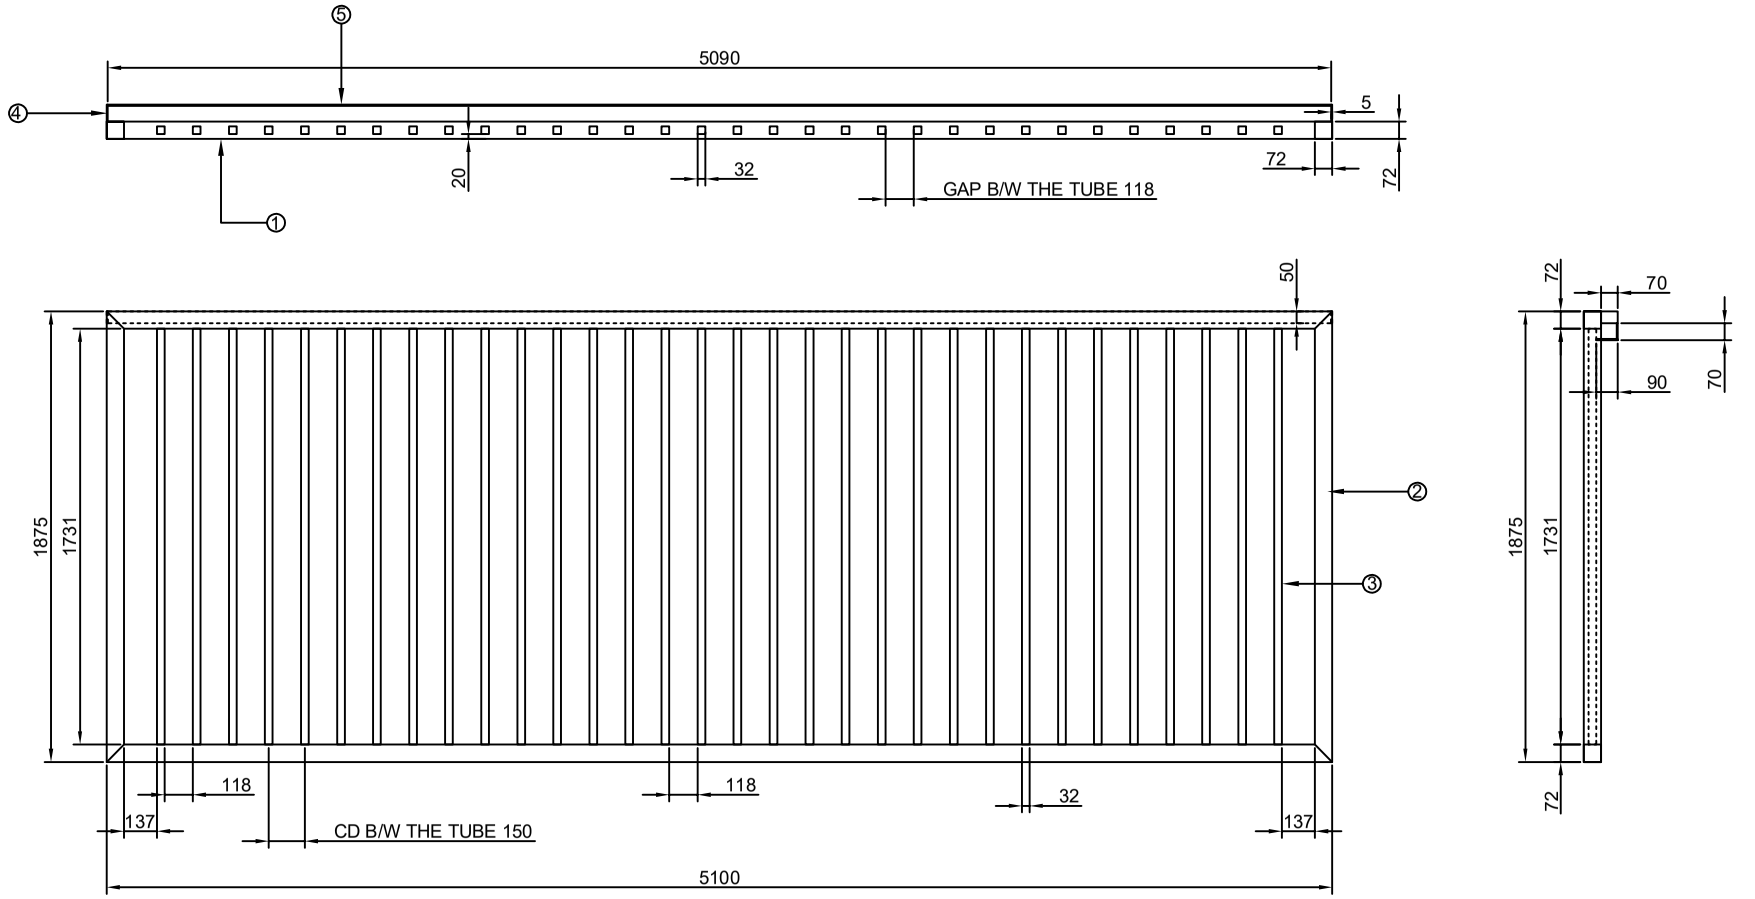


QTY-02

BOM FOR SINGLE LEAF			
SL NO.	DESCRIPTION	SPECIFICATION	QTY
1	MS SQ. TUBE	72X72X3.2X5100	2NOS
2	MS SQ. TUBE	72X72X3.2X1875L	2NOS
3	MS SQ. TUBE	32X32X2.6X1731L	32NOS
4	MS BRIGHT FLAT	50X5X70L	2NOS
5	MS BRIGHT FLAT	50X5X5090L	1NO

This drawing & design is the property of NIHVA TECHNOLOGIES. Not to be sold or copied to any other concern.

TITLE:-
5100MM LENGTH LEAF

NIHVA
NIHVA TECHNOLOGIES PVT. LTD.

	NAME	DATE	SIGN
DRAWN	SUJATA	10/06/2023	
CHECK			
APPRD.			

If any queries contact : design1@nihva.com

ALL DIMENSION ARE IN mm

CLIENT - EIRICH
LOCATION - Pune
PRODUCT - Automatic Sliding Gate — QTY-02
DWG NO:- NIHVA/22-23/MFR/0092 — REV-00
SCALE: NTS — SCALE:-- 1:1 — SHEET: 01 OF 01

Rev No.	Revision	Date	Revised By