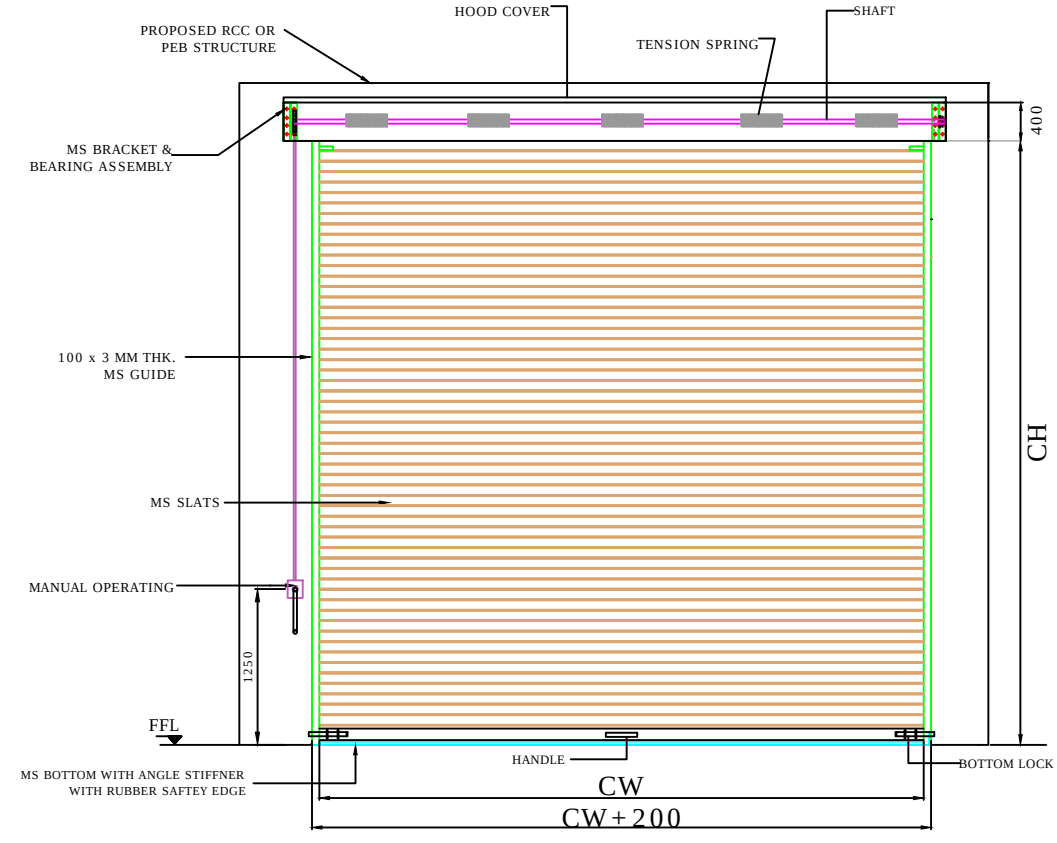


INSIDE ELEVATION

PLAN

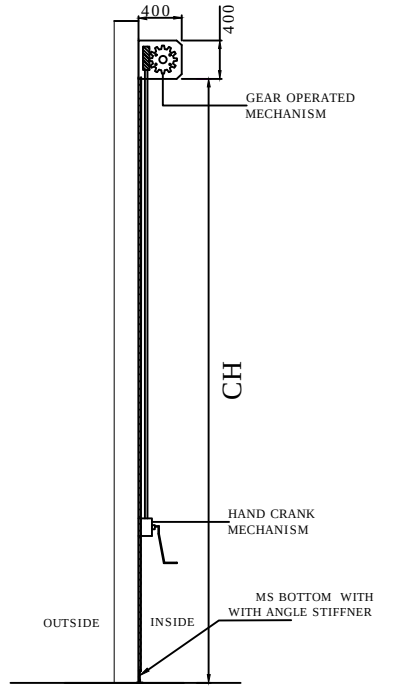


SIDE VIEW

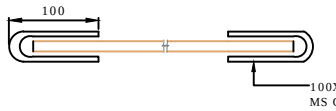


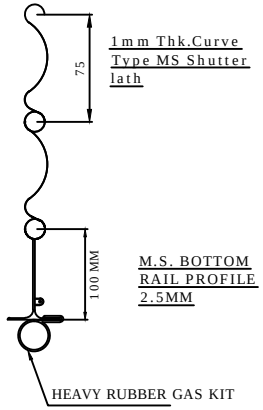


| SHUTTER TYPE | CLEAR WIDTH (CW) | CLEAR HEIGHT (CH) | QUANTITY | LOCATION | INSTALLATION |
|---|---|---|---|---|---|
| RS3A | 3000 | 3000 | 1 | A11-A12 | INSIDE |

REV1-COLOUR SCHEME OF ROLLING SHUTTER HAS BEEN UPDATED WITH APPROVED RAL SHADE 5012(LIGHT BLUE).

DIMENSION :

| CLEAR WIDTH | CLEAR HEIGHT | QUANTITY |
|---|---|---|
| 3000 | 3000 | 1 |

MATERIAL:

THICKNESS :

NOTE:
1.REQUIRED STRUCTURE FOR ROLLING SHUTTER WILL BE CLIENT'S SCOPE.
2.ONE COAT OF RED OXIDE PRIMER WILL BE GIVEN TO THE SHUTTER.
3.FOR FINAL FINISH CLIENT SHOULD MENTION COLOR SHADE FOR ROLLING SHUTTER.
4.TWO COAT OF SYNTHETIC ENAMEL PAINT APPROVED RAL 5012 LIGHT BLUE WILL BE GIVEN TO THE SHUTTER

NIHVA TECHNOLOGIES PVT. LTD.
NIHVA TECHNOLOGIES PVT. LTD. PUNE
Email:- info@nihva.com
Website:- www.nihva.com

TITLE:

# GEAR OPERATED ROLLING SHUTTER

CLIENT'S APPROVAL :

CLIENT - SCON

PROJECT - BEKAERT INDUSTRIES PVT. LTD.

SITE LOCATION - RANJANGAON

DWG. NO. : NIHVA/16-17/207/R01

| SCALE: NTS | WT: | SHEET:1 OF 1 |
|---|---|---|

| | |
|---|---|
| DRAWN BY: SURAJ | DATE: 31-03-2017 |
| CHECK BY : SAGAR P. | DATE: 31-03-2017 |
| APPROVED BY : R.K | DATE: 31-03-2017 |

If any queries contact : projects@nihva.com

NOTE: ALL DIMENSIONS ARE IN mm

THIS DRAWING & DESIGN IS THE PROPERTY OF NIHVA TECHNOLOGIES. NOT TO BE SOLD OR COPIED TO ANY OTHER CONCERN.