


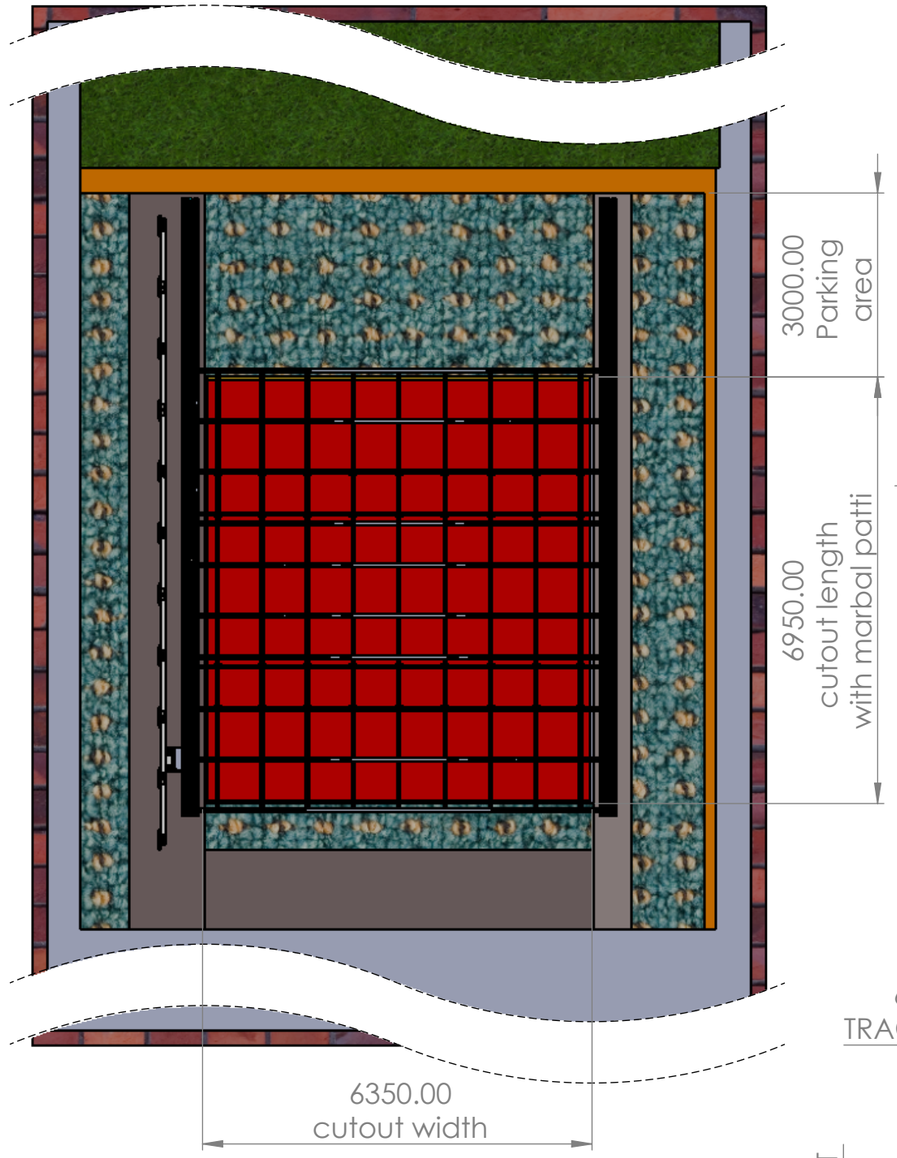


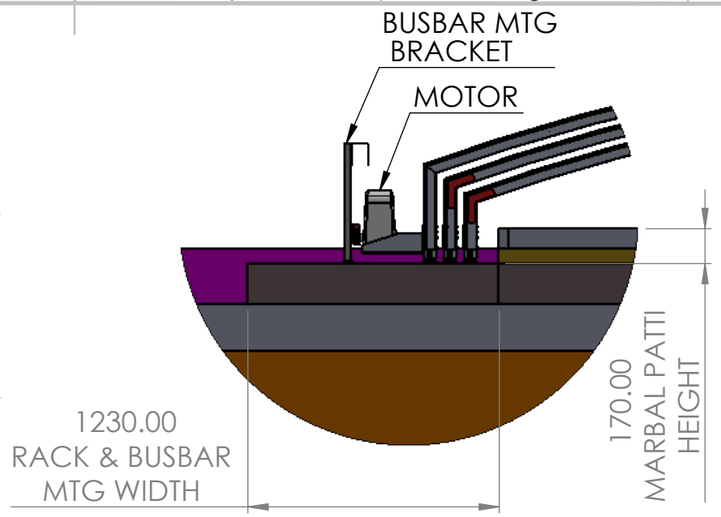


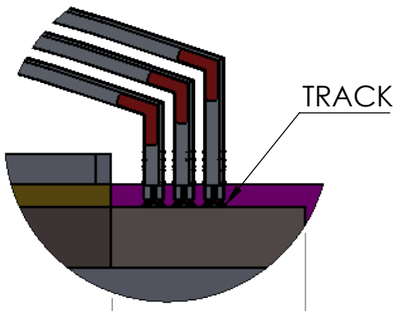

DETAIL B
SCALE 1 : 30

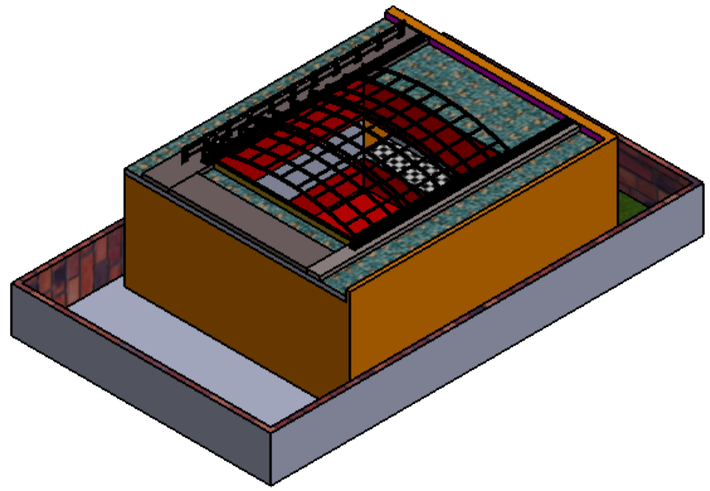


DETAIL C
SCALE 1 : 20

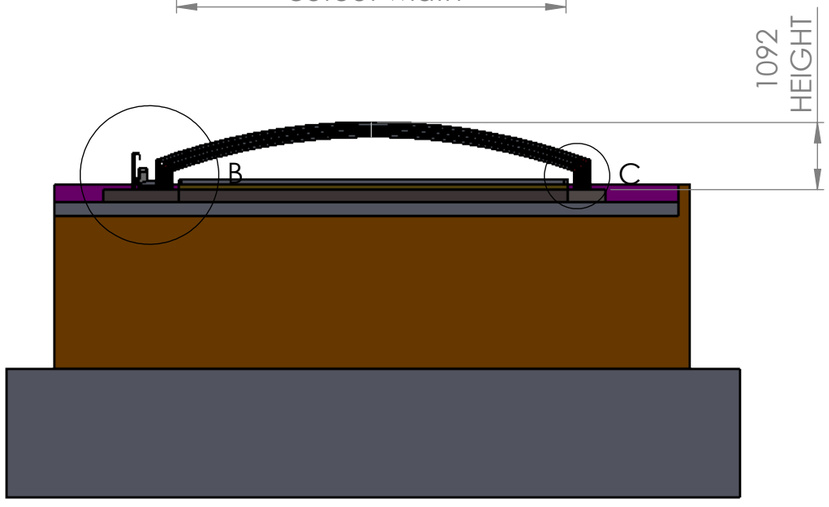




| | | | |
|---|---|---|---|
| TITLE : | GA | | |
| | NAME | SIGNATURE | DATE |
| DRAWN | SURAJ . W | | 28-03-2025 |
| CHK'D | PRANAV M. | | 28-03-2025 |
| APPV'D | VIJAY T. | | 28-03-2025 |
| | | DIMENSIONS ARE IN MILLIMETERS | |

NIHVA Technologies Pvt. Ltd.

NIHVA TECHNOLOGIES PVT LTD

| | |
|---|---|
| CLIENT NAME : | SALAVI MAM |
| PRODUCT NAME : | RETRACTABLE ROOF |
| SITE LOCATION : | GUJARAT |
| DWG NO. | GA |
| | A3 |
| | REVISION : 0 |
| SCALE: | SHEET 1 OF 1 |