
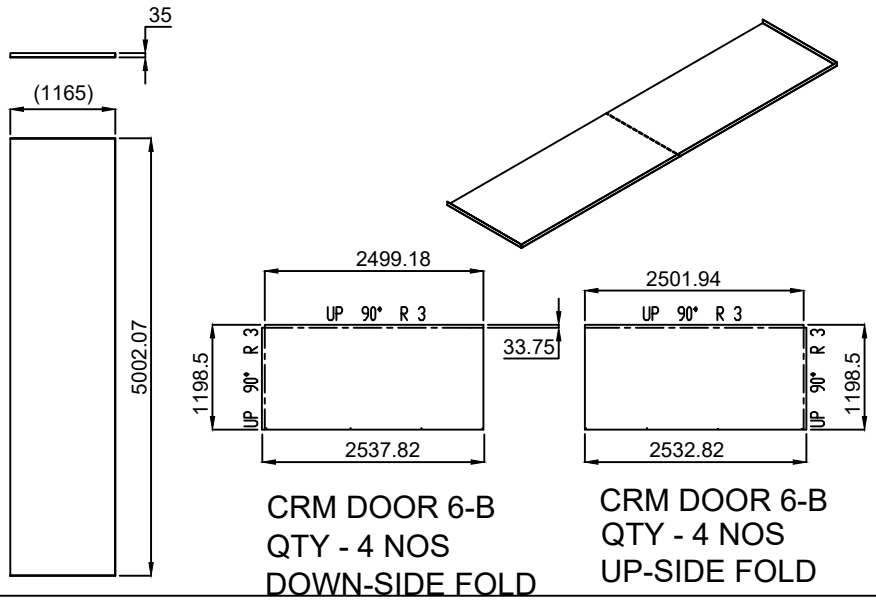


CRM DOOR 6-B
QTY - 4 NOS
DOWN-SIDE FOLD


CRM DOOR 6-B
QTY - 4 NOS
UP-SIDE FOLD

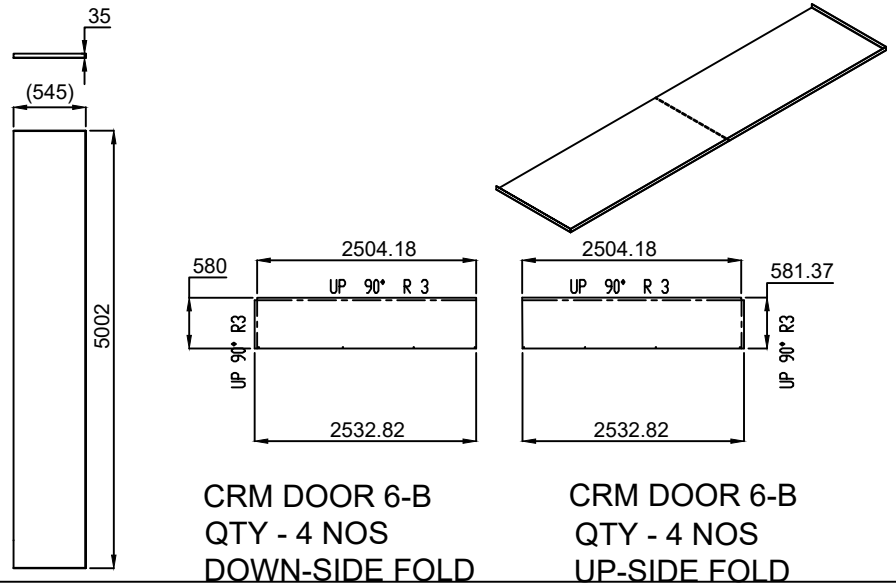

CRM DOOR 6-B
QTY - 4 NOS
DOWN-SIDE FOLD

CRM DOOR 6-B
QTY - 4 NOS
UP-SIDE FOLD

CRM DOOR ALL
QTY - 16 NOS / each sheet all qty

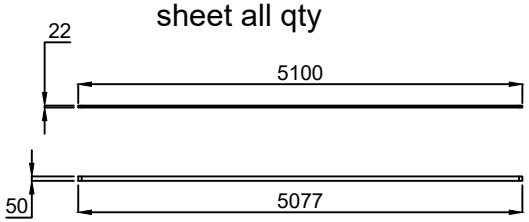

PPGI SHEET 1 MM

NOTE: DURING BENDING CRITICAL DIMENSION SHOULD BE MANDETORY

REV.	REVISION DESCRIPTION	Date	Revised By
000	MODIFIED DUE TO RECIEVED COIL SIZE 1210 MM INSTEAD OF 1250 MM	22/05/2022	MAHESH S.

This drawing & design is the property of NIHVA TECHNOLOGIES. Not to be sold or copied to any other concern.

TITLE:- 4 LEAF BOTH SIDE CRM DOOR 06_B

	NAME	DATE	SIGN
DRAWN	M.SUTAR	22/05/2022	
CHECK	M.SUTAR	22/05/2022	
APPRD.			

NIHVA TECHNOLOGIES PVT. LTD.
NIHVA TECHNOLOGIES PVT. LTD. PUNE
Tel : 020 66304033
Email:- info@nihva.com
Website:- www.nihva.com

CLIENT - NIHVA TECHNOLOGIES PVT.LTD
LOCATION -
PRODUCT - SLIDING DOOR - PPGI CLADDING

If any queries contact : design@nihva.com
DWG NO:-NIHVA/22-23/VDR/0015 REV- 0
ALL DIMENSION ARE IN mm
SCALE: NTS SCALE:-- 1:1 SHEET: 02 OF 02