
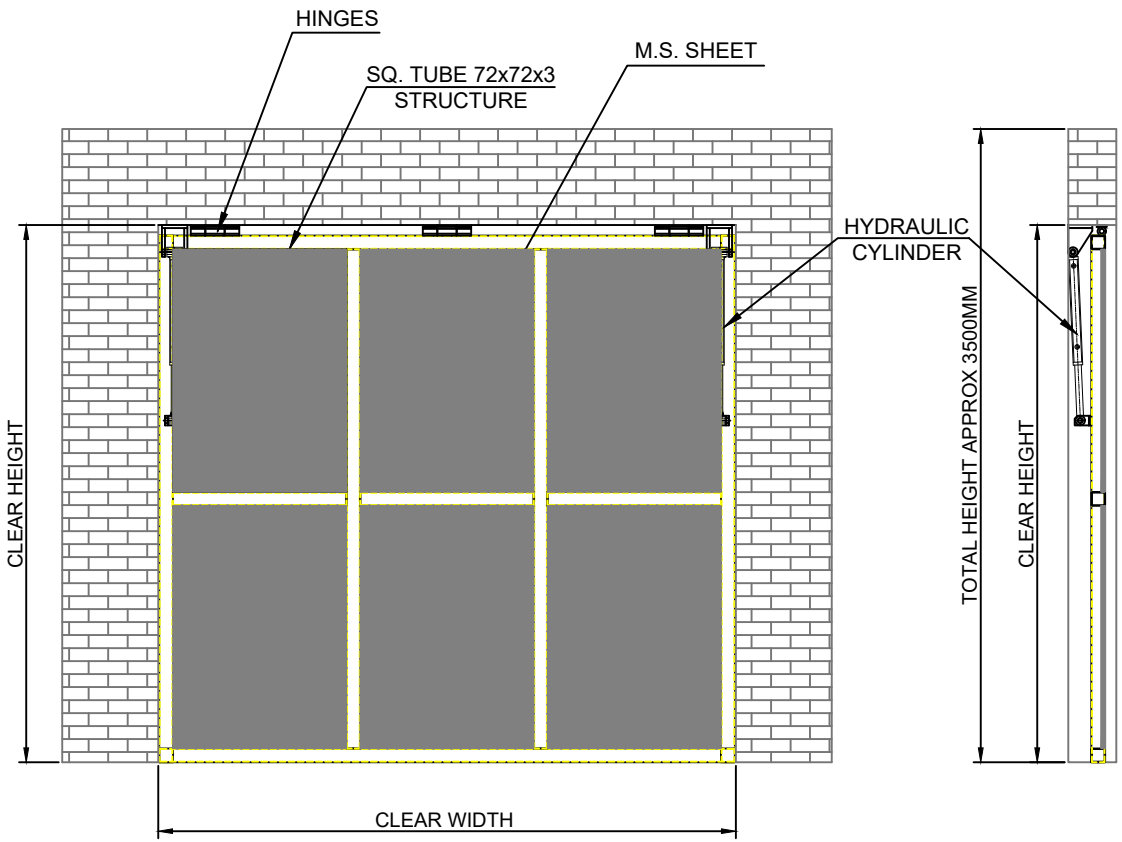


CYL. IN CLOSE POSITION

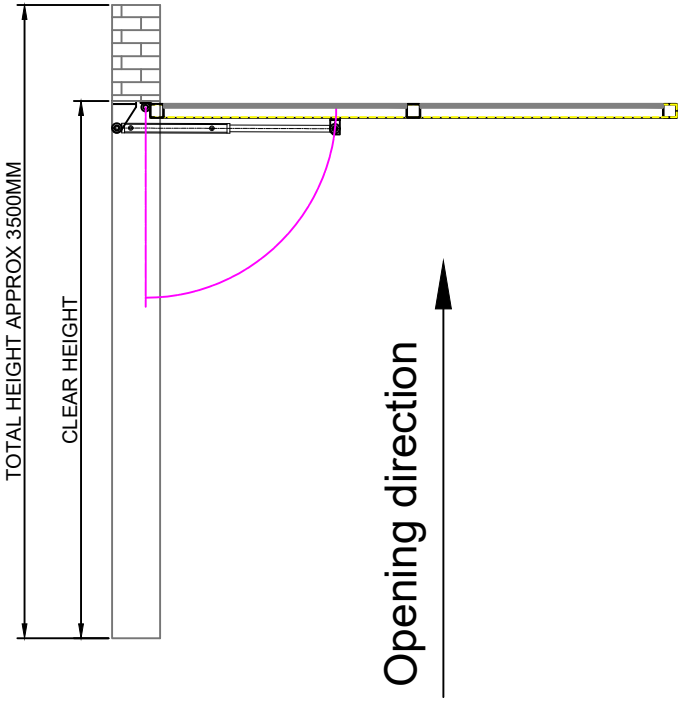

CYL. IN CLOSE POSITION

DOOR SIZES			
SL NO.	CLEAR WIDTH	CLEAR HEIGHT	QTY
1	3000 mm	2743.2 (9 FEET)	1 NO
2	3352.8 mm	2438.4 (8 FEET)	1 NO
3	3200 mm	2743.2 (9 FEET)	1 NO

Note:-

1.All Dimension are in MM.

2.All Civil work and if required motor foundation or ms bracket will be in Client scope

3.Civil,Installation and Fabrication Tolerance will be ±20mm

4.Gate weight will be approx. 300 - 400kg

5.Required structure will be client scope

Rev No.	Revision	Date	Revised By

This drawing & design is the property of NIHVA TECHNOLOGIES. Not to be sold or copied to any other concern.

TITLE:- VERTICAL SWING DOOR CUM ROOF

NIHVA TECHNOLOGIES PVT. LTD.

	NAME	DATE	SIGN
DRAWN	NIRMALA	02/08/2023	
CHECK	A.K	02/08/2023	
APPRD.	V.T	02/08/2023	

If any queries contact : design@nihva.com

ALL DIMENSION ARE IN mm

CLIENT - SAGAR DHAWADE

LOCATION -

PRODUCT - VERTICAL SWING DOOR CUM ROOF | QTY-00

DWG NO:- NIHVA/23-24/CLT/047 | REV-00

SCALE: NTS | SCALE:-- 1:1 | SHEET: 01 OF 01