



M12X60mm HEX BOLT SHOULD BE WELDED TO PLATE BEFORE INSERTING IN FOUNDATION (CLIENT'S SCOPE)

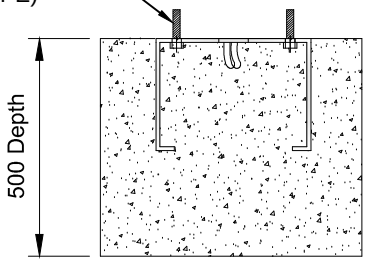

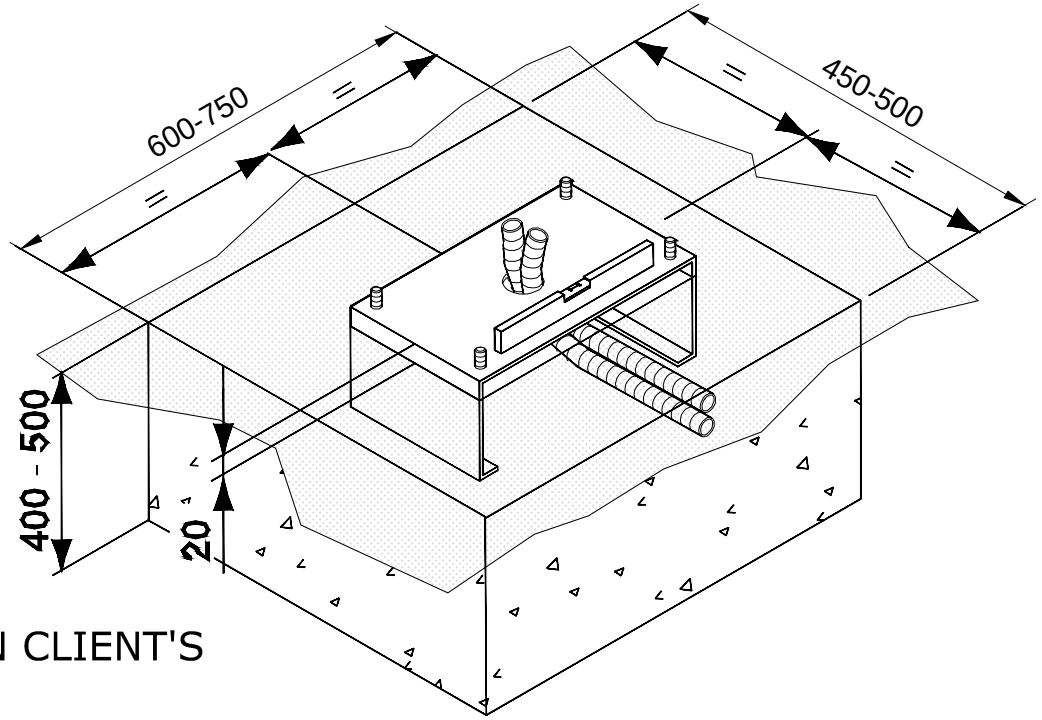

FOUNDATION DETAILS (IN CLIENT'S SCOPE)

TOLERANCE - ±10mm

This drawing & design is the property of NIHVA TECHNOLOGIES. Not to be sold or copied to any other concern.

TITLE: FOUNDATION FOR BOOM BARRIER	NIHVA TECHNOLOGIES PVT. LTD.	NIHVA TECHNOLOGIES PVT. LTD. PUNE Tel : 020 66304033 Email:- info@nihva.com Website:- www.nihva.com

	SIGN	DATE
DRAWN	OMKAR	17-11-2017
CHECK	SHEKHAR.	17-11-2017
APPROVAL	SHEKHAR	17-11-2017

CLIENT - LUPIN LIMITED		
PROJECT -		
SITE LOCATION - MIHAN,NAGPUR		
DWG. NO. : NIHVA/17-18/ 0280		REV-0
SCALE: NTS	WT:	SHEET: 01 OF 01

If any queries contact : projects@nihva.com

ALL DIMENSION ARE IN mm