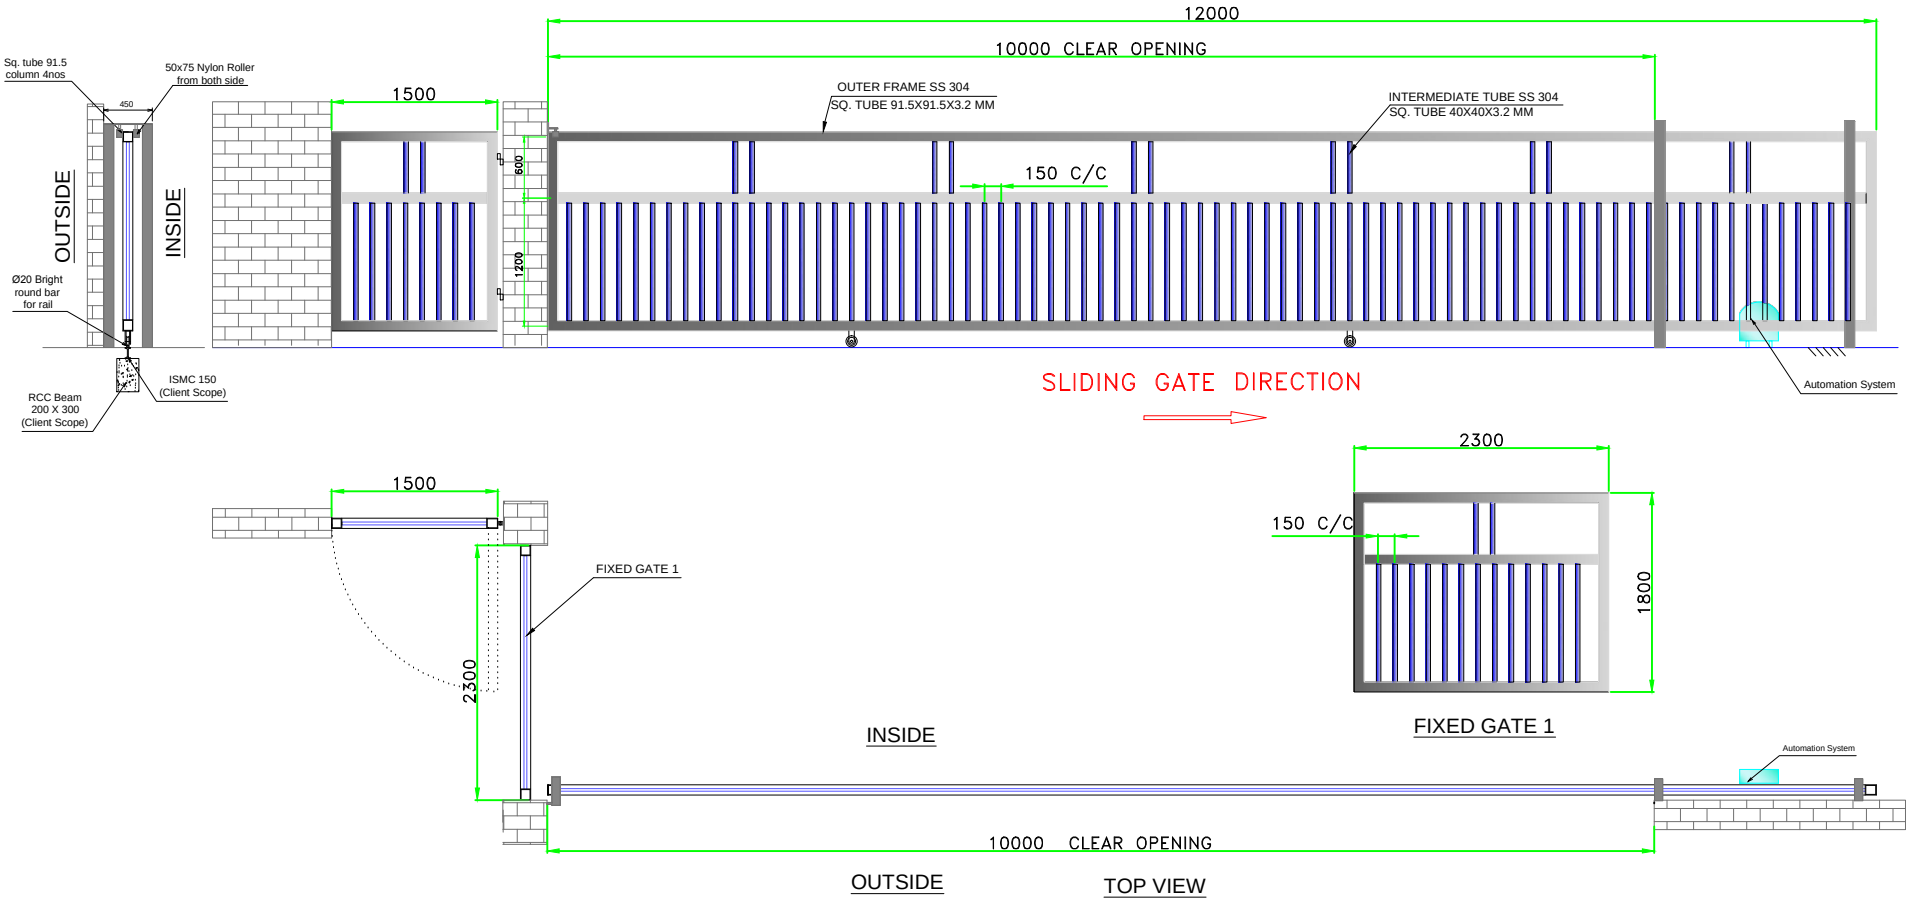



SLIDING GATE SIZE = 12000 (W) X 1800 (H), QTY = 1NOS..
SLIDING GATE WEIGHT = 1000 KG.APPROX.
CLEAR OPENING = 10,000 (W) X 1800 (H)
WICKET GATE SIZE = 1500(W) X 1800 (H), QTY = 1NOS.
WICKET GATE W.C.1 WEIGHT = 200KG.APPROX.
FIXED GATE SIZE = 2300(W) X 1800(H),
FIXED GATE OUTER FRAME = 70X70X2mm
FIXED GATE INNER FRAME = 30X30X1.6mm QTY = 1NOS.
FIXED GATE WEIGHT = 250KG.APPROX.
OUTER FRAME = 91.5 X 91.5 X 3.2 mm
INNER FRAME = 40 X 40 X 3.2 mm
GAP B/W FRAME = 150 c/c
MATERIAL = SS 304
C' COLUMN VERTICAL SUPPORT = 4 NOS.

This drawing & designing is the property of NIHVA TECHNOLOGIES. Not be sold or copy to any other concern.

| | | | |
|---|---|---|---|
| TITLE: SLIDING GATE | ALL DIMENSION ARE IN mm | | NIHVA TECHNOLOGIES PVT. LTD. |
| | SIGN | DATE | |
| CLIENT APPROVAL | DRAWN: ABHIJIT | 15/12/14 | CLIENT - JSW |
| | CHECK: ANIL | 15/12/14 | PROJECT - |
| | REV.: 05 | | SITE - KHED |
| | APPRD. | | DWG. NO. - NVA/JSW/D1/1 of 3 |
| | MFG | | SCALE: 01 \| WT: \| SHEET: 01 |
| | Ref. No. | | If any queries contact : projects@nihva.com |

NIHVA TECHNOLOGY PVT. LTD. PUNE
Tel : 020 66304033
Email:- info@nihva.com
Website:- www.nihva.com