


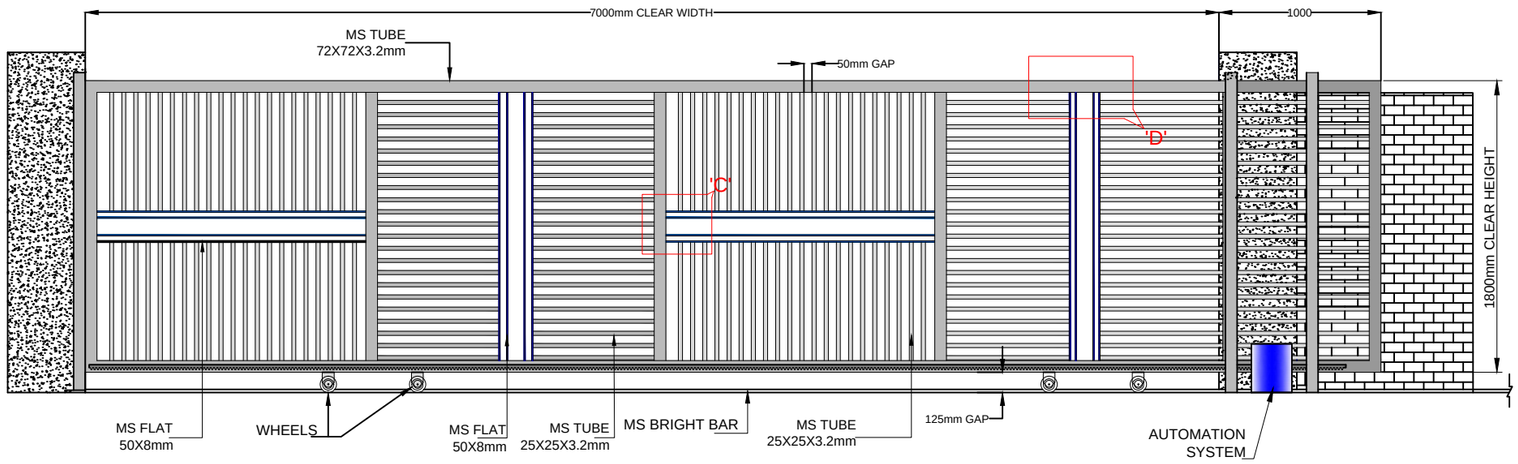


ELEVATION

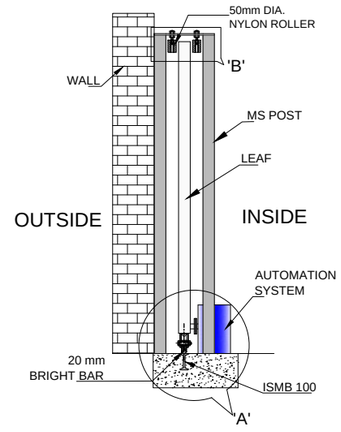


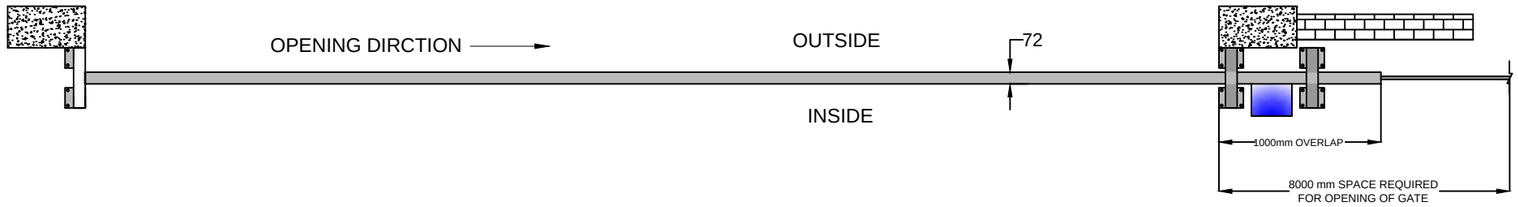


PLAN

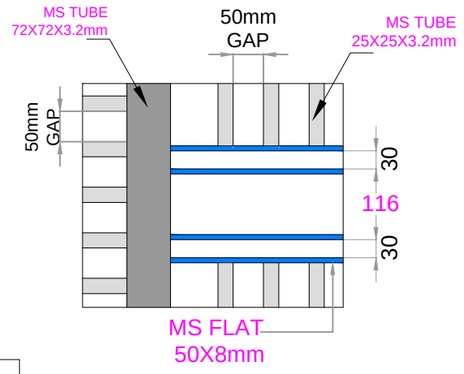


DETAIL VIEW OF 'C'.

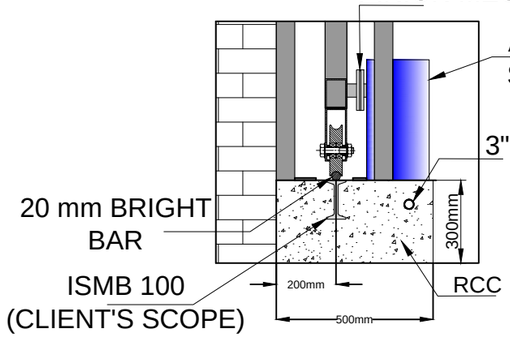

DETAIL VIEW OF 'A'.

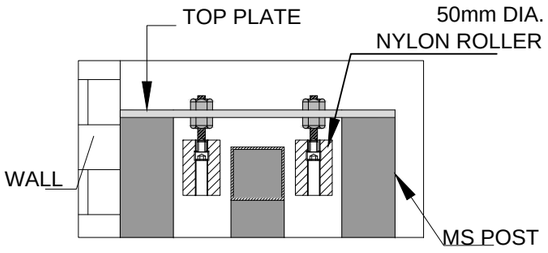

DETAIL VIEW OF 'B'.

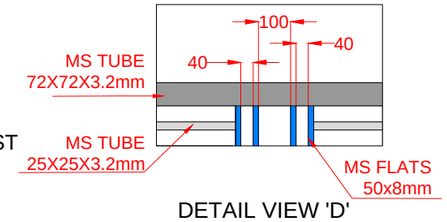

DETAIL VIEW 'D'

NOTE-
1. ALL REQUIRED CIVIL WORK WILL BE IN CLIENTS SCOPE.
2. ONE COAT OF RED OXIDE & TWO COAT OF APPROVED RAL SHADE WILL BE GIVEN TO THE GATE.

SR NO	CLEAR WIDTH	CLEAR HEIGHT	QTY.
1	7000mm	1800mm	01NOS

REV:-01.(03-04-2018)
A).DRAWING IS UPDATED AS PER PREVIOUS COMMENT

TOLERANCE - ±10mm

This drawing & design is the property of NIHVA TECHNOLOGIES. Not to be sold or copied to any other concern.

TITLE
MOTORIZED SLIDING GATE

	NAME	SIGN	DATE
DRAWN	SURAJ		28-03-2018
CHECK	OMKAR		28-03-2018
APPRD.	SHEKHAR		28-03-2018

If any queries contact : design@nihva.com

ALL DIMENSION ARE IN mm

NIHVA
NIHVA TECHNOLOGIES PVT. LTD.

NIHVA TECHNOLOGIES
PVT. LTD. PUNE
Tel : 020 66304033
Email:- info@nihva.com
Website:- www.nihva.com

CLIENT - SCON PROJECT
PROJECT - ARI ARMATUREN STEAMLINE LLP
SITE LOCATION - PUNE.
DWG. NO. : NIHVA/17-18/0399/R01. | REV- 01
SCALE: NTS | WT: | SHEET: 01 OF 01

03-04-2018 12:24:53