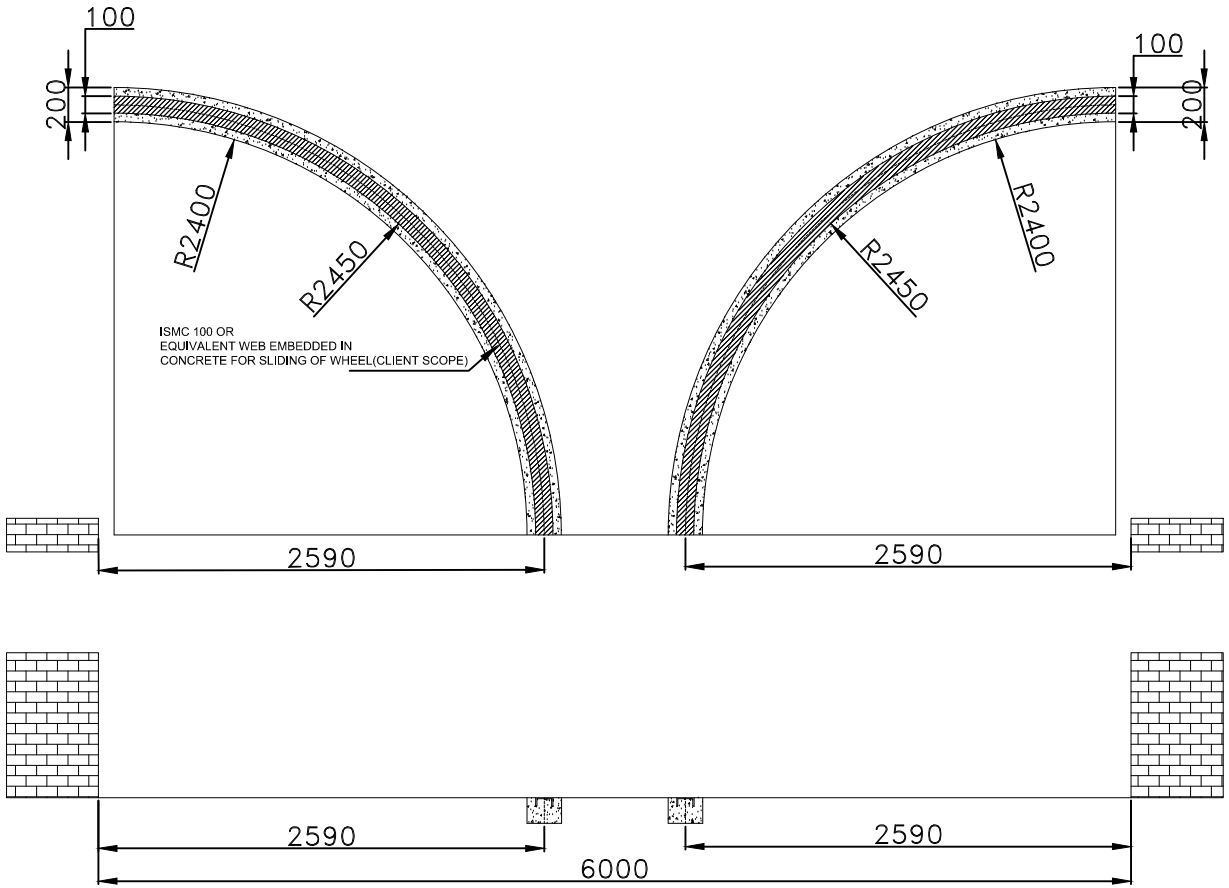


This drawing & designing is the property of NIHVA TECHNOLOGIES. Not be sold or copy to any other concern.

TITLE			
SWING GATE FOUNDATION DRAWING			
	NAME	SIGN	DATE
DRAWN	SURAJ		13.12.2018
CHECK	P.A		13.12.2018
APPROVAL	R.D		13.12.2018
If any queries contact : design@nihva.com			
ALL DIMENSION ARE IN mm			

NIHVA
NIHVA TECHNOLOGIES PVT. LTD.
NIHVA TECHNOLOGY PVT. LTD. PUNE
Tel : 020 66304033
Website:- www.nihva.com
Email:- info@nihva.com

CLIENT - INDAMER TECHNICS PVT. LTD.		
PROJECT -		
SITE - NAGPUR		
DWG. NO. : NIHVA/18-19/0204		REV. : 0
SCALE: NTS	WT:	SHEET: