



ELEVATION VIEW

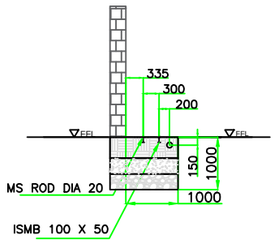

SIDE VIEW

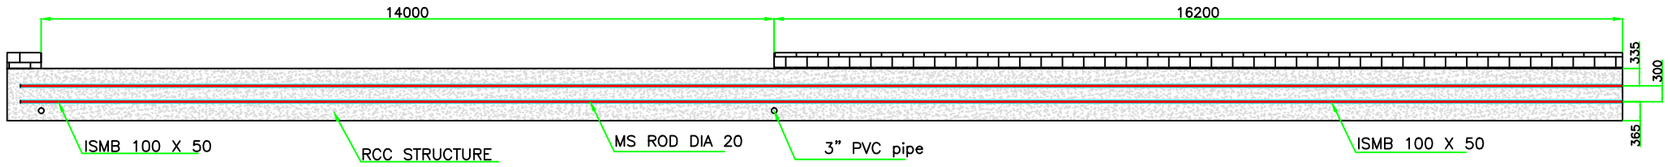

NOTE:

1. All dimensions are in mm.
2. All civil work is in client scope.
3. 3" PVC pipe should be provided for photocell wire conduit. (Client scope)
4. Power supply near motor- 3Ph, 400 V, 50 Hz (Client scope)
5. Safety: Photocell and flashlight.

This drawing & design is the property of NIHVA TECHNOLOGIES. Not to be sold or copied to any other concern.

MANUAL SLIDING GATE
14000 CW x 2400 CH

		SIGN	DATE
DRAWN	G.P.		11.03.2022
CHECK	A.K.		11.03.2022
APPRD.	V.T.		11.03.2022

If any queries contact : design@nihva.com

ALL DIMENSION ARE IN mm

NIHVA
NIHVA TECHNOLOGIES PVT. LTD.

NIHVA TECHNOLOGIES
PVT. LTD. PUNE
Tel : 020 66304033
Email:- info@nihva.com
Website:- www.nihva.com

CLIENT -SRF

LOCATION - INDORE

PRODUCT - FOUNDATION DWG

NIHVA\21-22\CLT\359 | REV- 00

SCALE: NTS | QTY: 1NOS | SHEET: 02 OF 02