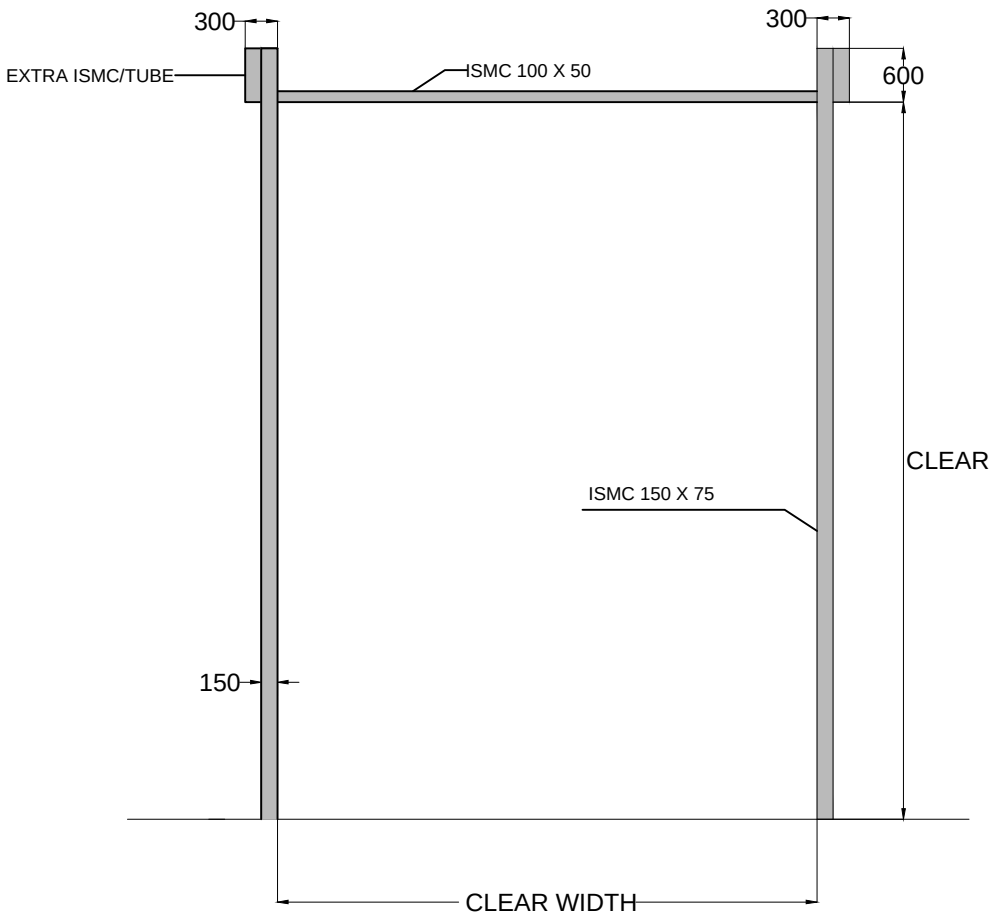


CLEAR WIDTH	CLEAR HEIGHT	QTY.
4000mm	5000mm	01NOS

TOLERANCE - ±10mm

NOTE :

1. MATERIAL FOR ALL STRUCTURE = M.S

This drawing & design is the property of NIHVA TECHNOLOGIES. Not to be sold or copied to any other concern.

TITLE
STRUCTURE FOR MOTORIZED ROLLING SHUTTER

NIHVA
NIHVA TECHNOLOGIES PVT. LTD.
NIHVA TECHNOLOGIES PVT. LTD. PUNE
Tel : 020 66304033
Email:- info@nihva.com
Website:- www.nihva.com

	NAME	SIGN	DATE
DRAWN	P.V.A		02-03-2019
CHECK	V.M.T		02-03-2019
APPRD.			

CLIENT - SYNERGY

PROJECT-EMBASSY INDUSTRIAL PARKS PVT. LTD.

SITE LOCATION - CHAKAN

If any queries contact : design@nihva.com

DWG. NO. : NIHVA/18-19/0282 REV- 00

ALL DIMENSION ARE IN mm

SCALE: NTS WT: SHEET: 01 OF 01