

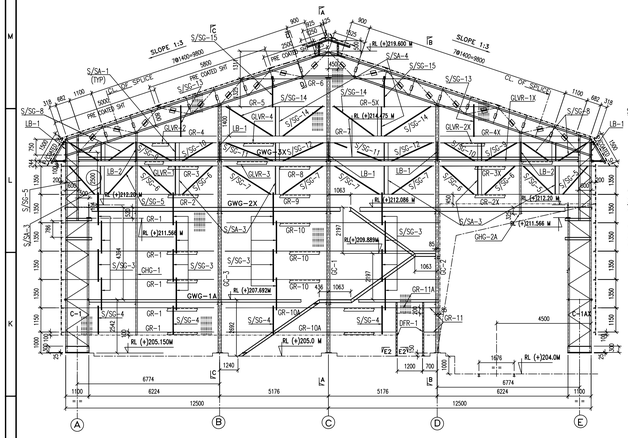



VIEW E–E
(FOR GABLE END ON LINE 1)

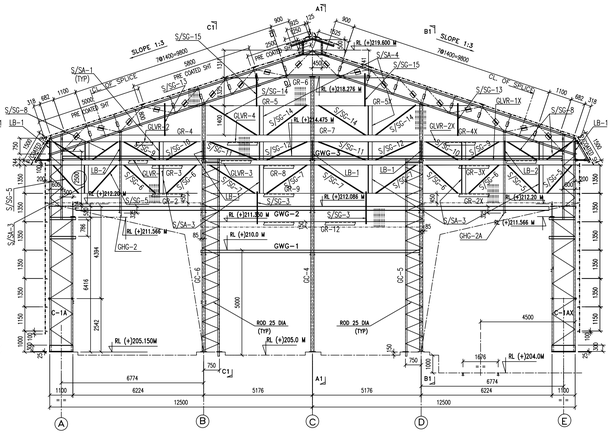


VIEW E–E
(FOR GABLE END ON LINE 53)

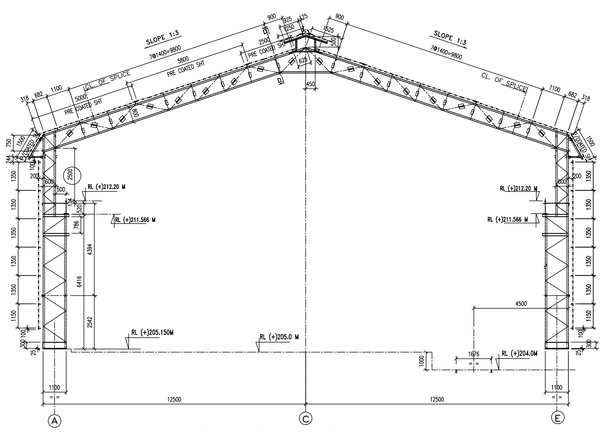

SECTION THROUGH INTERMEDIATE COLUMNS

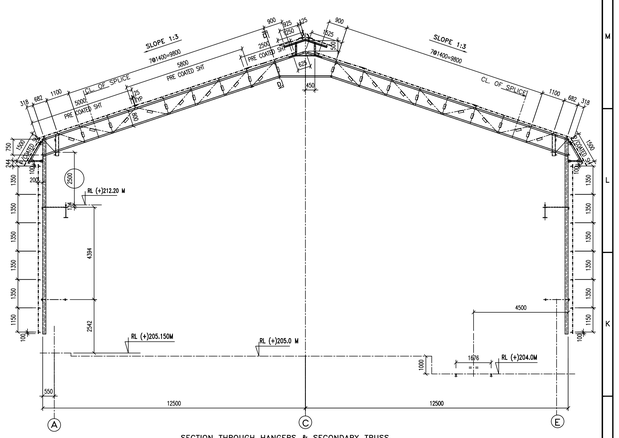


SECTION THROUGH HANGERS & SECONDARY TRUSS.

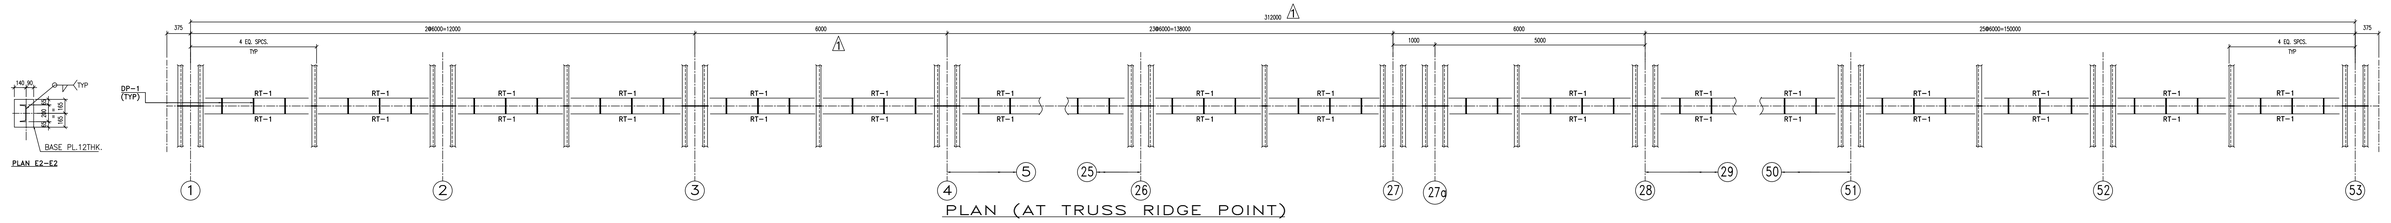


PLAN E2–E2


PLAN (AT TRUSS RIDGE POINT)

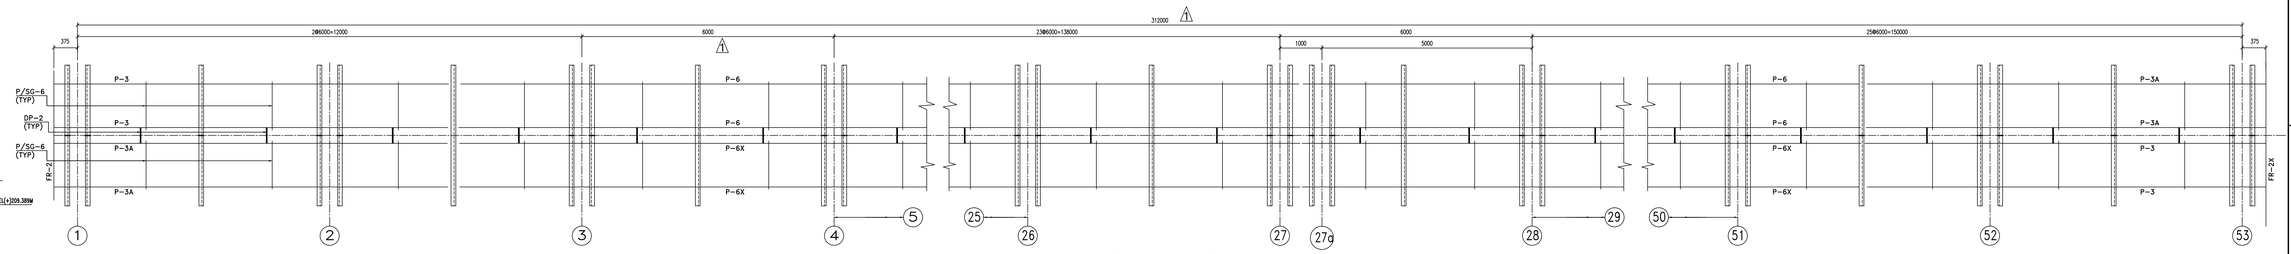


PLAN (AT MONITOR LEVEL)

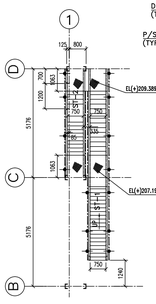

DETAIL 'X'

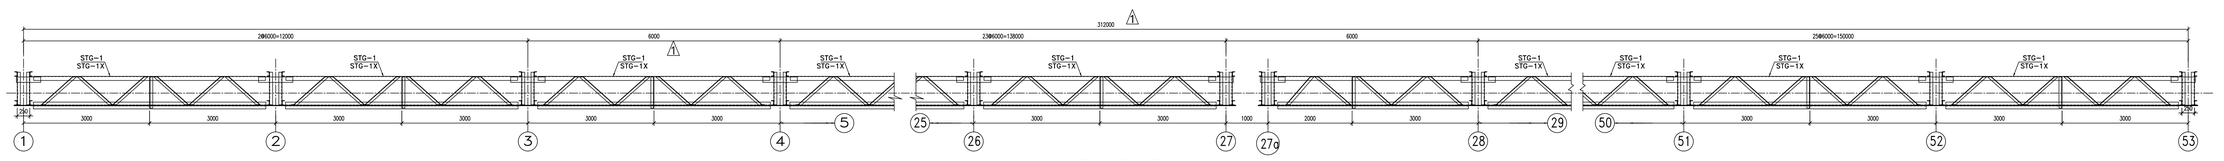

VIEW D–D

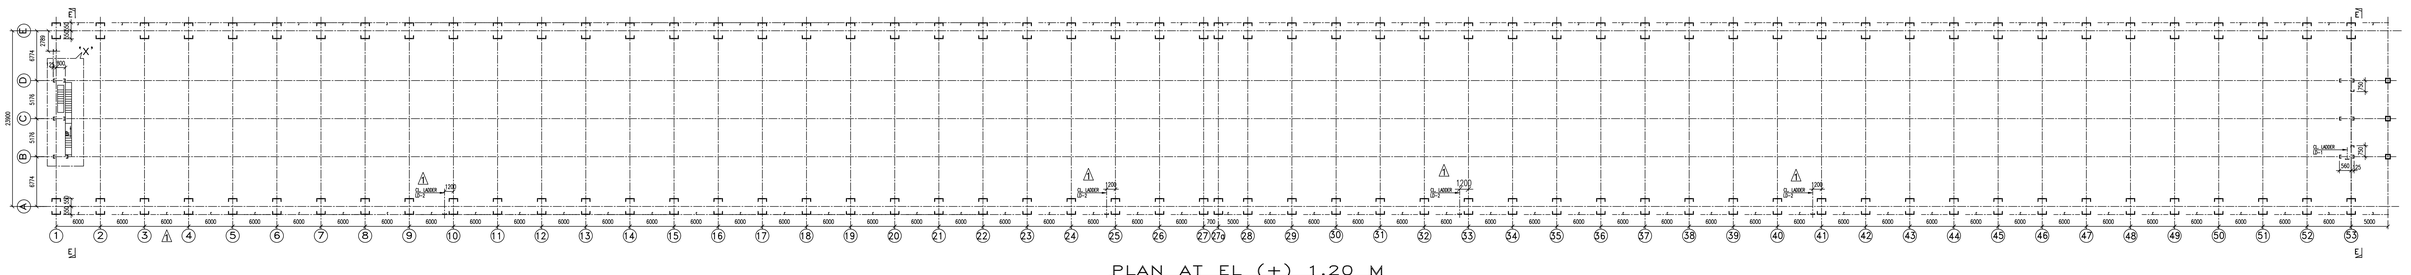

PLAN AT EL (+) 1.20 M
1:200

NOTES:–

1. ALL DIMENSIONS ARE IN mm. & LEVELS ARE IN METER.
2. THIS DRG. IS TO BE READ IN CONJUNCTION WITH DRG. NO. 1–B014–404–05–001,003 & 002_SHT2.

SHEETING ARRGT. SHOWN HERE ARE INDICATIVE FOR EXTENT & TYPE ONLY. INDIVISUAL SHEET SIZES TO BE FINALISED DURING SHEETING DETAILING.
FOR SIDE & GABLES TRANSLUCENT SHEETS AFTER EVERY 5 PRECOATED SHEETS WILL BE PROVIDED IN SAME VERTICAL PLANE.

REV	REVISION DETAILS	NO.OF REV. MARKS	DRAWN	CHECKED	MECH.	PRO.&UTIL.	RLEC.	INST.	CIVIL	STRL.	APPROVED	DATE
6												
5												
4												
3												
2												
1	REVISED AS PER OUTOTEC COMMENTS DT. 20.08.08 & MKD		D.BERA	AL.							AM.	21.08.08

REVIEWED

SL.NO.	DRG. PRPD. BY	DESCRIPTION	DRAWING NO.	SHT	REV
6					
5					
4					
3					
2					
1					

REFERENCE DRAWINGS

DATE		01.07.08	02.07.08	04.07.08						04.07.08	04.07.08
SIGN.											
NAME		D BERA	N.K	S.D						AL	A.M
	DESIGNED	DRAWN	CHECKED	MECH.	PRO.&UTIL.	RLEC.	INST.	CIVIL	STRL.	APPROVED	

REVIEWED

1. DO NOT SCALE, IF ANY DOUBT PLEASE ASK.
2. REVISION MARKS ARE INSCRIBED IN △

THIS DRAWING IS MBE'S PROPERTY AND MUST NOT BE USED EXCEPT IN CONNECTION WITH MBE'S WORK. REPRODUCTION, USE OR DISCLOSURE OF THE CONTENTS OF THIS DRAWING TO THIRD PARTY/IES WITHOUT EXPRESS / WRITTEN PERMISSION OF MBE IS STRICTLY PROHIBITED.

CLIENT	VEDANTA ALUMINA LTD JHARSUGUDA, INDIA
PROJECT	THREE UNITS OF GREEN ANODE PLANT
TITLE	PETCOKE STORAGE SHED CROSS SEC. & MARKING OF GABLE END,TRUSS RIDGE & MONITOR LVL

mbe PROJECTS DIVISION — McNally Bharat ENGINEERING COMPANY LIMITED, 4, MANGOE LANE, KOLKATA, INDIA

SCALE	MBE DRAWING NUMBER	SHT NO.	REV.
1 : 20	1-B014-404-05-002	1 OF 2	1

MBE PROPOSAL/SO NO. 08901

SHT–A0

STF–C–001 (REV–1) 01–10.0.2001

DXF FILE : 1–B014–404–05–002_SHT1–R1