


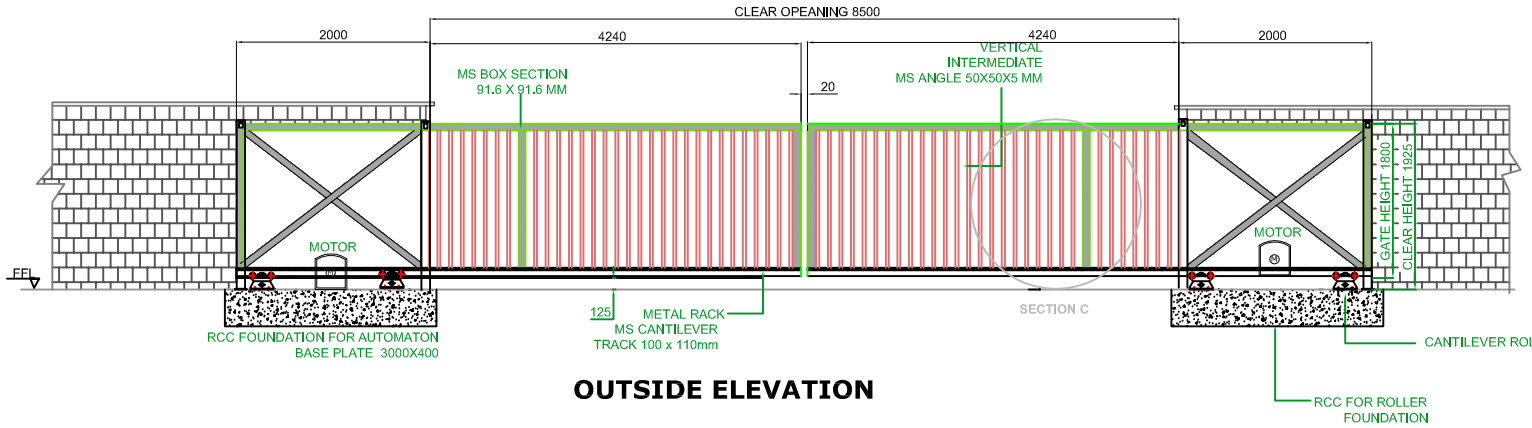


OUTSIDE ELEVATION

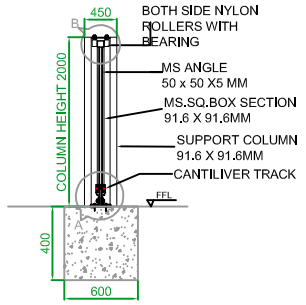


SIDEVIEW

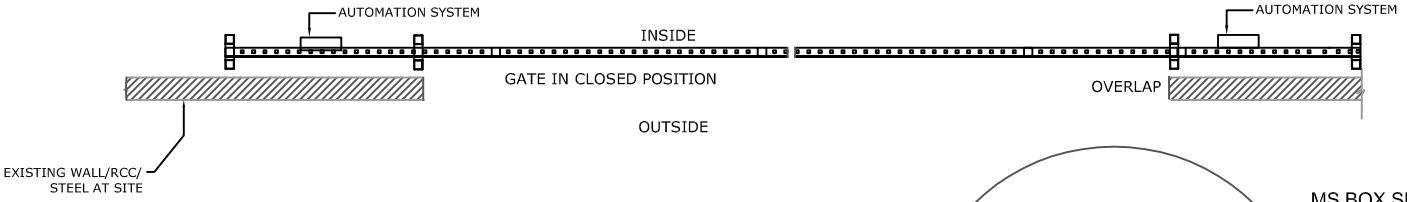


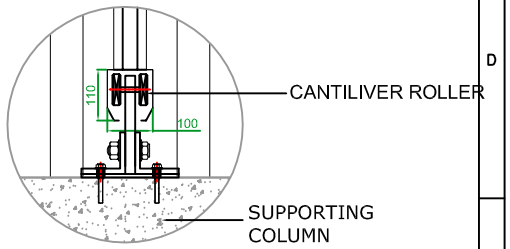


DETAILS OF A

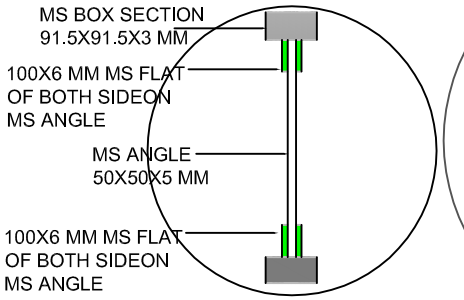

SIDE VIEW OF SECTION C

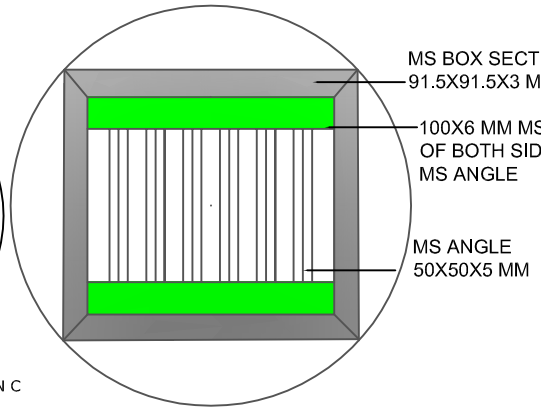

DETAILS OF C

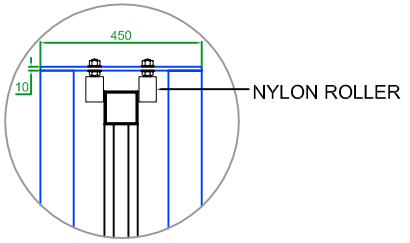

DETAILS OF B

SIZE OF GATE BIPARTING :- 8.5M(W) X 1.8M(H)

QTY:- 1 NOS

TITLE: CANTILEVER SLIDING GATE -BIPARTING		SIGN	DATE
CLIENTS APPROVEL:–	DRAWN		
	CHECK		
	ENG		
	APPRD.		
ALL DIMENSION ARE IN M.M.	PROD		
If any queries CONTACT: projects@nihva.com	MFG		
	Ref. No.		

NIHVA TECHNOLOGIES PVT. LTD.

NIHVA TECHNOLOGY PVT. LTD. PUNE
Tel : 020 66304033
Email:- info@nihva.com
Website:- www.nihva.com

CLIENT:
PROJECT :
SITE :
PRODUCT NAME:
DWG. NO.:
SCALE: WT: SHEET: 1 OF 1

NIHAV