
BOOM BARRIER LAYOUT WITH WIRING DIAGRAM


NOTE :
All wires and electrical conduit/tray should be co-ordinated with electrical vendor


TECHNICAL DETAILS - QIK 7EH	
POWER SUPPLY	230V AC - 50/60 Hz
OPENING TIME	2÷6 s/90°
CURRENT	1 A
DEGREE OF PROTECTION	IP 24D
CONTROL PANEL	73RQ
MOTOR DIMENSIONS	300(W) x 320(D) x 1050(H)

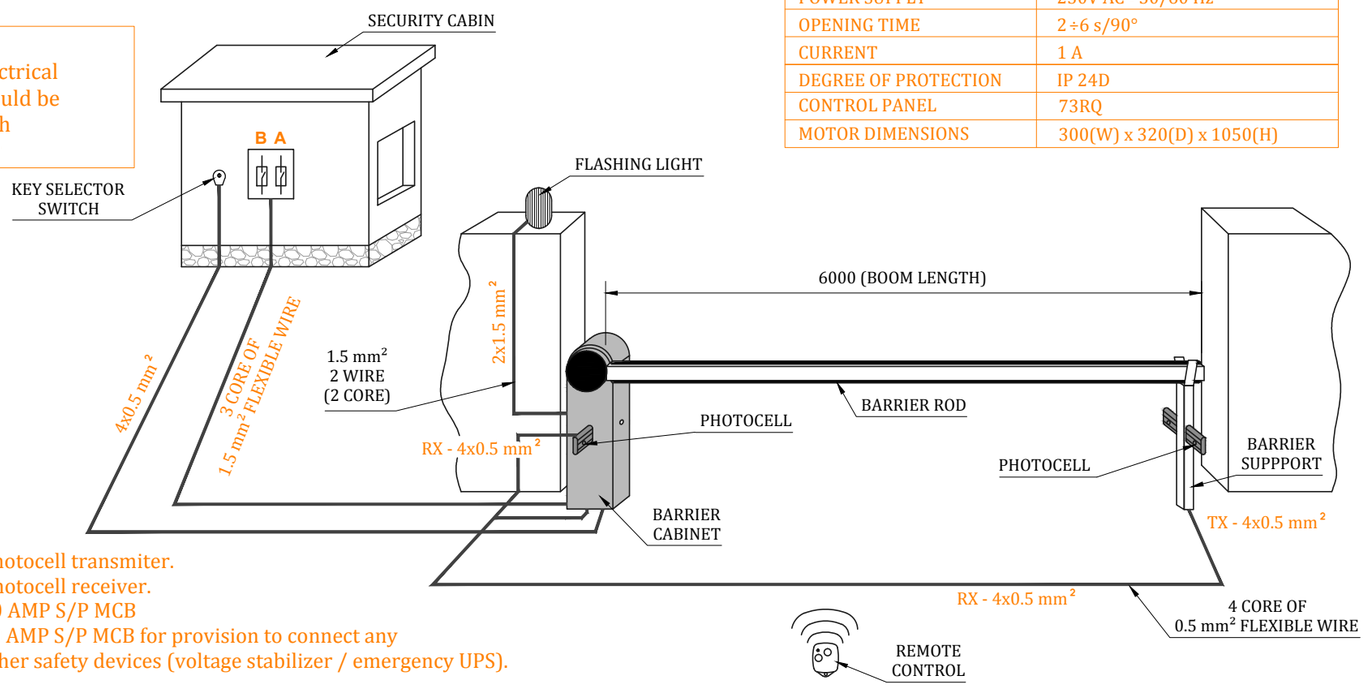

TX : Photocell transmiter.
RX : Photocell receiver.
A : 10 AMP S/P MCB
B : 10 AMP S/P MCB for provision to connect any other safety devices (voltage stabilizer / emergency UPS).

BOOM BARRIER FOUNDATION

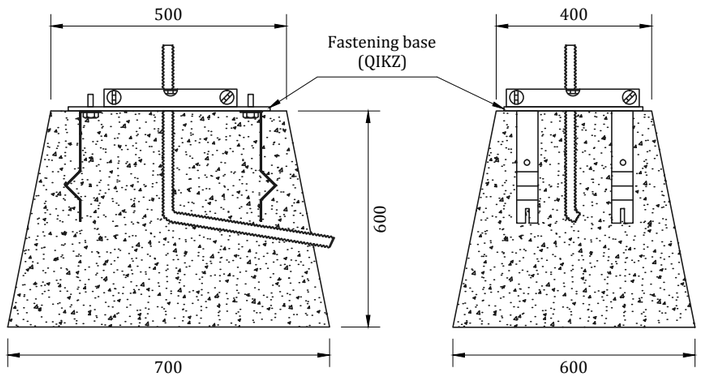

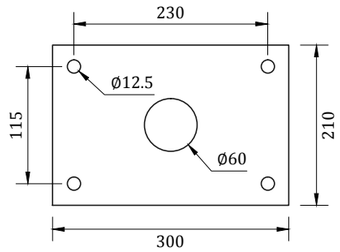


(QIKZ)

* If the flooring does not permit a firm, stable fastening, prepare a cemented area with the anchoring clamps and the base plate (QIKZ) englobed in the cement. The base must be level and clean.
* Insert pieces of iron (or another material) in the holes of the anchoring clamps, to hook the clamps, to hook the clamps to the cement reinforcement.
* Pass the cable guard trunking through the central hole of the plate.

Attention : checking the robustness and stability of the fastening.

KEY PLAN :-

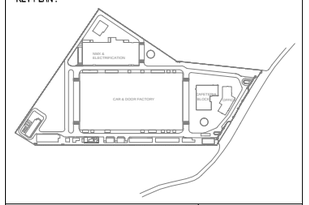

N

GENERAL NOTES :
- ALL DIMENSIONS ARE IN MILLIMETRES AND ARE UNFINISHED DIMENSIONS UNLESS OTHERWISE SPECIFIED.
- ALL LEVELS ARE IN METRES AND ARE UNFINISHED LEVELS UNLESS OTHERWISE SPECIFIED.
- DO NOT SCALE DRAWINGS. ONLY WRITTEN DIMENSIONS SHALL BE FOLLOWED. ANY DISCREPANCIES NOTED SHALL BE BROUGHT TO THE NOTICE OF THE ARCHITECT PRIOR TO EXECUTION.

REV.	DESCRIPTION	DATE	BY	CHD.
T2	ISSUED FOR TENDER	02.03.17	SV	VA
T1a	ISSUED FOR CLIENT REVIEW	24.11.16	SV	VA
T1	ISSUED FOR TENDER	01.04.15	MB	VA

AMENDMENT

GRAPHIC SCALE: 0 1M 4M 6M / 1M 0 2M 6M 10M

CLIENT:
KONE ELEVATOR INDIA PVT. LTD.

PROJECT:
PROPOSED KONE ELEVATOR FACTORY AT PILLAIPAKKAM, NEAR CHENNAI.

DRAWING TITLE:
STANDARD DETAILS - 04
BOOM BARRIER DETAIL TYPE - 01

SCALE : AS SHOWN	DRAWN : V.A.	REV
DATE : 18.02.2015	CHKD : V.R.	
DRAWING NO: KEIPL-P-FAC-AR20-04-01-189948		T2

ARCHITECTURE • INTERIOR DESIGN • ENGINEERING • PLANNING • CONSTRUCTION MANAGEMENT
C R NARAYANA RAO
10, KARPAGAMBAL NAGAR, MYLAPORE, CHENNAI-600 004
B.Arch. (Hons.), M.Arch., (Calif.), F.I.I.A., IntlAssoc.A.I.A., Registered Architect.