


DRAWING

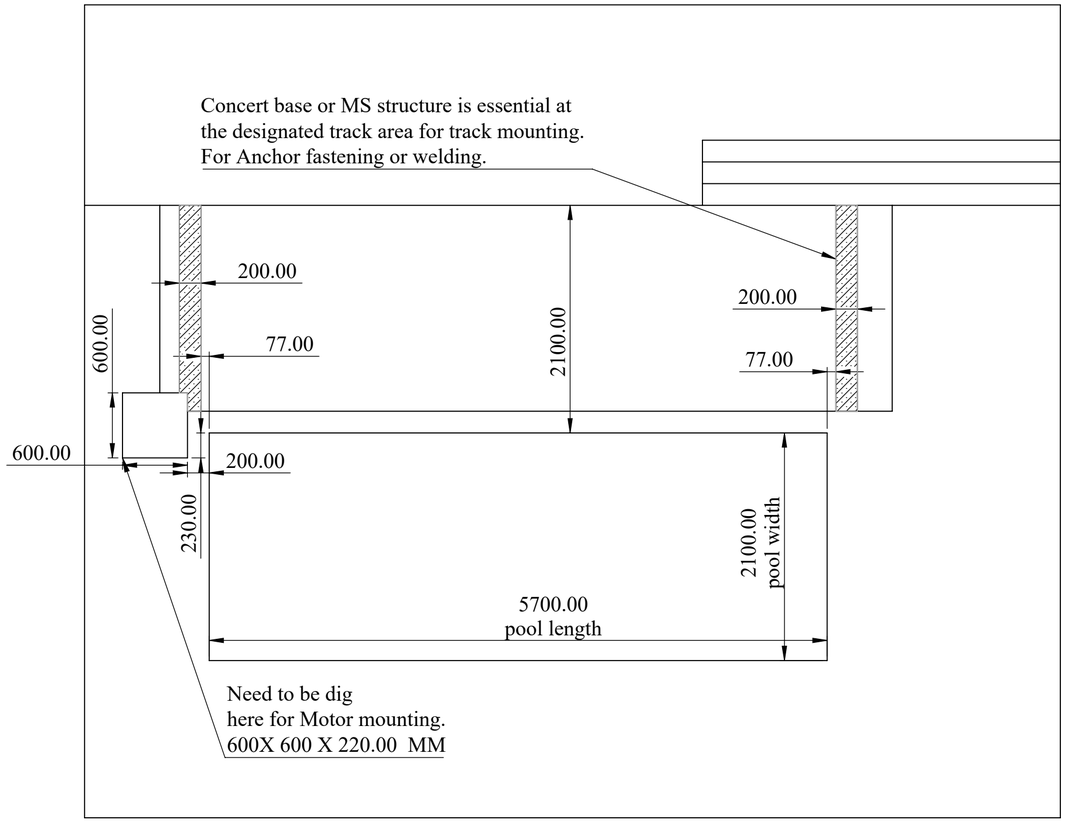


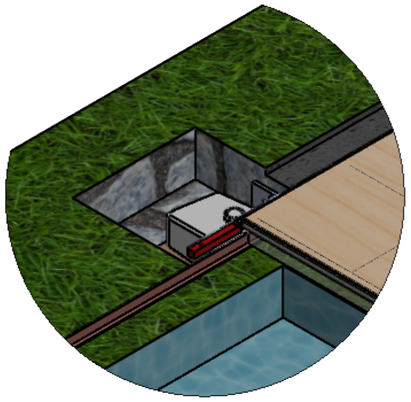

DETAIL G
SCALE 1 : 15

MOTOR ARRANGEMENT

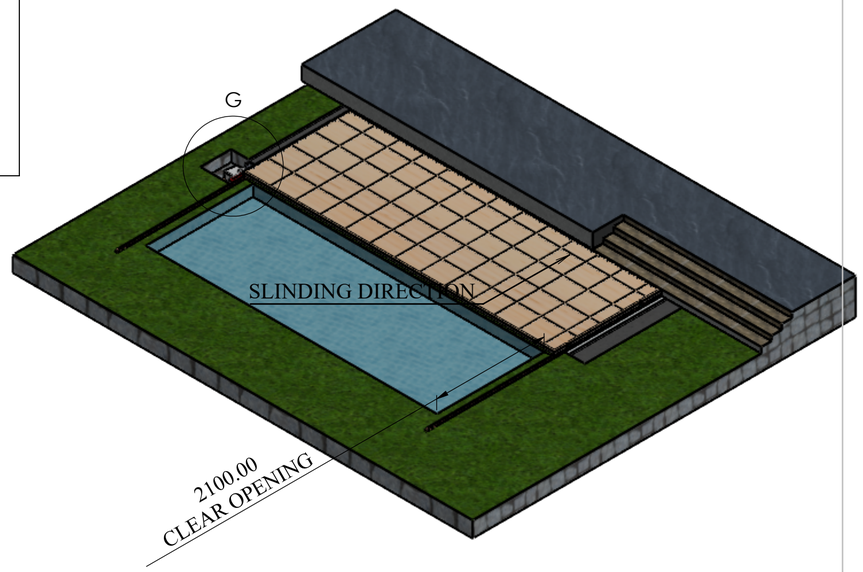


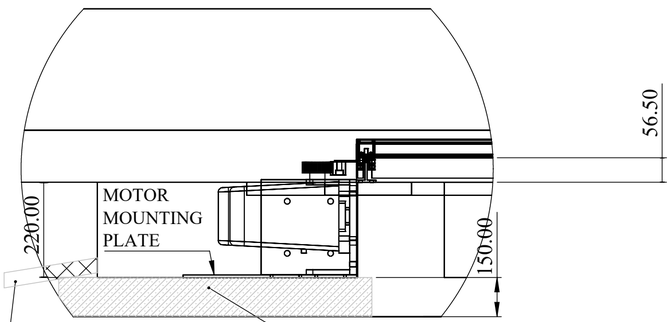

DETAIL K
SCALE 1 : 10

Drainage hole
req for water
remove 1-2 INCH pipe

Concete base req
for anchor fastening of Motor.
Height150 MM

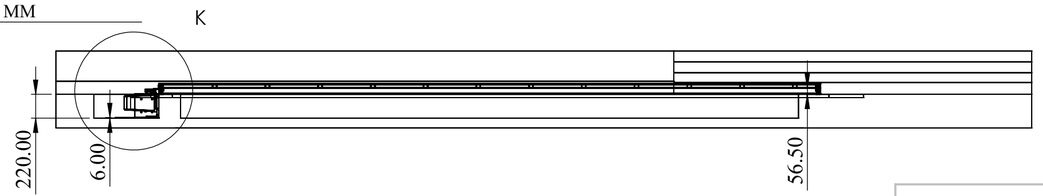

REV DESCRIPTION	DATE	REV NO
	29-07-2025	REV 00
1.		

NOTE :

All civil work is under the end client scope.

SPECIAL INSTRUCTION'S :

TITLE - SWIMMING POOL ENCLOSER			
DWG NO - NTPL-000-PM-001-00-00-00			
NIHVA Technologies Pvt. Ltd.	NIHVA TECHNOLOGIES PVT.LTD.PUNE Website - www.nihva.com		
	NAME	SIGNATURE	DATE
DRAWN	V.W.		29-07-2025
CHK'D	P.M.		30-07-2025
APPV'D	V.T.		30-07-2025
If any queries contact - design.nihva@gmail.com			
ALL DIMENSION ARE IN mm		A2	
PRODUCT - SWIMMING POOL DECK			
PROJECT NO - NTPL-000-PM		REVISION - 00	
SITE LOCATION -		WEIGHT -	
MATRIAL -		QTY - 1	
PROJECTION METHOD:		SCALE :	
		SHEET 2 OF 2	