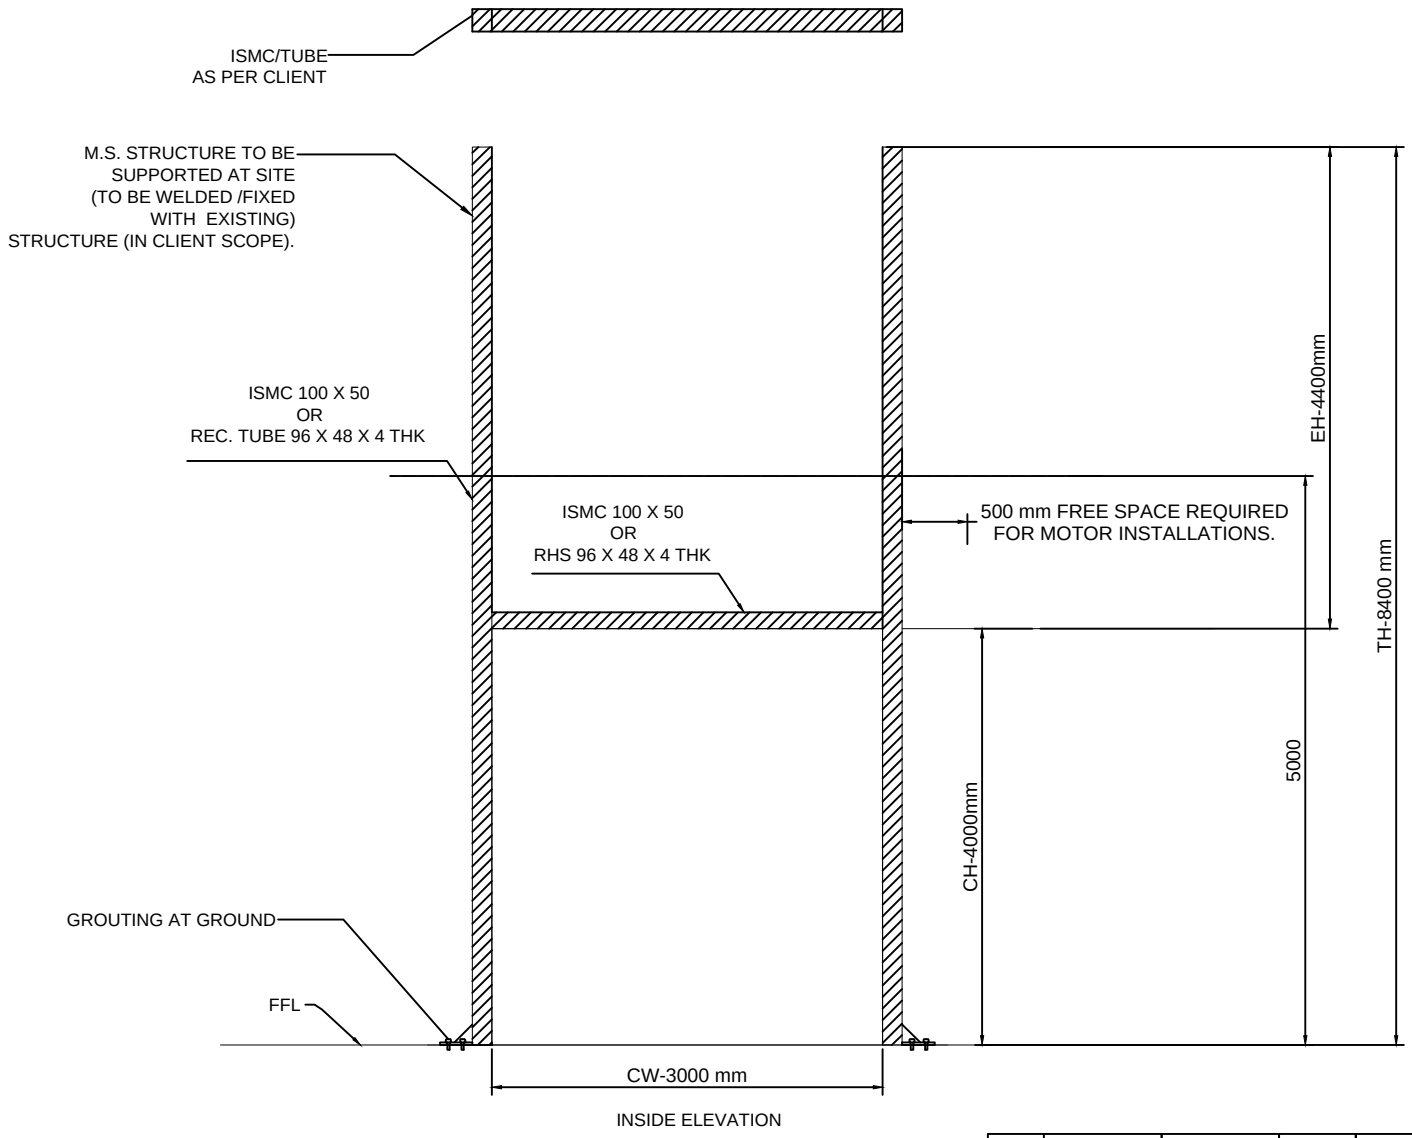

INSIDE ELEVATION

SR NO	CLEAR WIDTH CW	CLEAR HEIGHT CH	QTY	TH	EH
1	3000 mm	4000mm	10	8400	4400

This drawing & design is the property of NIHVA TECHNOLOGIES. Not to be sold or copied to any other concern.

TITLE: STRUCTURE FOR SECTIONAL DOOR

NIHVA TECHNOLOGIES PVT. LTD. PUNE
Tel : 020 66304033
Email:- info@nihva.com
Website:- www.nihva.com

	NAME	SIGN	DATE
DRAWN	S.M.S.		8.7.2021
CHECK	V.J.		8.7.2021
REV.			
APPROVAL			

If any queries contact : projectsupport@nihva.com

ALL DIMENSION ARE IN mm

CLIENT - JEENALI TRADING

PROJECT -

SITE LOCATION - WADHA

DWG. NO. : NIHVA/21-22/039/SDSTRUCT

SCALE: NTS | WT: | SHEET: 01 OF 01

NOTES-
(1) REQUIRED M.S. STRUCTURE , FITTING & ALL CIVIL WORK IN CLIENT SCOPE .
(2) PRODUCT WILL BE INSTALLED AFTER READINESS OF STRUCTURE AS PER DRAWING.