
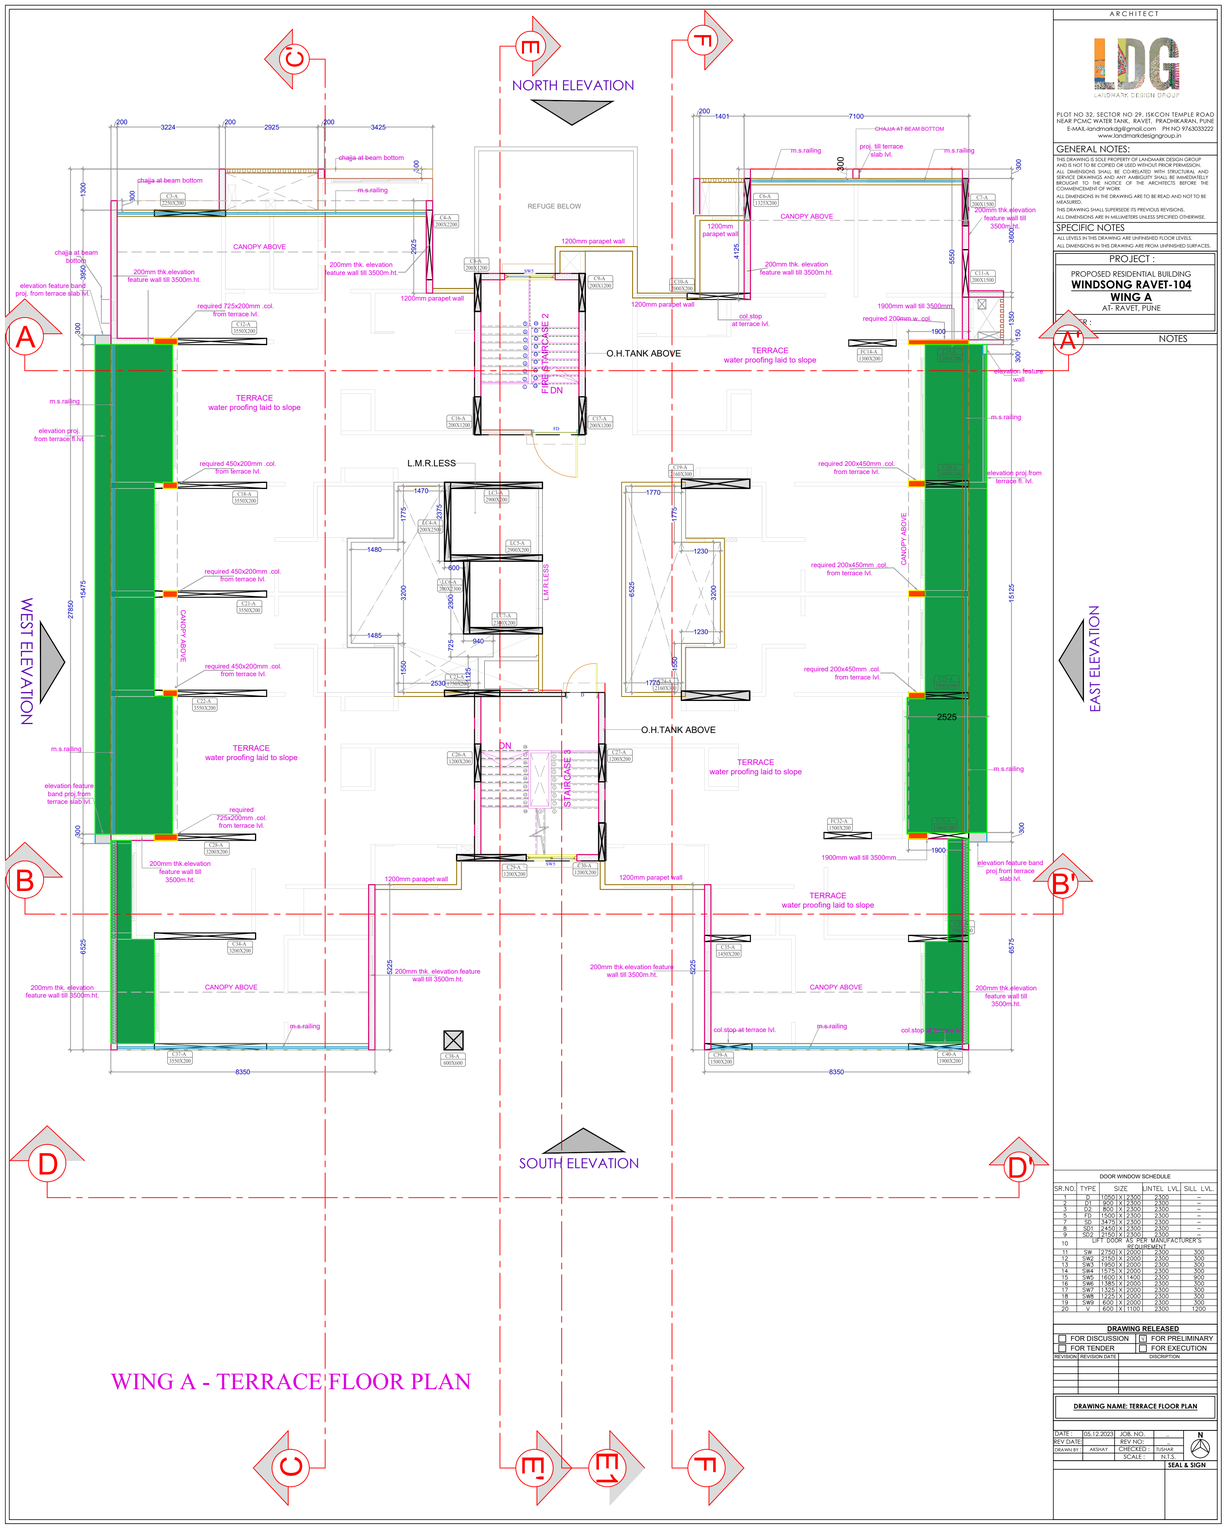


WING A - TERRACE FLOOR PLAN

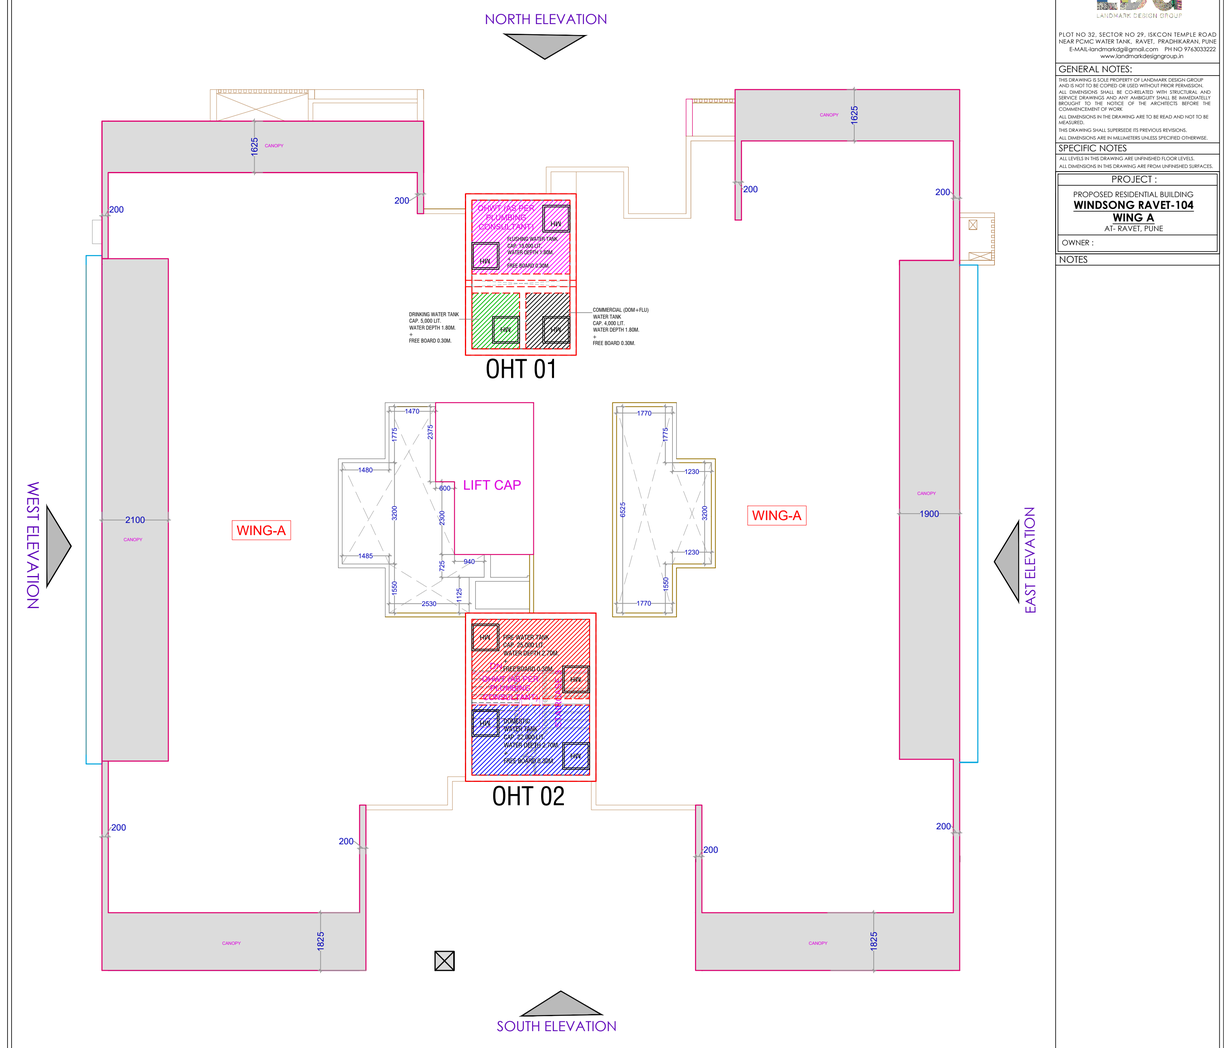

WING A - OHWT LEVEL FLOOR PLAN

ARCHITECT
LDG
LANDMARK DESIGN GROUP
PLOT NO 32, SECTOR NO 29, ISKCON TEMPLE ROAD NEAR PCMC WATER TANK, RAVET, PRADHIKARAN, PUNE
E-MAIL-landmarkdg@gmail.com PH NO 9763033222
www.landmarkdesigngroup.in

GENERAL NOTES:

THIS DRAWING IS SOLE PROPERTY OF LANDMARK DESIGN GROUP AND IS NOT TO BE COPIED OR USED WITHOUT PRIOR PERMISSION.

ALL DIMENSIONS, SHALL BE CO-RELATED WITH STRUCTURAL AND SERVICE DRAWINGS AND ANY AMBIGUITY SHALL BE IMMEDIATELY BROUGHT TO THE NOTICE OF THE ARCHITECTS BEFORE THE COMMENCEMENT OF WORK.

ALL DIMENSIONS IN THE DRAWING ARE TO BE READ AND NOT TO BE MEASURED.

THIS DRAWING SHALL SUPERSEDE ITS PREVIOUS REVISIONS.

ALL DIMENSIONS ARE IN MILLIMETERS UNLESS SPECIFIED OTHERWISE.

SPECIFIC NOTES

ALL LEVELS IN THIS DRAWING ARE UNFINISHED FLOOR LEVELS.

ALL DIMENSIONS IN THIS DRAWING ARE FROM UNFINISHED SURFACES.

PROJECT :

PROPOSED RESIDENTIAL BUILDING

WINDSONG RAVET-104

WING A

AT- RAVET, PUNE

OWNER :

NOTES

DOOR WINDOW SCHEDULE

SR.NO.	TYPE	SIZE	LINTEL LVL	SILL LVL
1	D	1000 X 2100	2300	–
2	D1	800 X 2100	2300	–
3	D2	900 X 2100	2300	–
4	FD	1500 X 2300	2300	–
5	UD	1475 X 2300	2300	–
6	SD	2450 X 2300	2300	–
7	SD2	2150 X 2300	2300	–
10	UPT DOOR AS PER MANUFACTURER'S REQUIREMENT			
11	SW	2750 X 2000	2300	300
12	SW2	2150 X 2000	2300	300
13	SW3	1975 X 2000	2300	300
14	SW4	1875 X 2000	2300	300
15	SW5	1650 X 1400	2300	300
16	SW6	1385 X 2000	2300	300
17	SW7	1325 X 2000	2300	300
18	SW8	1225 X 2000	2300	300
19	SW9	600 X 1200	2300	300
20	V	600 X 1100	2300	1200

DRAWING RELEASED

- ☐ FOR DISCUSSION
- ☐ FOR PRELIMINARY
- ☐ FOR TENDER
- ☐ FOR EXECUTION

REVISION	REVISION DATE	DISCRIPTION

DRAWING NAME: TERRACE FLOOR PLAN

DATE : 05.12.2023 JOB. NO.

REV DATE : REV NO:

DRAWN BY : AKSHAY CHECKED : TUSHAR

SCALE : N.T.S.

SEAL & SIGN

ARCHITECT
LDG
LANDMARK DESIGN GROUP
PLOT NO 32, SECTOR NO 29, ISKCON TEMPLE ROAD NEAR PCMC WATER TANK, RAVET, PRADHIKARAN, PUNE
E-MAIL-landmarkdg@gmail.com PH NO 9763033222
www.landmarkdesigngroup.in
GENERAL NOTES:
THIS DRAWING IS SOLE PROPERTY OF LANDMARK DESIGN GROUP AND IS NOT TO BE COPIED OR USED WITHOUT PRIOR PERMISSION.
ALL DIMENSIONS, SHALL BE CO-RELATED WITH STRUCTURAL AND SERVICE DRAWINGS AND ANY AMBIGUITY SHALL BE IMMEDIATELY BROUGHT TO THE NOTICE OF THE ARCHITECTS BEFORE THE COMMENCEMENT OF WORK.
ALL DIMENSIONS IN THE DRAWING ARE TO BE READ AND NOT TO BE MEASURED.
THIS DRAWING SHALL SUPERSEDE ITS PREVIOUS REVISIONS.
ALL DIMENSIONS ARE IN MILLIMETERS UNLESS SPECIFIED OTHERWISE.
SPECIFIC NOTES
ALL LEVELS IN THIS DRAWING ARE UNFINISHED FLOOR LEVELS.
ALL DIMENSIONS IN THIS DRAWING ARE FROM UNFINISHED SURFACES.
PROJECT :
PROPOSED RESIDENTIAL BUILDING
WINDSONG RAVET-104
WING A
AT- RAVET, PUNE
OWNER :
NOTES

DISCRIPTION

DRAWING RELEASED

- ☐ FOR DISCUSSION
- ☐ FOR PRELIMINARY
- ☐ FOR TENDER
- ☐ FOR EXECUTION

REVISION	REVISION DATE	DISCRIPTION

DRAWING NAME: OHWT LEVEL FLOOR PLAN

DATE : 05.12.2023 JOB. NO.

REV DATE : REV NO:

DRAWN BY : AKSHAY CHECKED : TUSHAR

SCALE : N.T.S.

SEAL & SIGN