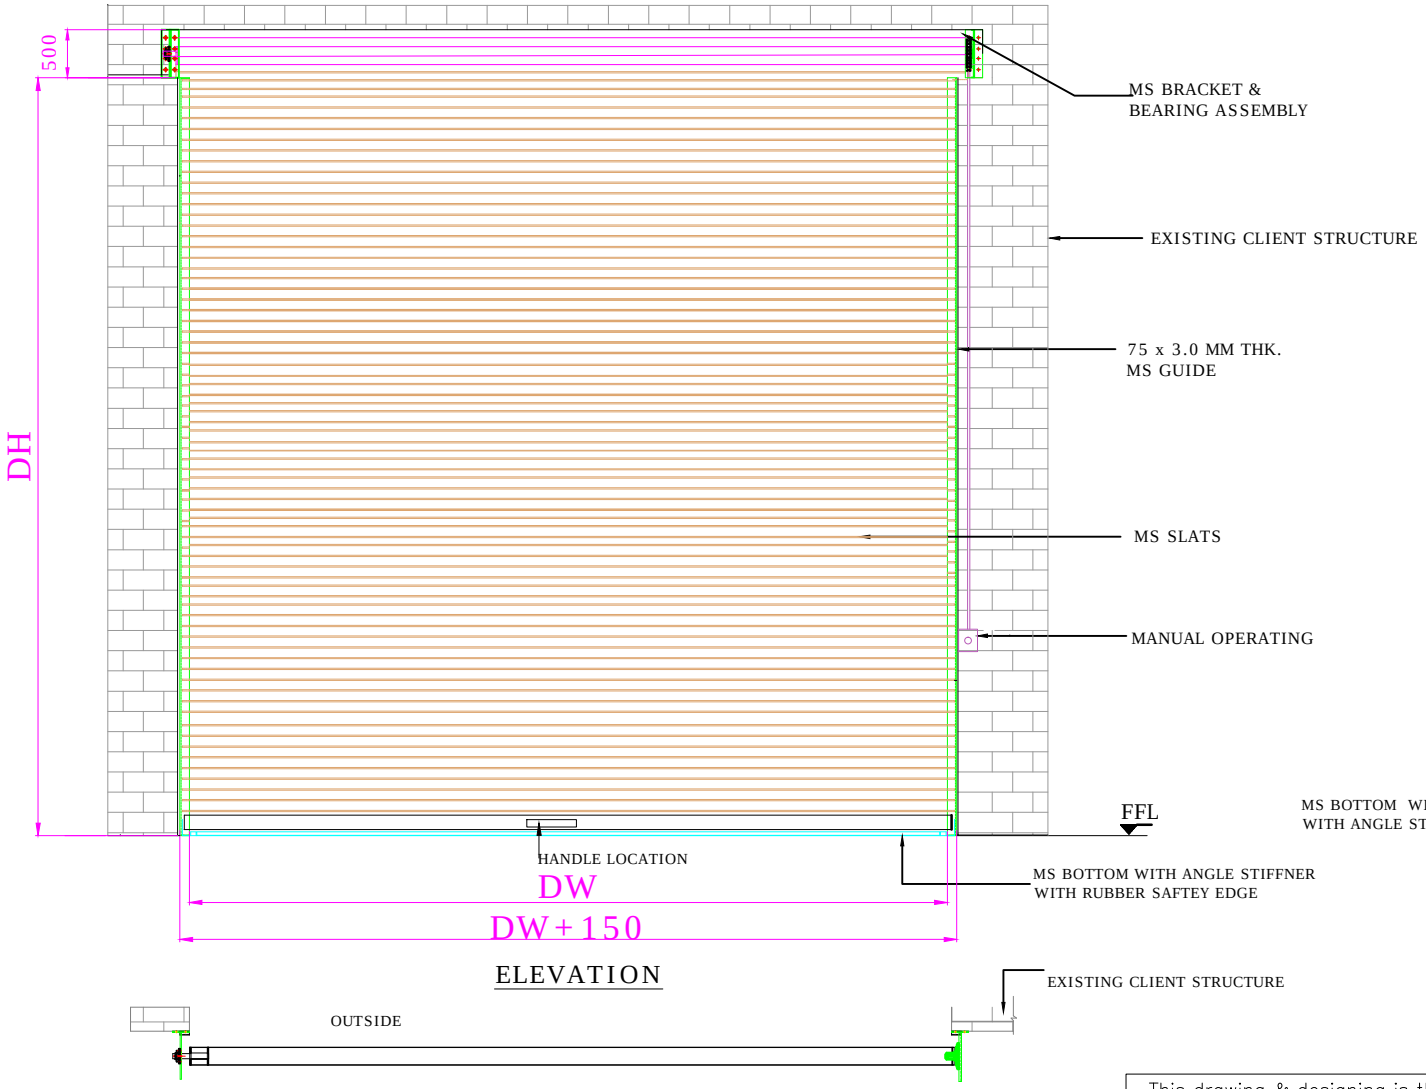
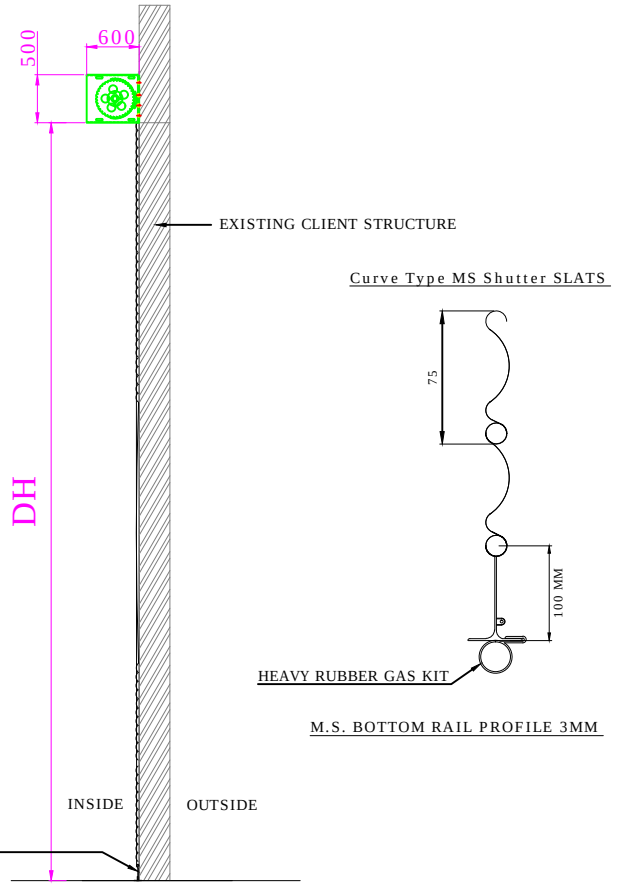


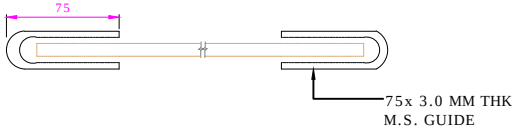

ELEVATION




PLAN




SIDE VIEW




| Sr.No. | DOOR WIDTH | DOOR HEIGHT | QUANTITY |
|---|---|---|---|
| 1} | 2451 mm | 3033 mm | 11 |
| 2} | 3000 mm | 3033 mm | 2 |

COLOR-(RAL-7001-GREY COLOR)

This drawing & designing is the property of NIHVA TECHNOLOGIES. Not be sold or copy to any other concern.

TITLE

GEAR OPERATED
ROLLING SHUTTER

CLIENT APPROVAL

ALL DIMENSION ARE IN mm

| | NAME | DATE | SIGN. |
|---|---|---|---|
| DRAWN | ABHIJIT | 12/01/16 | |
| CHECK | ANIL | | |
| REV. | 00 | | |
| APPRD. | | | |
| MFG | | | |
| Ref. No. | | | |

NIHVA TECHNOLOGIES PVT. LTD.

NIHVA TECHNOLOGY
PVT. LTD. PUNE
Tel : 020 66304033
Email:- info@nihva.com
Website:- www.nihva.com

CLIENT : INDOSPACE

PROJECT : APM BUILDING

SITE : CHAKAN-PUNE

DWG. NO.: NIHVA/15-16/163

SCALE: 01 | WT: | SHEET: 01 OF 01

If any queries contact : projects@nihva.com