


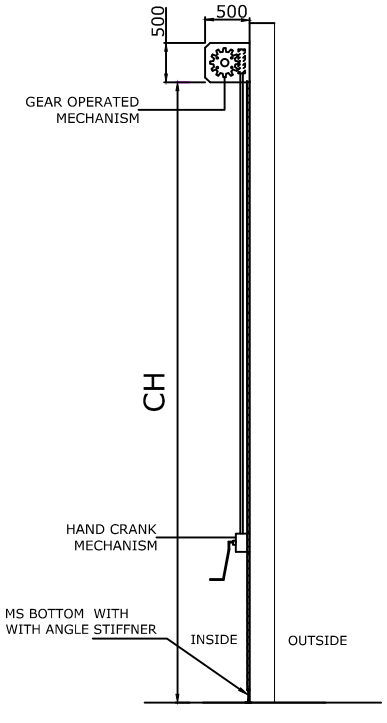


SIDE VIEW

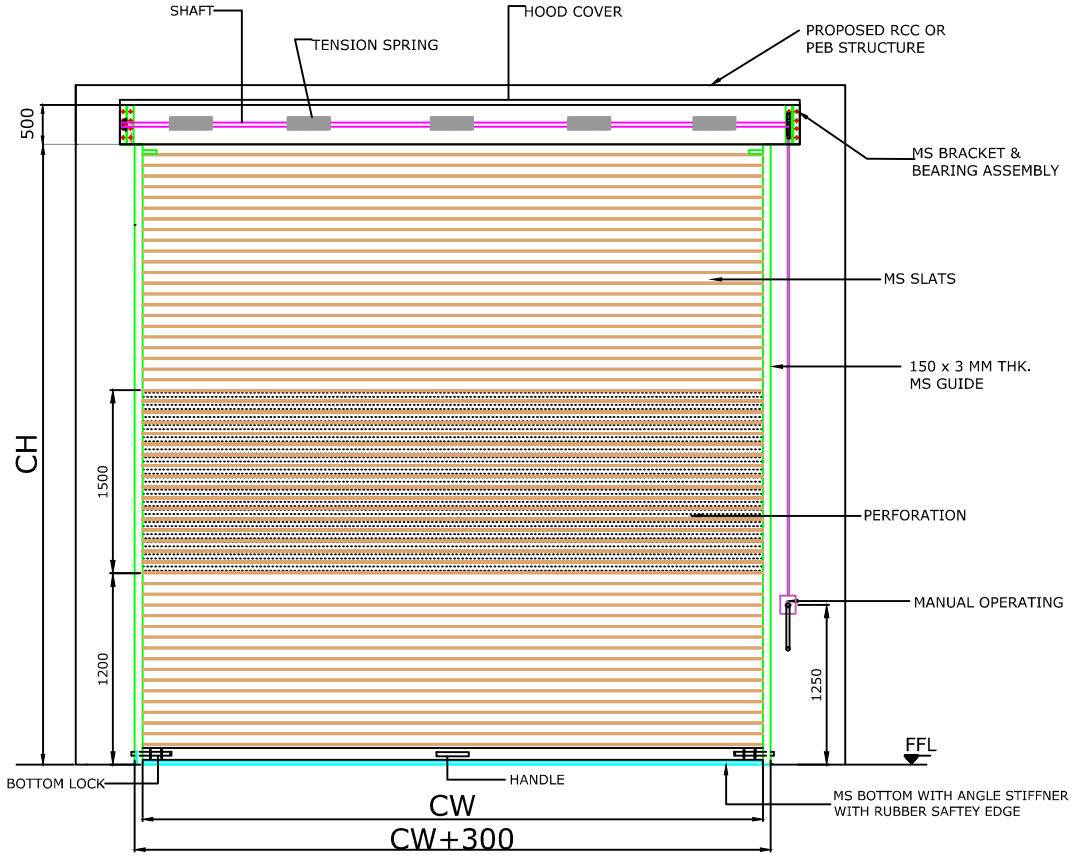


INSIDE ELEVATION

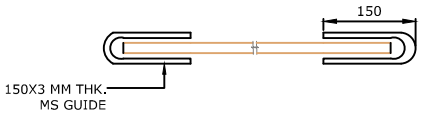

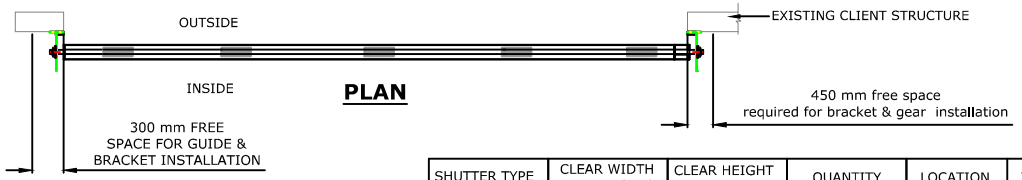

PLAN

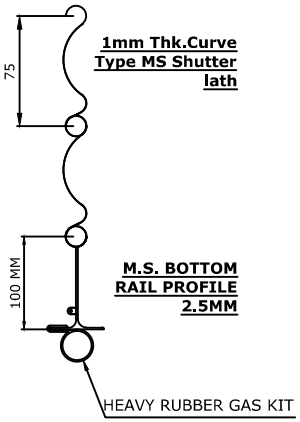

M.S. BOTTOM RAIL PROFILE 2.5MM

SHUTTER TYPE	CLEAR WIDTH (CW)	CLEAR HEIGHT (CH)	QUANTITY	LOCATION	INSTALLATION	REMARK
RS5	4700	5000	1	P1-Q1	INSIDE	REQUIRE STRUCTURE AT LEFT SIDE FOR GUIDE & BRACKET

DIMENSION :

CLEAR WIDTH	CLEAR HEIGHT	QUANTITY
4700	5000	1

MATERIAL:

THICKNESS :

NOTE:
1.REQUIRED STRUCTURE FOR ROLLING SHUTTER WILL BE CLIENT'S SCOPE.
2.ONE COAT OF RED OXIDE PRIMER WILL BE GIVEN TO THE SHUTTER.
3.FOR FINAL FINISH CLIENT SHOULD MENTION COLOR SHADE FOR ROLLING SHUTTER.

NIHVA TECHNOLOGIES PVT. LTD.
NIHVA TECHNOLOGIES PVT. LTD. PUNE
Email:- info@nihva.com
Website:- www.nihva.com

TITLE:

GEAR OPERATED ROLLING SHUTTER

CLIENT'S APPROVAL :

CLIENT - SCON

PROJECT - BEKAERT INDUSTRIES PVT. LTD.

SITE LOCATION - RANJANGAON

DWG. NO. : NIHVA/16-17/199

SCALE: NTS | WT: | SHEET:1 OF 1

DRAWN BY: SURAJ | DATE: 31-03-2017

CHECK BY : SAGAR P. | DATE: 31-03-2017

APPROVED BY : R.K | DATE: 31-03-2017

If any queries contact : projects@nihva.com

NOTE: ALL DIMENSIONS ARE IN mm

THIS DRAWING & DESIGN IS THE PROPERTY OF NIHVA TECHNOLOGIES. NOT TO BE SOLD OR COPIED TO ANY OTHER CONCERN.