

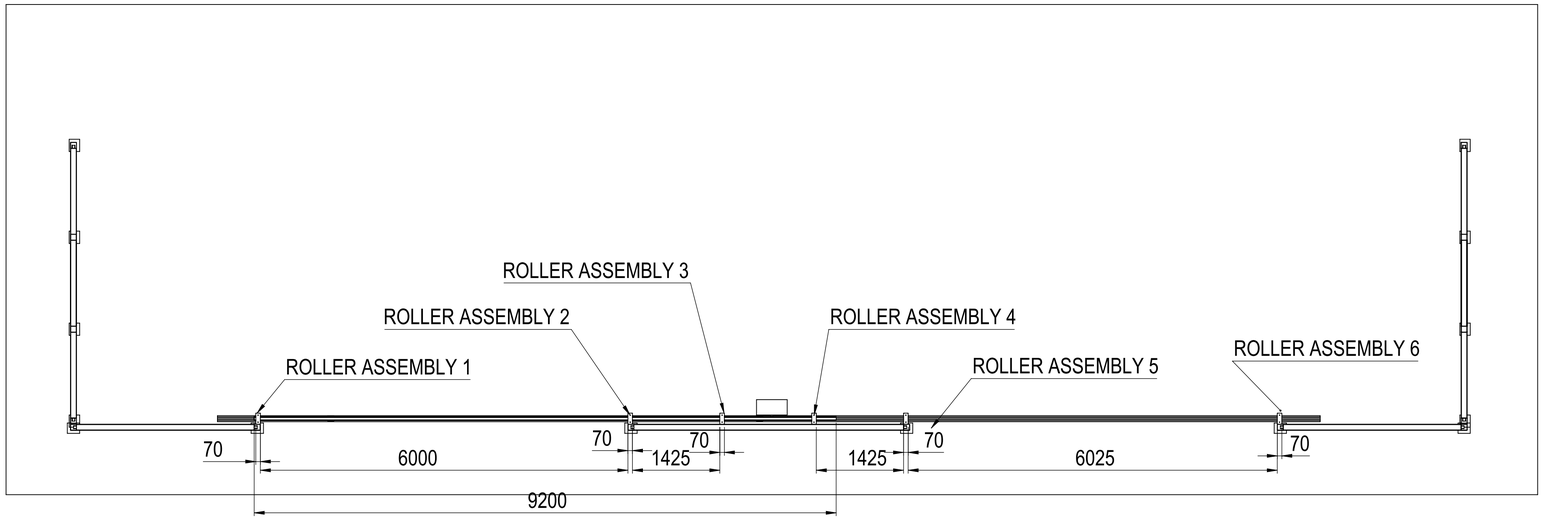



TOP VIEW

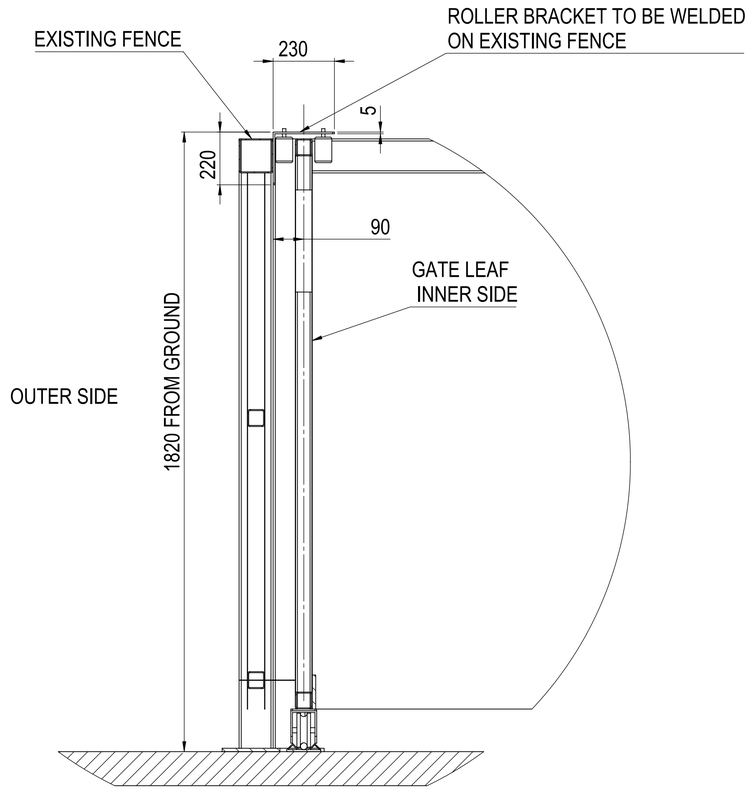

DETAIL B
SCALE 1 : 9

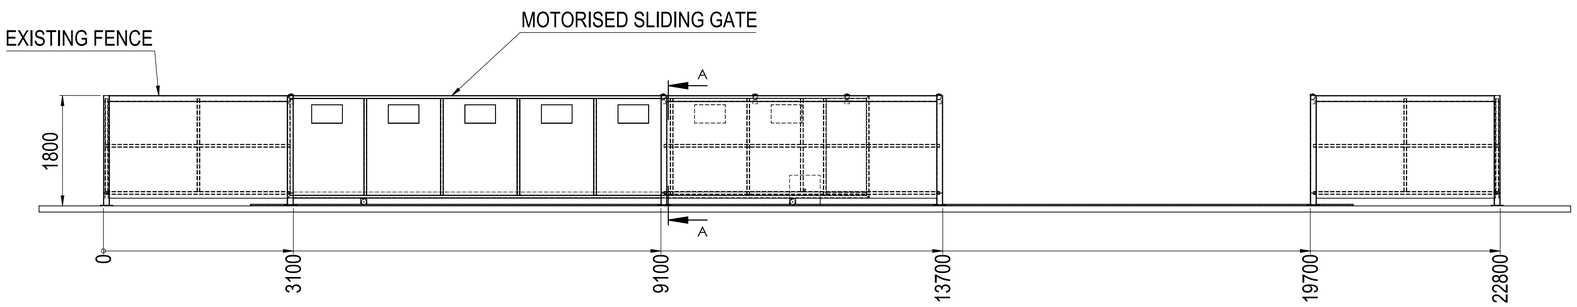

FRONT VIEW

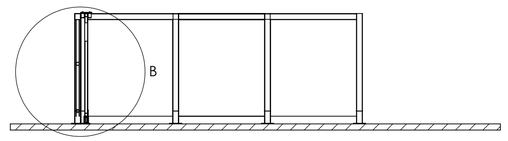

SECTION A-A
SCALE 1 : 50

UNLESS OTHERWISE SPECIFIED: DIMENSIONS ARE IN MILLIMETERS SURFACE FINISH: TOLERANCES: LINEAR: ANGULAR:		FINISH:		DEBURR AND BREAK SHARP EDGES	DO NOT SCALE DRAWING	REVISION
	NAME	SIGNATURE	DATE		TITLE: ROLLER BRACKET WELDING DWG	
DRAWN	SMS		16/9/20			
CHK'D	PA		16/9/20			
APP'VD						
MFG						
Q.A						
				MATERIAL: M.S.	DWG NO. Sliding Gate with Fence Position 1	A1
				WEIGHT:	SCALE:1:100	SHEET 1 OF 1