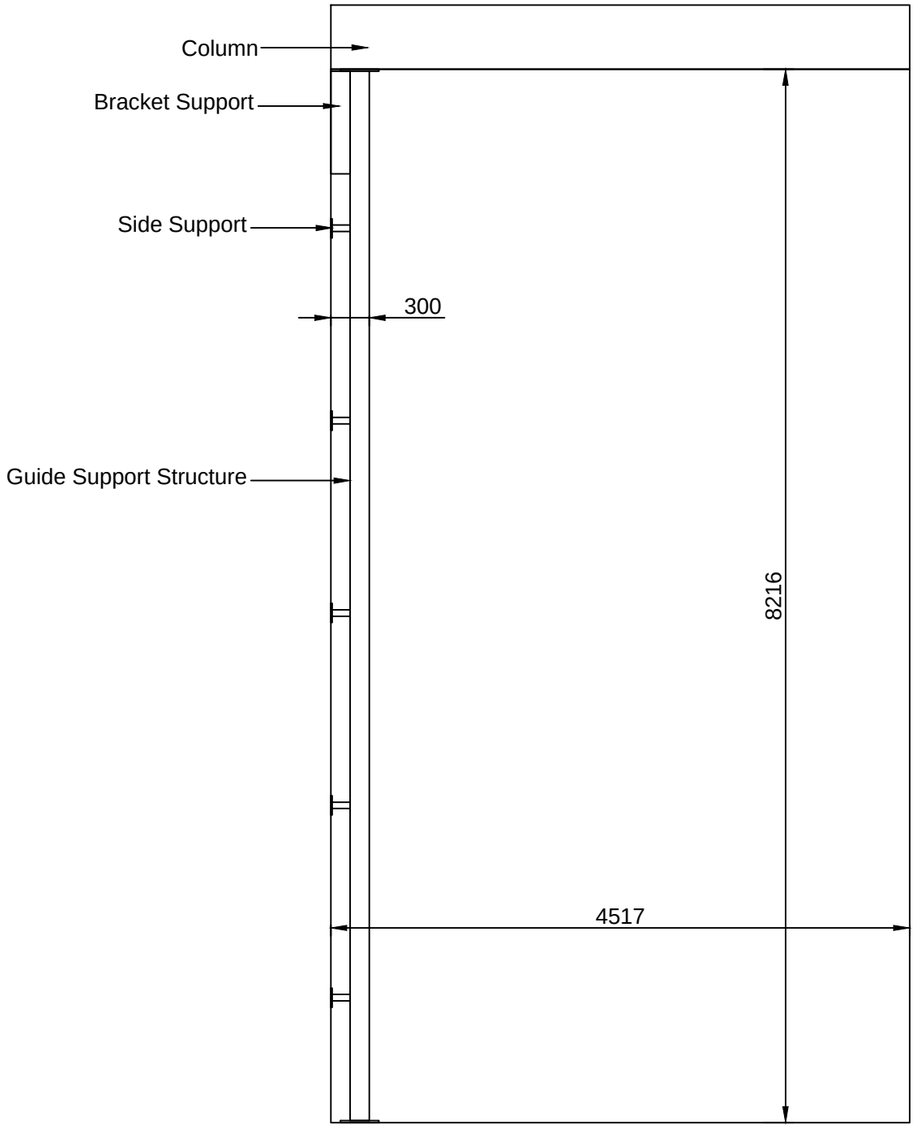

View From Outside

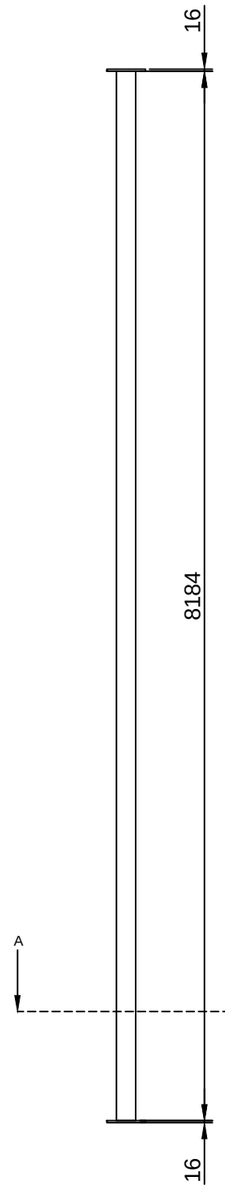

Guide Support Structure Assembly

Section A-A

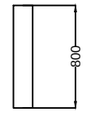

Bracket Support
SHS 150 x 150

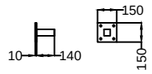

Side Support Ass.

DIMENSION :		
CLEAR WIDTH	CLEAR HEIGHT	QUANTITY
4215 mm	7900 mm	1 No

MATERIAL :

THICKNESS :

NOTE:-

NIHVA TECHNOLOGIES PVT. LTD.
NIHVA TECHNOLOGIES PVT. LTD. PUNE
Email:- info@nihva.com
Website:- www.nihva.com

TITLE:

DOUBLE WALL ROLLING SHUTTER STRUCTURE (1st Floor LH from inside)

CLIENT'S APPROVAL :

CLIENT - SEZ BIOTECH

PROJECT -

SITE LOCATION - PUNE

DWG. NO. : NIHVA/21-22/MFG/045

SCALE: NTS	WT:	SHEET:1 OF 1
DRAWN BY: G.P.		DATE: 29-03-2022
CHECKED BY: P.J.		DATE: 29-03-2022
APPROVED BY : A.K.		DATE: 29-03-2022

If any queries contact : design@nihva.com

NOTE: ALL DIMENSIONS ARE IN mm

THIS DRAWING & DESIGN IS THE PROPERTY OF NIHVA TECHNOLOGIES. NOT TO BE SOLD OR COPIED TO ANY OTHER CONCERN.