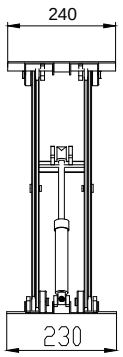

SECTION A-A
SCALE 1 : 10

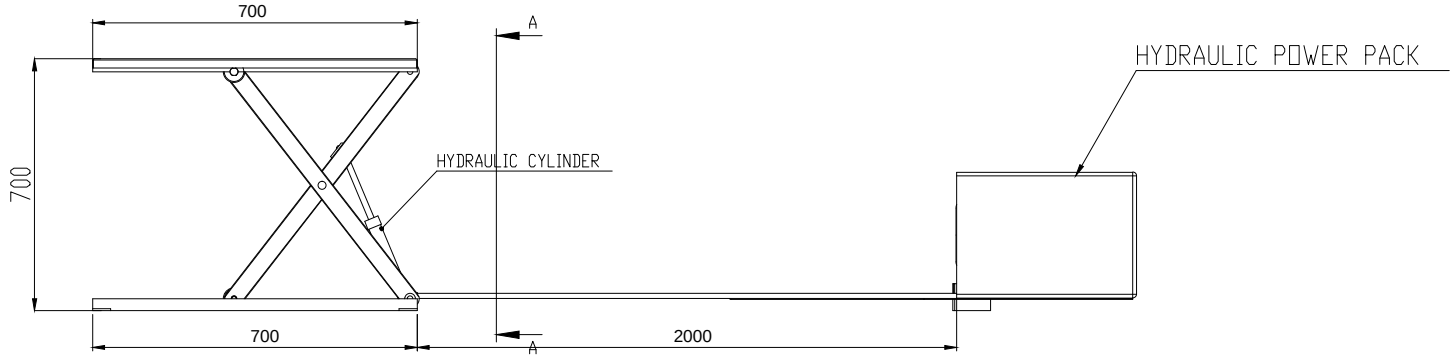

SECTION B-B
SCALE 1 : 10

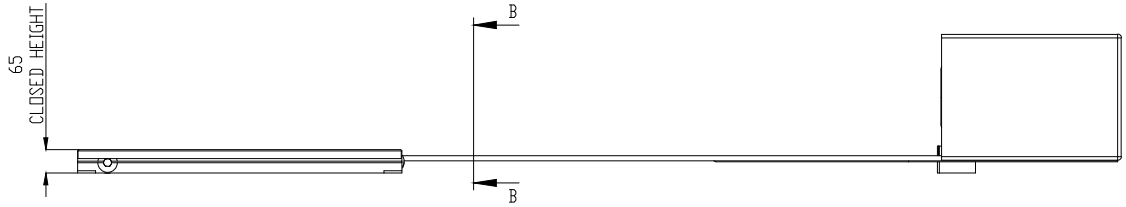

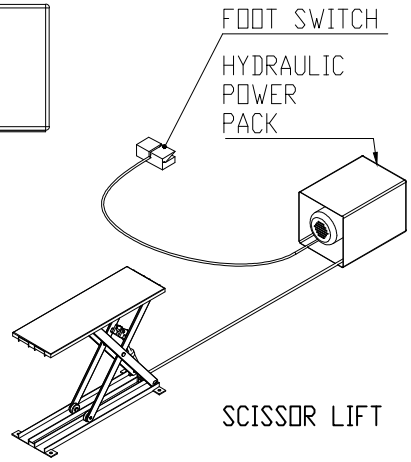

SCISSOR LIFT

SPECIFICATIONS:-
1. PLATFORM SIZE:- 700MMX240MM
2. LOADING CAPACITY:-150KG
3. LIFTING HEIGHT:- 700MM APPROX. HYDRAULIC LIFTING
4. LIFTING SPEED:- 8 SEC
5. CLOSED HEIGHT:-65MM
6. POWER CHORD:- 4M
7. METHOD OF OPERATION:- FOOT SWITCH (CHORD LENGTH 2M)

NOTE:- Allowable tolerence is ±1mm.

This drawing & designing is the property of NIHVA TECHNOLOGIES. Not be sold or copy to any other concern.

TITLE	SCISSOR LIFT		NIHVA TECHNOLOGIES PVT. LTD.
	SIGN	DATE	
DRAWN	OMKAR	06/08/16	CLIENT -
CHECK	ANIL	06/08/16	PROJECT -
REV.	01		SITE -
APPROVAL			DWG. NO. : NIHVA/16-17/0034/R01
If any queries contact : projects@nihva.com			SCALE: 01 / WT: / SHEET: 01 OF 01
ALL DIMENSION ARE IN mm			

NIHVA TECHNOLOGY PVT. LTD. PUNE
Tel : 020 66304033
Email:- info@nihva.com
Website:- www.nihva.com