
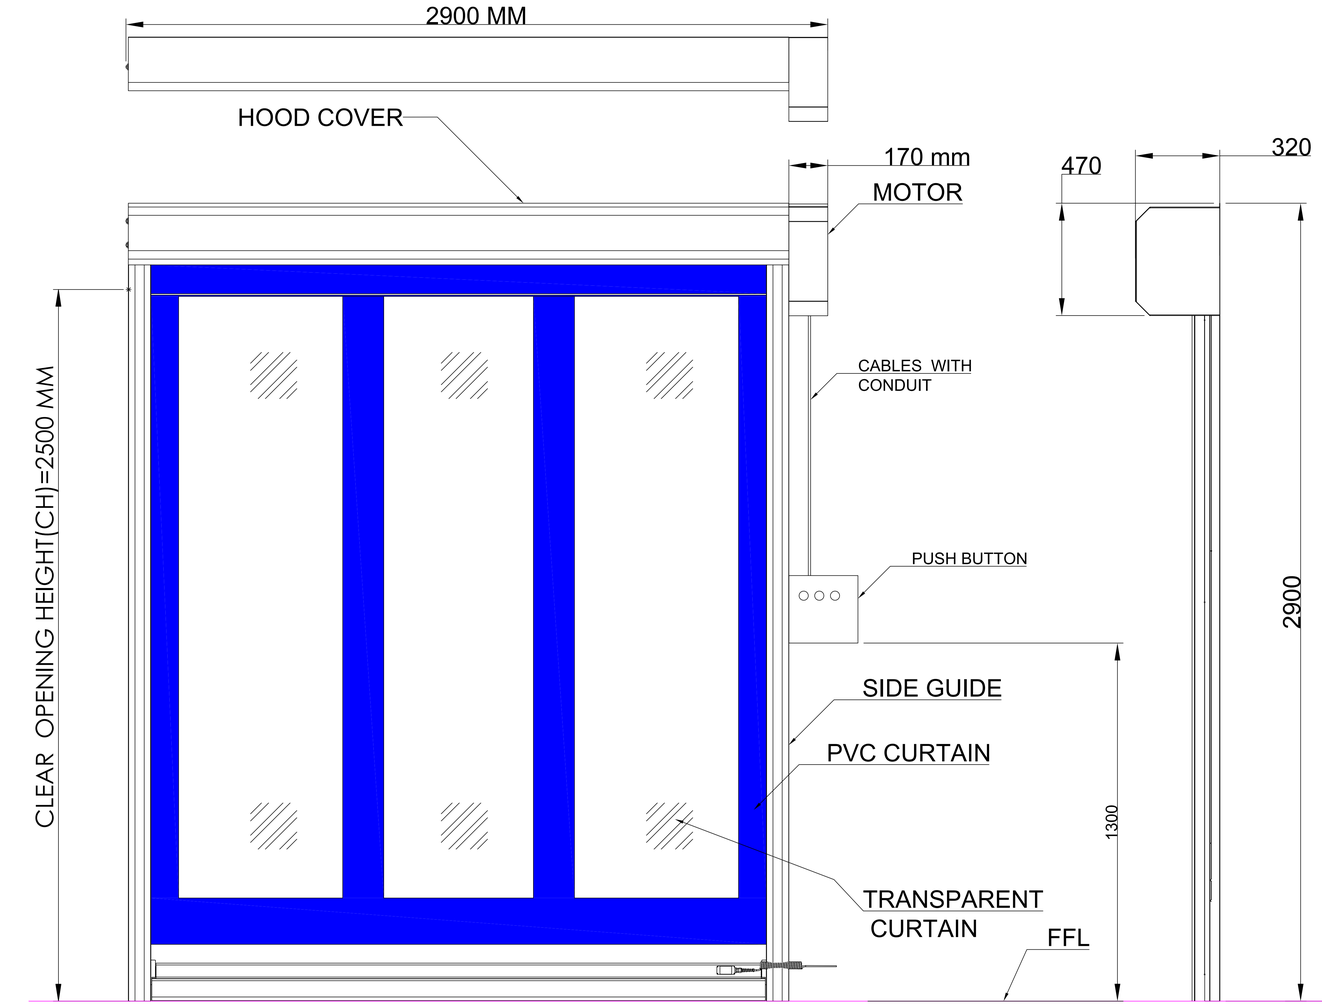


HIGH SPEED DOOR

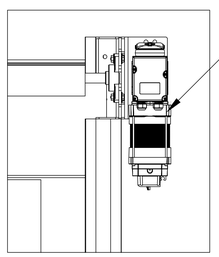


Speed	Inverter Motion system to adjust different speeds, with progressive control of acceleration & deceleration during braking		
	Opening Speed up to		3,0 m/s
	Closing Speed		0,8 m/s
Security Features	EN 13241-1		Standard
Resistance to Wind Load	EN 12424		up to Class 2
Curtain Stabilisation / Wind Load	Aluminium anodized windbars		Standard
Curtain	Fabric	0.9 - 1.5 mm	Standard
	Transparent PVC section	2.0 mm	Standard
Guide Material / Surface	Aluminium Anodized		Standard
	Painting in any RAL color		Optional
	Stainless Steel SS 316 matte finish		Optional
Shaft / Operator Cover	Straight		Optional
Operator and Control (German brand)	Connecting Voltage		220V - 1ph, N
	Open-Stop-Close Button		Standard
	Protection Category (Operator / Control)		IP 54 / IP 65
	Emergency-OFF Button		Standard
	Closing Zone Monitoring	Light Curtain	Optional
		optical safety edge	Standard
	External Route Monitoring	Photocell	Standard
	Door area Monitoring	Radar Presence Detector	Optional
		Induction Loop	Optional
	Electronic Limit Switch		Standard
Emergency Opening	Crank Handle		Standard
	Counterweight system		Optional
	Chain		Optional

NOTE:
1. REQUIRED STRUCTURE , FITTING & ALL CIVIL WORK IS IN CLIENT SCOPE.
2. STRUCTURE SHOULD BE RIGID & NEED TO BE FIXED/WELDED WITH EXISTING STRUCTURE AT SITE(IN CLIENT SCOPE).

RAL CODE FOR PVC CURTAIN-BLUE

2500	2500	1 NO	RH
CLEAR OPENING WIDTH (CW)	CLEAR OPENING HEIGHT (CH)	QUANTITY	MOTOR POSITION

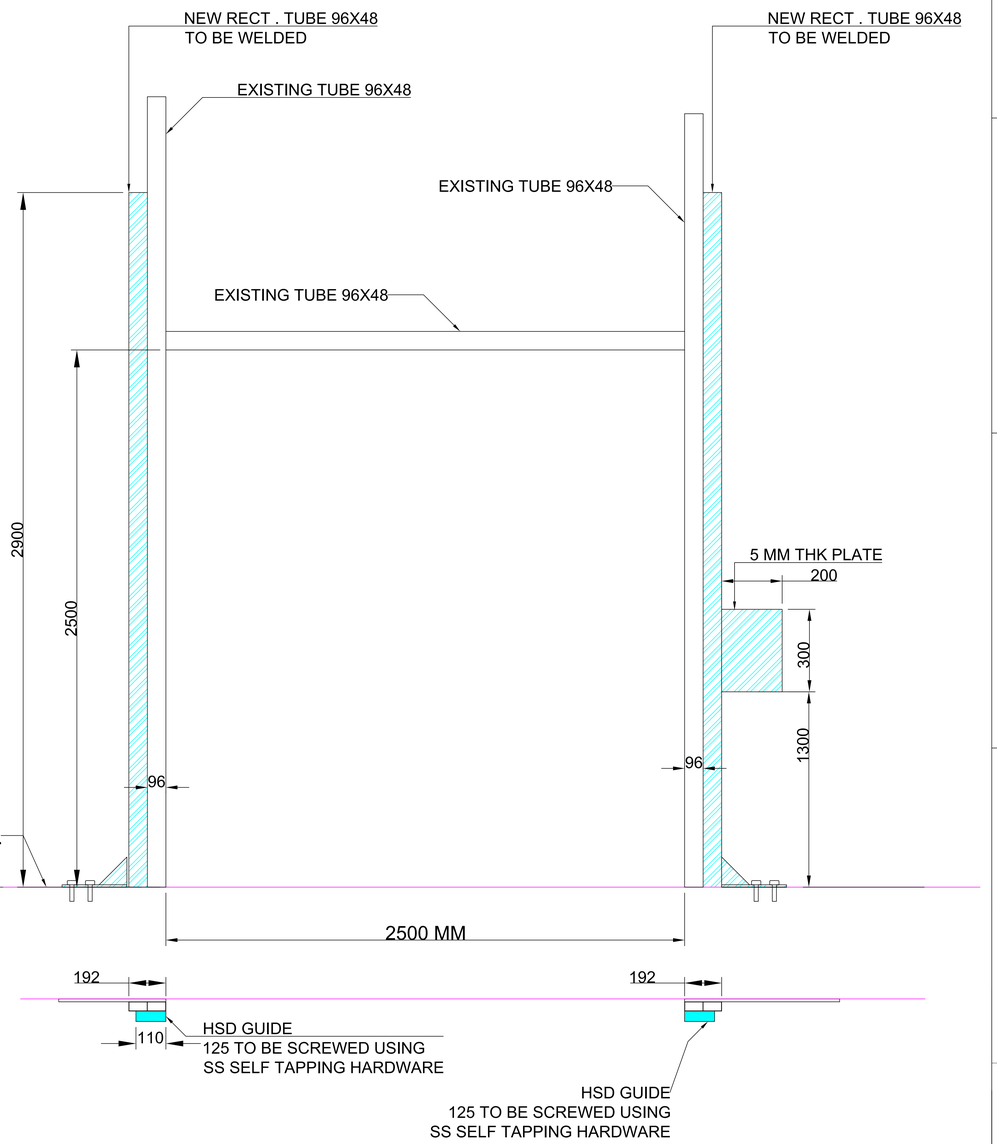

STRUCTURE DRAWING(CLIENT SCOPE)

This drawing & design is the property of NIHVA TECHNOLOGIES. Not to be sold or copied to any other concern.

TITLE	NIHVA MAKE HIGH SPEED DOOR 2500X2500		
	NAME	SIGN	DATE
DRAWN	S.M.S.		4.1.2021
CHECK	A.K.		4.1.2021
APPRD.			

NIHVA TECHNOLOGIES PVT. LTD.
NIHVA TECHNOLOGIES PVT. LTD. PUNE
Tel : 020 66304033
Email:- info@nihva.com
Website:- www.nihva.com

CLIENT -
PROJECT -
SITE LOCATION -
If any queries contact : design@nihva.com
DWG. NO. : NIHVA/20-21/VDR/0093
REV- R00
ALL DIMENSION ARE IN mm
SCALE: NTS
WT:
SHEET: 1 OF 1