

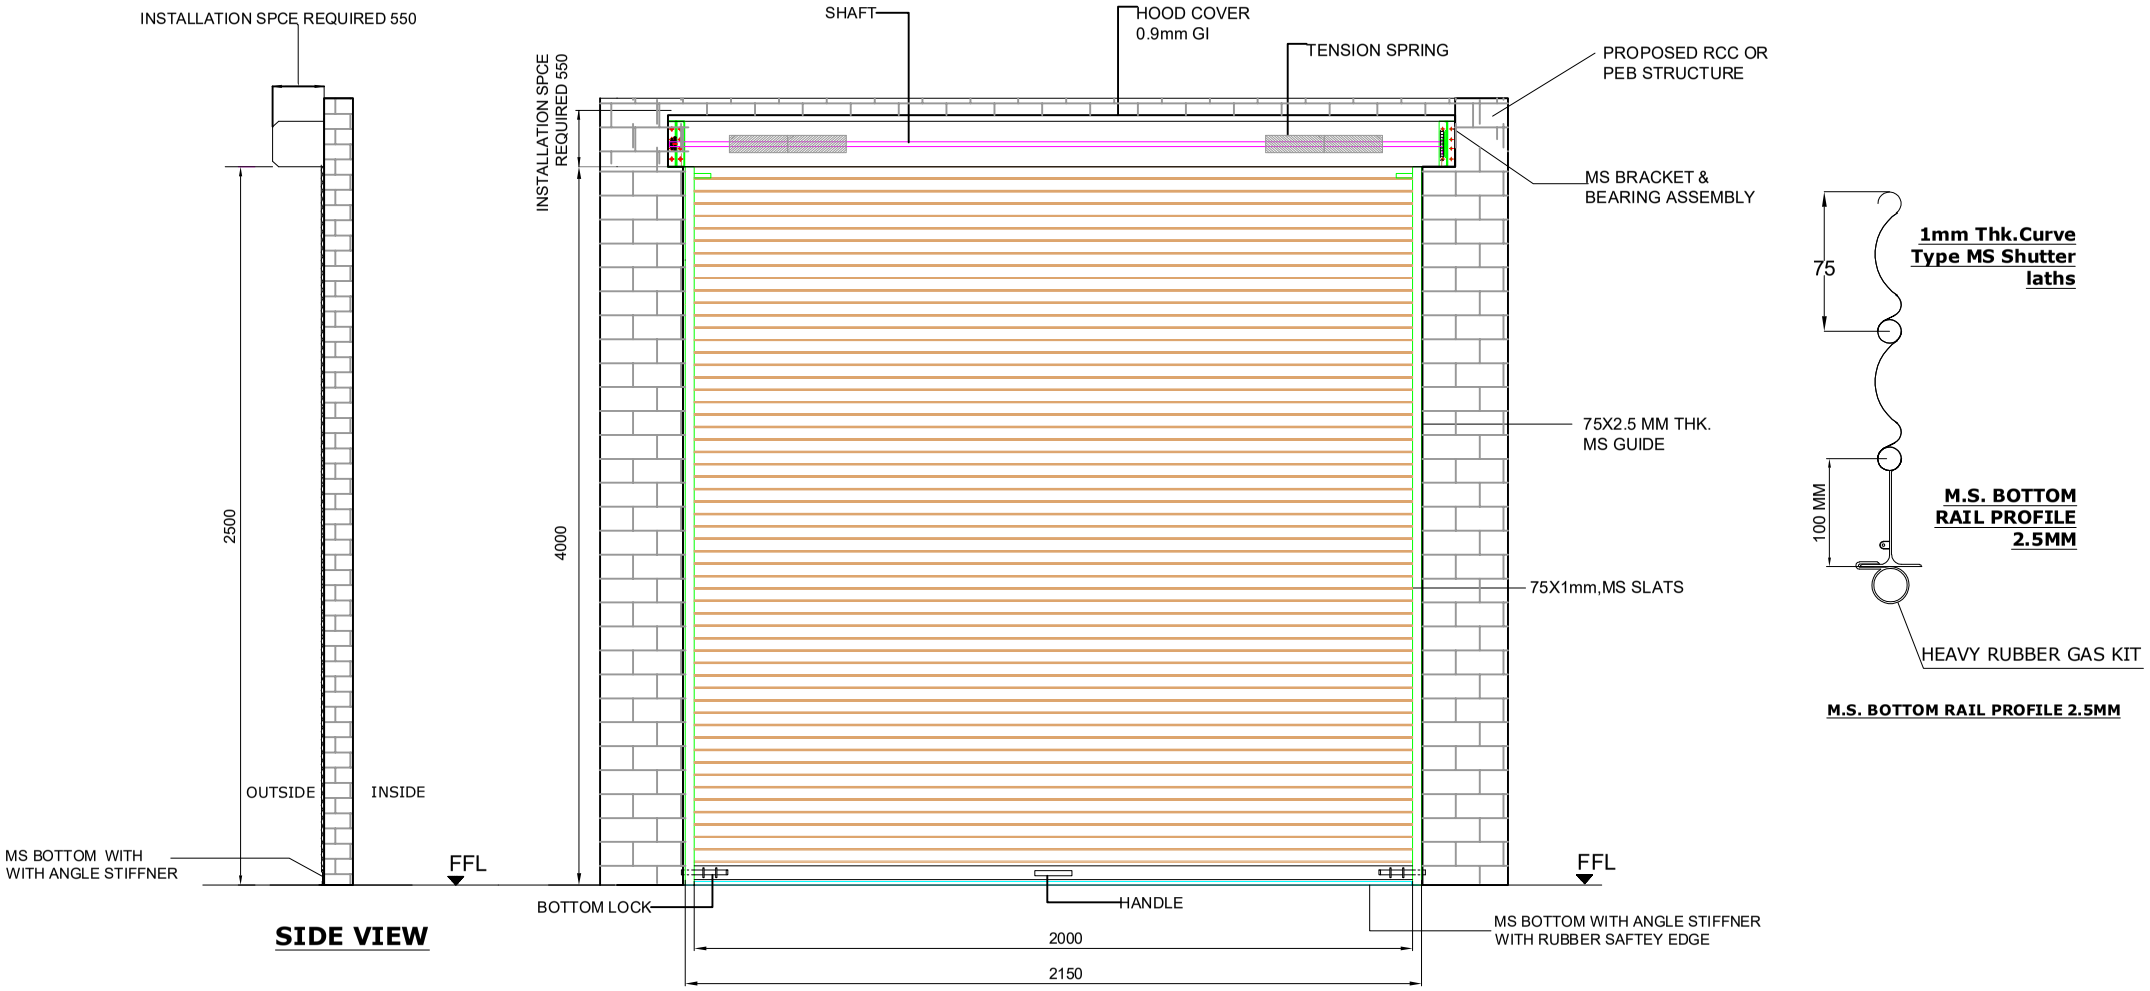


M.S. BOTTOM RAIL PROFILE 2.5MM

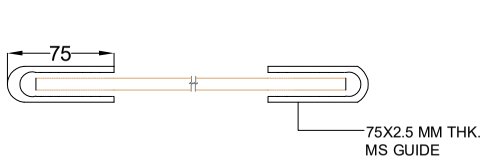

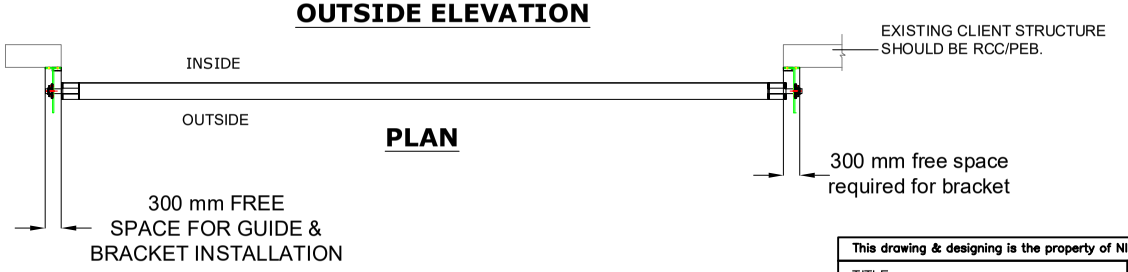

RAL CODE	SHADE	COLOUR
RAL 5002	ULTRAMARINE BLUE	
RAL 7035	LIGHT GREY	
RAL 7001	SILVER GREY	

NOTE:-

1. ALL CIVIL WORK WILL BE IN CLIENT SCOPE.
2. SURFACE FINISH: POWDER COATING OF APPROVED RAL CODE.
3. MOUNTING: ON CONCRETE COLUMN / WALL
4. IF STRUCTURE REQUIRED WILL BE IN CLIENT SCOPE.
5. GIVEN DRAWING IS ONLY FOR THE CLIENT UNDERSTANDING PURPOSE.
   ACTUAL DIMENSION AND PRODUCT PARTS MAY VARY AS PER SITE CONDITION AND CLIENT REQUIREMENTS

TOLERANCE - ±10mm

DW	DH	QTY
2000MM	2500MM	02

This drawing & designing is the property of NIHVA TECHNOLOGIES. Not to be sold or copied to any other concern.

TITLE: **Push & Pull Single Skin Rolling Shutter**

NIHVA TECHNOLOGIES PVT. LTD.

	SIGN	DATE
DRAWN	SUJATA	25/04/2022
CHECK	A.K	25/04/2022
APPROVAL	V.T	25/04/2022

CLIENT -

PROJECT - PUSH PULL ROLLING SHUTTER

SITE -PUNE

DWG. NO. : NIHVA/22-23/CLT/0196 | REV-00

If any queries contact : design1@nihva.com | SCALE: NTS | WT: | SHEET: 01 OF 01

ALL DIMENSION ARE IN mm